CÔNG TY TNHH DESIGN AND CONSTRUCTION NEW MAXHOME
HÀ NỘI

HỒ SƠ THIẾT KẾ KỸ THUẬT THI CÔNG

CÔNG TRÌNH: NHÀ Ở GIA ĐÌNH

CHỦ ĐẦU TƯ: CHỊ : NGUYỄN THỊ ÁNH NGUYỆT

ĐỊA ĐIỂM: NAM HỒNG - HÀ TĨNH

HẠNG MỤC KẾT CẤU

THỰC HIỆN

HẢNG A LAO

KIỂM DUYỆT

NGUYỄN TẤT HỘI

HÀ NỘI, THÁNG 12 NĂM 2025

GHI CHÚ CHUNG

1. ĐẶC ĐIỂM CÔNG TRÌNH

- HẠNG MỤC : THIẾT KẾ CHI TIẾT NHÀ Ở THẤP TẦNG
- CẤP CHỐNG ĐỘNG ĐẤT : KHÔNG THIẾT KẾ KHÁNG CHẤN
- TẢI TRỌNG GIÓ : CÔNG TRÌNH TÍNH TOÁN VỚI 100% TẢI TRỌNG GIÓ TIÊU CHUẨN CỦA VÙNG XÂY DỰNG
- GIẢI PHÁP KẾT CẤU PHẦN THÂN : HỆ KHUNG DẦM BTCT. KẾT CẤU SÀN GỒM CÁC Ô BẢN SÀN BTCT TOÀN KHỐI
- GIẢI PHÁP XỬ LÝ NỀN VÀ MÓNG : MÓNG CỌC BÊ TÔNG CỐT THÉP
- THIẾT KẾ MÓNG THEO GIẢ ĐỊNH VÌ CHƯA CÓ BÁO CÁO KHẢO SÁT ĐỊA CHẤT DO CHỦ ĐẦU TƯ CUNG CẤP

2. CÁC TIÊU CHUẨN ÁP DỤNG CHO CÔNG TRÌNH

BẢNG 1.

STT	TÀI LIỆU	KÍ HIỆU
1	– QUY CHUẨN XÂY DỰNG VIỆT NAM HIỆN HÀNH	
2	– TẢI TRỌNG VÀ TÁC ĐỘNG – TIÊU CHUẨN THIẾT KẾ	TCVN 2737 – 2023
3	– KẾT CẤU GẠCH ĐÁ VÀ GẠCH ĐÁ CỐT THÉP. TIÊU CHUẨN THIẾT KẾ	TCVN 5573 – 2011
4	– KẾT CẤU BÊ TÔNG CỐT THÉP. TIÊU CHUẨN THIẾT KẾ	TCVN 5574 – 2018
5	– KẾT CẤU THÉP. TIÊU CHUẨN THIẾT KẾ	TCVN 5575 – 2018
6	– NHÀ CAO TẦNG. HƯỚNG DẪN THIẾT KẾ BÊ TÔNG CỐT THÉP TOÀN KHỐI	TCVN 198 – 1997
7	– TIÊU CHUẨN THIẾT KẾ CÔNG TRÌNH CHỊU ĐỘNG ĐẤT	TCVN 9386 – 2012
8	– KẾT CẤU BTCT YÊU CẦU CẦN BẢO VỆ CHỐNG ĂN MÒN TRONG MÔI TRƯỜNG BIỂN	TCVN 9346 – 2012
9	– TIÊU CHUẨN THIẾT KẾ NỀN NHÀ VÀ CÔNG TRÌNH	TCVN 9362 – 2012
10	– MÓNG CỌC – TIÊU CHUẨN THIẾT KẾ	TCVN 10304 – 2014
11	– XI MĂNG XÂY TRÁT	TCVN 9202 – 2012
12	– THÉP CỐT BÊ TÔNG	TCVN 1651 – 2008

3. TẢI TRỌNG TÁC ĐỘNG

BẢNG 2.

	HOẠT TẢI SỬ DỤNG	TẢI ĐƠN VỊ	HỆ SỐ ĐỘ TIN CẬY
1	– SÀN CẦU THANG	300 (KG/M2)	1.2
2	– SÀN HÀNH LANG	300 (KG/M2)	1.2
3	– SÀN BAN CÔNG VÀ LOGIA	200 (KG/M2)	1.2
4	– SÀN VĂN PHÒNG LÀM VIỆC	200 (KG/M2)	1.2
5	– SÀN PHÒNG HỌP VÀ HỘI TRƯỜNG	400 (KG/M2)	1.2
6	– SÀN PHÒNG NGỦ CĂN HỘ	150 (KG/M2)	1.3
7	– SÀN VỆ SINH CĂN HỘ	150 (KG/M2)	1.3
8	– SÀN PHÒNG NGỦ KHÁCH SẠN	200 (KG/M2)	1.2
9	– SÀN PHÒNG KHÁCH	200 (KG/M2)	1.2
10	– SÀN VỆ SINH KHU VĂN PHÒNG	200 (KG/M2)	1.2
11	– SÀN KINH DOANH CỬA HÀNG VÀ ĂN UỐNG	300 (KG/M2)	1.2
12	– SÀN CỬA HÀNG TRƯNG BÀY VÀ SIÊU THỊ	400 (KG/M2)	1.2
13	– SÀN GARA ÔTÔ	500 (KG/M2)	1.2
14	– SÀN PHÒNG MÁY	750 (KG/M2)	1.2
15	– SÀN MÁI BẰNG CÓ SỬ DỤNG	150 (KG/M2)	1.3
16	– SÀN MÁI BẰNG KHÔNG SỬ DỤNG	75 (KG/M2)	1.3
17	– SÀN MÁI TÔN KHÔNG SỬ DỤNG	30 (KG/M2)	1.3

BẢNG 3.

STT	TĨNH TẢI	TRỌNG LƯỢNG RIÊNG	HỆ SỐ ĐỘ TIN CẬY
1	– BÊ TÔNG	2500 (KG/M3)	1.1
2	– VỮA LÓT	1800 (KG/M3)	1.3
3	– VỮA TRÁT	1800 (KG/M3)	1.3
4	– GẠCH LÁT	2000 (KG/M3)	1.1
5	– GẠCH ĐẶC	1800 (KG/M3)	1.1
6	– GẠCH LỖ	1400 (KG/M3)	1.1
7	– GẠCH BÊ TÔNG KHÍ TRƯNG ÁP	900 (KG/M3)	1.1

BẢNG 4.

	HOẠT TẢI GIÓ	TẢI ĐƠN VỊ	HỆ SỐ ĐỘ TIN CẬY
1	KHU VỰC XÂY DỰNG	..... (KG/M2)	1.2

4. CÁC YÊU CẦU KHI THI CÔNG

1. PHẢI CÓ BIỆN PHÁP THI CÔNG ĐỂ ĐẢM BẢO AN TOÀN CHO CÁC CÔNG TRÌNH LÂN CẬN.
2. NHÀ THẦU PHẢI CÓ BIỆN PHÁP BẢO DƯỠNG THI CÔNG TRONG QUÁ TRÌNH THI CÔNG.
3. TẠI CHỖ GIAO CỦA CỘT (HOẶC TƯỜNG) VÀ DẦM (HOẶC SÀN) MÁC BÊ TÔNG LẤY BẰNG MÁC BÊ TÔNG CỦA CỘT (HOẶC TƯỜNG) TẦNG DƯỚI. TRONG VÙNG NÀY VIỆC THI CÔNG PHẢI HẾT SỨC CẨN THẬN, ĐẦM RUNG BÊ TÔNG THẬT KỸ.
4. SÀN CÓ BƯỚC >4M YÊU CẦU KHI CHỐNG COFFRAGE PHẢI TẠO ĐỘ VỒNG F=1/400 Ở GIỮA NHỊP VÀ CONSOLE TỪ 1M TRỞ LÊN PHẢI TẠO ĐỘ VỒNG F=1/250.
5. CƯỜNG ĐỘ BÊ TÔNG CỦA DẦM CONSOLE, SÀN KHÔNG DẦM PHẢI ĐẠT 100% CƯỜNG ĐỘ MỚI ĐƯỢC THÁO DỠ COFFRAGE.
6. TẤT CẢ CÁC SÀN BÊ TÔNG CÓ TRẦN BÊN DƯỚI, PHẢI CHỜ SẴN CÁC THANH NEO TRONG SÀN.
7. PHẢI CÓ SỰ PHỐI HỢP CHẶT CHẼ CÁC BẢN VẼ THI CÔNG CHUYÊN MÔN: KẾT CẤU, KIẾN TRÚC, ĐIỆN NƯỚC, PCCC, ĐIỀU HÒA,....ĐẶT CÁC ĐƯỜNG ỐNG VÀ ỐNG NỐI, KIỂM TRA CÁC LỖ MỞ. ĐỘ CHÍNH XÁC CÁC BỘ PHẬN ĐẶT CHỜ, TRÁNH KHOAN ĐỤC VÀO KẾT CẤU CHỊU LỰC.
8. NẾU NỘI DUNG TRONG GHI CHÚ CHUNG KHÔNG PHÙ HỢP THÌ LẤY GHI CHÚ TRONG BẢN VẼ CHI TIẾT LÀM CHUẨN
9. SAI SỐ CHO PHÉP KHI ĐỔ SÀN BÊ TÔNG KHÔNG DẦM LÀ F=1MM
10. CÔNG TÁC QUAN TRẮC BIẾN DẠNG CÔNG TRÌNH PHẢI ĐƯỢC TIẾN HÀNH NGAY TỪ KHI THI CÔNG HỐ MÓNG BAO GỒM :
    + QUAN TRẮC LÚN VÀ CHUYỂN VỊ NGANG THÀNH HỐ MÓNG BẰNG VIỆC CHÔN CÁC MỐC SÂU Ở ĐÁY VÀ THÀNH HỐ MÓNG.
    + QUAN TRẮC LÚN THEO THỜI GIAN BẰNG PHƯƠNG PHÁP ĐỊNH KỲ THỦY CHUẨN. MÁY ĐO LÚN CÓ THỂ DÙNG CÁC LOẠI MÁY NI002, NI004 HOẶC CÁC MÁY KHÁC CÓ ĐỘ CHÍNH XÁC TƯƠNG ĐƯƠNG.
    + TRƯỚC VÀ SAU KHI THI CÔNG HỐ MÓNG ĐỀU PHẢI QUAN TRẮC LÚN, SAU KHI HOÀN THÀNH THI CÔNG 1 TẦNG PHẢI TIẾN HÀNH QUAN TRẮC LÚN 1 LẦN, TIẾP TỤC CHO ĐẾN KHI CÔNG TRÌNH HOÀN THÀNH.
    + SAU KHI HOÀN THÀNH CÔNG TRÌNH : TIẾN HÀNH QUAN TRẮC LÚN 4 LẦN CHO NĂM ĐẦU TIÊN. TỪ NĂM THỨ 2 TRỞ ĐI, QUAN TRẮC 2 LẦN MỘT NĂM CHO ĐẾN KHI ĐỘ LÚN 2 LẦN MỘT NĂM CHO ĐẾN KHI ĐỘ LÚN ỔN ĐỊNH.
11. NGOÀI CÁC GHI CHÚ ĐẶC BIỆT Ở ĐÂY, CÁC QUY ĐỊNH KHÁC ĐỀU PHẢI TUÂN THEO CÁC TIÊU CHUẨN HIỆN HÀNH.
12. TRƯỚC KHI THI CÔNG YÊU CẦU GIA ĐÌNH LIÊN HỆ KỸ THUẬT CÔNG TY HƯỚNG DẪN BIỆN PHÁP THI CÔNG HOẶC NGHIỆM THU GIAI ĐOẠN NẾU CÓ SAI SÓT TRONG BẢN VẼ VUI LÒNG LIÊN HỆ KỸ THUẬT KIỂM TRA TƯ VẤN TRƯỚC KHI TRIỂN KHAI

CHỦ ĐẦU TƯ CẦN YÊU CẦU KỸ SƯ HIỆN TRƯỜNG KIỂM TRA - RÀ SOÁT BẢN VẼ TRƯỚC KHI THI CÔNG
NẾU CÓ THẮC MẮC VUI LÒNG LIÊN HỆ KIẾN TRÚC SƯ - KỸ SƯ THIẾT KẾ ĐỂ CÓ TƯ VẤN KỊP THỜI TRƯỚC KHI KHỞI CÔNG

HỖ TRỢ TƯ VẤN KỸ THUẬT XÂY DỰNG : 0924099999
LIÊN HỆ MUA VẬT LIỆU MAXHOME : 0921845555 (MIỄN PHÍ VẬN CHUYỂN TOÀN QUỐC)

–BÊ TÔNG LÓT MÓNG ĐÁ 4X6, MÁC 100 –BÊ TÔNG MÓNG, MÁC 250	–BÊ TÔNG CỘT, DẦM, SÀN MÁC 250 –LỚP BÊ TÔNG BẢO VỆ SÀN: 15MM	–LỚP BÊ TÔNG BẢO VỆ CỐT THÉP DẦM: 25MM –LỚP BÊ TÔNG BẢO VỆ CỐT THÉP CỘT: 25MM	–THÉP CB240T (ø<10) KÝ HIỆU (ø) CÓ RA=2100KG/CM2 –THÉP CB300V (10=<ø<=20) KÝ HIỆU (ø) CÓ RA=2600KG/CM2	–THÉP CB300V (20<ø) KÝ HIỆU (ø) CÓ RA=2600KG/CM2 –CHIỀU DÀI THÉP NEO TẠI CÁC VỊ TRÍ LẤY BẰNG 30D	–CẮT NỐI UỐN CỐT THÉP THEO TCXDVN 5574–2018. –KHI THI CÔNG CẦN KẾT HỢP BẢN VẼ KIẾN TRÚC

CÔNG TY TNHH DESIGN AND CONSTRUCTION NEW MAXHOME
HÀ NỘI
ĐC : TẦNG 25, TÒA NHÀ VP TTTM CHỢ MƠ
SỐ 459C PHỐ BẠCH MAI, P. BẠCH MAI
THÀNH PHỐ HÀ NỘI
TEL: 0964458888 - 0828133333

Chủ đầu tư:
NGUYỄN THỊ ÁNH NGUYỆT

Địa điểm:
NAM HỒNG - HÀ TĨNH

Tên công trình:
NHÀ Ở GIA ĐÌNH

HỢP ĐỒNG SỐ /HĐ-TK/20.....

CHỦ NHIỆM THIẾT KẾ KTS: NGUYỄN VĂN CƯỜNG	
TRIỂN KHAI KS: HÀNG A LAO	
KIỂM DUYỆT KTS: NGUYỄN TẤT HỘI	

NỘI DUNG ĐIỀU CHỈNH

Lần	Ngày	Duyệt
1	.....	.....
2	.....	.....
3	.....	.....
4	.....	.....
5	.....	.....
6	.....	.....
7	.....	.....


Hạng mục:
KẾT CẤU

Tên bản vẽ:
GHI CHÚ CHUNG


	Hà Nội, 12-2025
Phát hành lần 01	Thiết kế
.....	**KC-00**


GHI CHÚ CHUNG

5. CHI TIẾT GIA CƯỜNG DẦM TẠI VỊ TRÍ GIAO NHAU

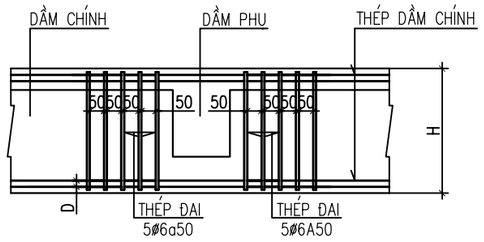


6. CHI TIẾT GIA CƯỜNG DẦM TẠI VỊ TRÍ CỘT CHỐNG LÊN DẦM CHÍNH

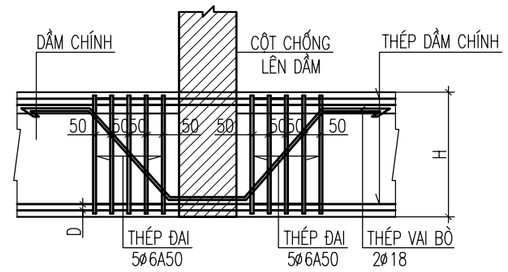


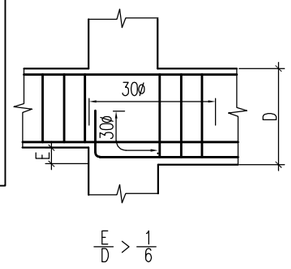

7. CHI TIẾT CẤU TẠO NÚT KHUNG

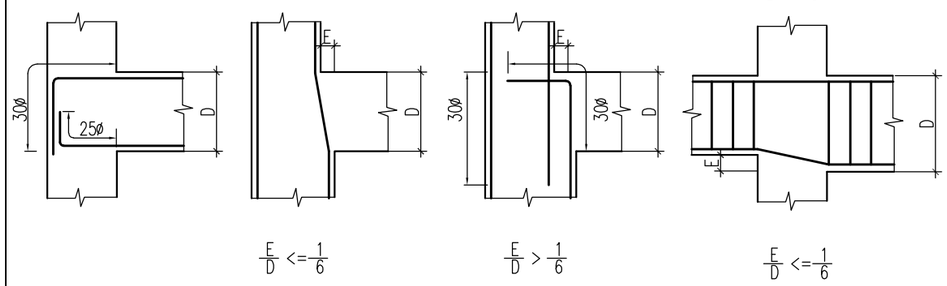


8. CHI TIẾT LIÊN KẾT CỘT VÀ TƯỜNG

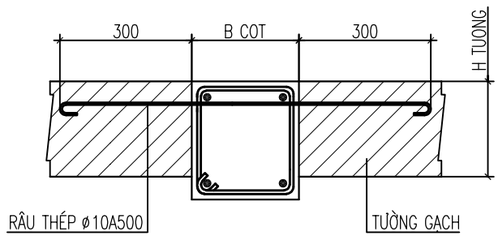

T. CHỈ DẪN CHUNG NỐI CỐT THÉP DẦM SÀN:

(1). NỐI CỐT THÉP DẦM (ÁP DỤNG CHO DẦM DƯỚI CỐT 0.00 M) :


THÉP CHỊU LỰC THEO PHƯƠNG CẠNH NGẮN NÊN NẰM GẦN MÉP BÊ TÔNG NHẤT

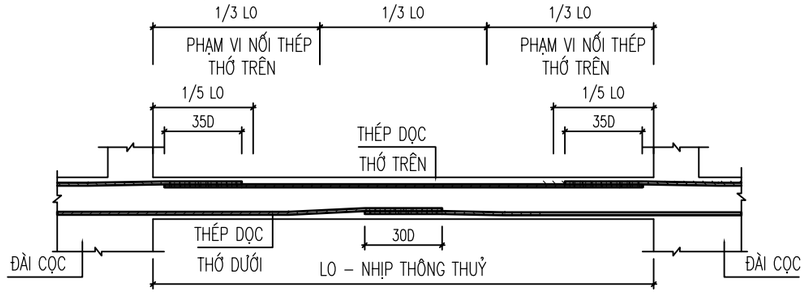


(2). NỐI CỐT THÉP SÀN (ÁP DỤNG CHO SÀN DƯỚI CỐT 0.00 M) :


– VỚI CỐT THÉP PHÂN BỐ ĐỀU TRÊN CÙNG VỊ TRÍ PHẢI NỐI SO LE (CÁCH 1 THANH NỐI 1 THANH).

– KHOẢNG CÁCH GIỮA CÁC VỊ TRÍ NỐI PHẢI >= 30D

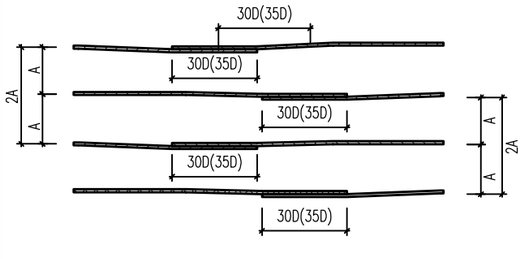

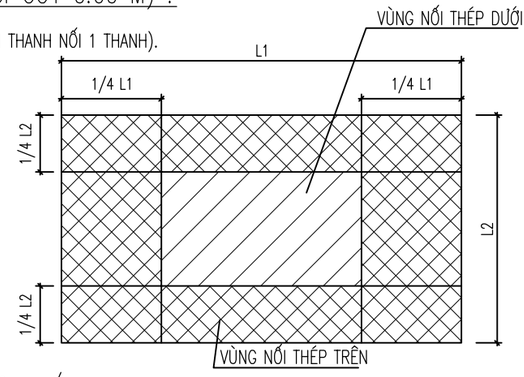


(3). NỐI CỐT THÉP DẦM (ÁP DỤNG CHO DẦM TRÊN CỐT 0.00 M) :

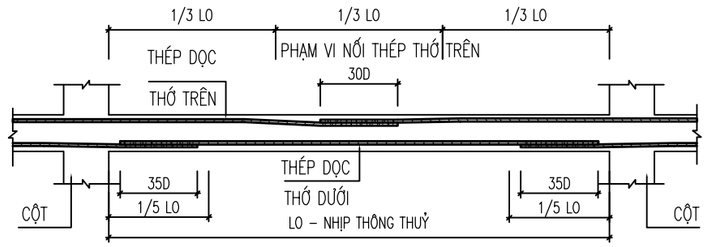


(4). NỐI CỐT THÉP SÀN (ÁP DỤNG CHO SÀN TRÊN CỐT 0.00 M) :

– VỚI CỐT THÉP PHÂN BỐ ĐỀU TRÊN CÙNG VỊ TRÍ PHẢI NỐI SO LE

– KHOẢNG CÁCH GIỮA CÁC VỊ TRÍ NỐI PHẢI >= 30D

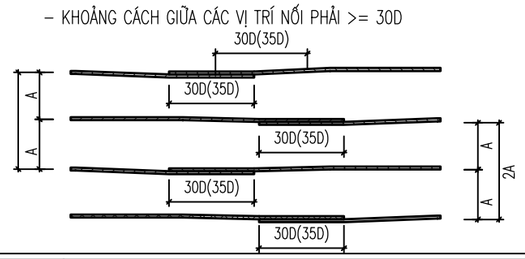

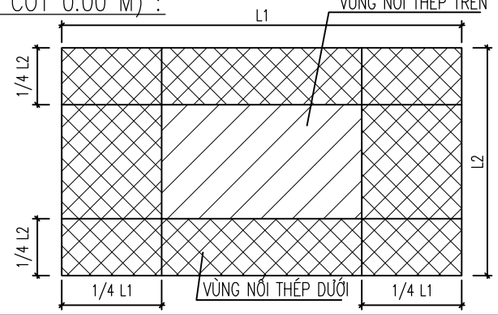

CHỦ ĐẦU TƯ CẦN YÊU CẦU KỸ SƯ HIỆN TRƯỜNG KIỂM TRA - RÀ SOÁT BẢN VẼ TRƯỚC KHI THI CÔNG
NẾU CÓ THẮC MẮC VUI LÒNG LIÊN HỆ KIẾN TRÚC SƯ - KỸ SƯ THIẾT KẾ ĐỂ CÓ TƯ VẤN KỊP THỜI TRƯỚC KHI KHỞI CÔNG

HỖ TRỢ TƯ VẤN KỸ THUẬT XÂY DỰNG : 0924099999
LIÊN HỆ MUA VẬT LIỆU MAXHOME : 0921845555 (MIỄN PHÍ VẬN CHUYỂN TOÀN QUỐC)

–BÊ TÔNG LÓT MÓNG ĐÁ 4X6, MÁC 100 –BÊ TÔNG MÓNG, MÁC 250	–BÊ TÔNG CỘT, DẦM, SÀN MÁC 250 –LỚP BÊ TÔNG BẢO VỆ SÀN: 15MM	–LỚP BÊ TÔNG BẢO VỆ CỐT THÉP DẦM: 25MM –LỚP BÊ TÔNG BẢO VỆ CỐT THÉP CỘT: 25MM	–THÉP CB240T (ø<10) KÝ HIỆU (ø) CÓ RA=2100KG/CM2 –THÉP CB300V (10=<ø<=20) KÝ HIỆU (ø) CÓ RA=2600KG/CM2	–THÉP CB300V (20<ø) KÝ HIỆU (ø) CÓ RA=2600KG/CM2 –CHIỀU DÀI THÉP NEO TẠI CÁC VỊ TRÍ LẤY BẰNG 30D	–CẮT NỐI UỐN CỐT THÉP THEO TCXDVN 5574–2018. –KHI THI CÔNG CẦN KẾT HỢP BẢN VẼ KIẾN TRÚC

CÔNG TY TNHH DESIGN AND CONSTRUCTION NEW MAXHOME
HÀ NỘI
ĐC : TẦNG 25, TÒA NHÀ VP TTTM CHỢ MƠ
SỐ 459C PHỐ BẠCH MAI, P. BẠCH MAI
THÀNH PHỐ HÀ NỘI
TEL: 0964458888 - 0828133333

Chủ đầu tư:

NGUYỄN THỊ ÁNH NGUYỆT

Địa điểm:

NAM HỒNG - HÀ TĨNH

Tên công trình:

NHÀ Ở GIA ĐÌNH

HỢP ĐỒNG SỐ /HĐ-TK/20.....

CHỦ NHIỆM THIẾT KẾ KTS: NGUYỄN VĂN CƯỜNG	
TRIỂN KHAI KS: HÀNG A LAO	
KIỂM DUYỆT KTS: NGUYỄN TẤT HỘI	

NỘI DUNG ĐIỀU CHỈNH

Lần	Ngày	Duyệt
1	.....	.....
2	.....	.....
3	.....	.....
4	.....	.....
5	.....	.....
6	.....	.....
7	.....	.....

Hạng mục:

KẾT CẤU


Tên bản vẽ:

GHI CHÚ CHUNG

	Hà Nội, 12-2025
Phát hành lần 01	Thiết kế
.....	**KC-00**

GHI CHÚ CHUNG

9. BỐ TRÍ LANH TÔ CỬA

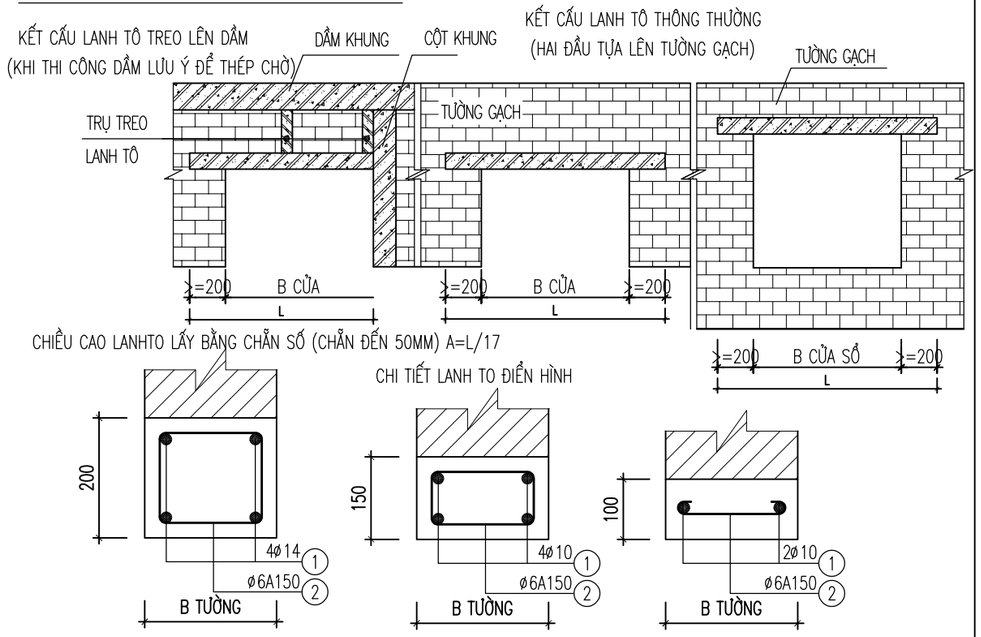

10. BẢO DƯỠNG BÊ TÔNG

THAM KHẢO THÊM TIÊU CHUẨN TCVN 8828:2011 – "BÊ TÔNG – YÊU CẦU BẢO DƯỠNG ẨM TỰ NHIÊN"

(1). BẢO DƯỠNG BÊ TÔNG MÓNG

- ĐỐI VỚI BÊ TÔNG MÓNG VÀ CÁC PHẦN NGẦM, CẦN ĐƯỢC TƯỚI NƯỚC THƯỜNG XUYÊN CHO ĐẾN KHI LẤP ĐẤT.
- CHỈ CẦN BÊ TÔNG ĐẠT ĐỘ TINH KẾT NHẤT ĐỊNH SAU 1–2 NGÀY CÓ THỂ THÁO COPPHA.
- SAU KHI LẤP ĐẤT CẦN MỘT LƯỢNG NƯỚC VỪA ĐỦ ĐỂ BẢO DƯỠNG TIẾP. TRONG MÙA HÈ NẮNG GẮT CÓ THỂ NGÂM NƯỚC.

(2). BẢO DƯỠNG BÊ TÔNG CỘT

- COPHA CỘT CÓ THỂ ĐƯỢC THÁO DỠ SAU 1–2 NGÀY, TÙY THUỘC VÀO ĐIỀU KIỆN THỜI TIẾT.
- NÊN DÙNG VẬT LIỆU CHE CHẮN ĐỂ HẠN CHẾ TỐI ĐA SỰ THOÁT NƯỚC CỦA BÊ TÔNG CỘT TIẾP XÚC VỚI MÔI TRƯỜNG.
- PHẢI ĐƯỢC TƯỚI NƯỚC THƯỜNG XUYÊN 3H/LẦN TRONG QUÁ TRÌNH BẢO DƯỠNG.

(2). BẢO DƯỠNG BÊ TÔNG DẦM, SÀN

(2.1). GIAI ĐOẠN ĐẦU

- CẦN PHỦ NGAY BỀ MẶT HỞ BẰNG CÁC VẬT LIỆU ĐÃ ĐƯỢC LÀM ẨM (NILON, BAO BỐ HAY CHẤT TẠO MÀNG NGĂN NƯỚC BỐC HƠI).

(2.1). GIAI ĐOẠN TIẾP THEO

- TRONG ĐIỀU KIỆN BÌNH THƯỜNG, NGAY SAU KHI ĐỔ BT 4 GIỜ NẾU TRỜI NẮNG PHẢI CHE PHỦ BỀ MẶT ĐỂ TRÁNH "TRẮNG BỀ MẶT".
- NHIỆT ĐỘ 15oC TRỞ LRRN THÌ 7 NGÀY ĐẦU PHẢI TƯỚI NƯỚC THƯỜNG XUYÊN ĐỂ GIỮ ẨM (CÓ THỂ NGÂM NƯỚC). KHOẢNG 3 GIỜ TƯỚI 1 LẦN, BAN ĐÊM ÍT NHẤT 2 LẦN. NHỮNG NGÀY SAU MỖI NGÀY TƯỚI 3 LẦN.
- TỪ 14–18 NGÀY PHẢI TƯỚI ÍT NHẤT 3 LẦN MỖI NGÀY ĐÊM.
- TRONG 2 NGÀY ĐẦU KHÔNG ĐỂ MƯA RƠI TRỰC TIẾP LÀM RỖ BỀ MẶT. TRONG 3 NGÀY ĐẦU, KHÔNG ĐƯỢC ĐI LẠI HAY TẬP KẾT VẬT LIỆU LÊN SÀN BÊ TÔNG MỚI ĐỔ.

(2.3). THÁO DỠ COPPA DẦM SÀN


- CHỈ ĐƯỢC THÁO COPPHA KHI CẤU KIỆN BÊ TÔNG ĐÃ ĐẠT ĐỦ SỨC BỀN VẬT LIỆU ĐỂ ỔN ĐỊNH KẾT CẤU.
- SAU 10–14 NGÀY CÓ THỂ THÁO DỠ ĐIỂM, KHÔNG NÊN THÁO DỠ TOÀN BỘ. NÊN TIẾP TỤC CHỐNG ĐỠ CÁC CẤU KIỆN SÀN, DẦM.
- SAU 3–4 TUẦN CÓ THỂ THÁO TOÀN BỘ COPPA DẦM SÀN. NẾU CÓ ĐIỀU KIỆN ĐỂ CÀNG LÂU CÀNG TỐT.

'CHỈ DẪN BẢO DƯỠNG SỬ DỤNG CHO BÊ TÔNG R28'

11. LỚP BẢO VỆ THÉP TRONG BÊ TÔNG - CON KÊ BÊ TÔNG


1. MÓNG

– LỚP BÊ TÔNG BẢO VỆ THÉP DÀY:
A = 50 MM
B = 100 MM ĐỐI VỚI CỌC ÉP VÀ ĐÓNG
B' = 50 MM
ø LÀ ĐƯỜNG KÍNH CỐT THÉP

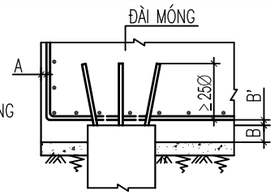

5. SÀN

– LỚP BÊ TÔNG BẢO VỆ CỐT THÉP DÀY:
A =15 MM KHI H>=10 CM
A =10 MM KHI H<10 CM
D LÀ ĐƯỜNG KÍNH THÉP CHỊU LỰC LỚP NHẤT
H LÀ CHIỀU DÀY SÀN

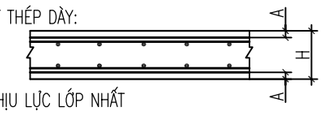


2. DẦM MÓNG VÀ DẦM SÀN TẦNG HẦM

– LỚP BÊ TÔNG BẢO VỆ CỐT THÉP DÀY:
A = 30 MM

3. CỘT VÀ VÁCH

– LỚP BÊ TÔNG BẢO VỆ CỐT THÉP CHỊU LỰC:
A >=25 MM VÀ A >= D
D LÀ ĐƯỜNG KÍNH THÉP CHỊU LỰC LỚP NHẤT

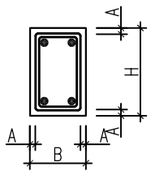

4. DẦM

– LỚP BÊ TÔNG BẢO VỆ CỐT THÉP CHỊU LỰC:
A >= 25 MM VÀ A >= D
D LÀ ĐƯỜNG KÍNH THÉP CHỊU LỰC LỚP NHẤT

12. DANH MỤC VẬT LIỆU SỬ DỤNG CHO CÔNG TRÌNH

5.1 BÊ TÔNG

– CÁC CHỈ ĐỊNH VỀ ĐẶC TRƯNG CỦA BÊ TÔNG TRONG MỤC NÀY CĂN CỨ THEO ĐIỀU 5. MỤC 5.1 TCVN 5574 – 2018

BẢNG 1. CHỈ TIÊU KỸ THUẬT CỦA BÊ TÔNG

CẤU KIỆN \ VẬT LIỆU	BÊ TÔNG			
	MÁC	ĐỘ SỤT (CM)	RB (KG/CM2)	RBT (KG/CM2)
– CỌC BÊ TÔNG	250	5–>10	115	9.0
– BÊ TÔNG LÓT	100	–	45	4.8
– MÓNG	250	–	115	9.0
– CỘT VÀ VÁCH	250	–	115	9.0
– DẦM VÀ SÀN	250	–	115	9.0
– BỂ NƯỚC NGẦM – VÁCH HẦM	250	–	115	9.0
– CẦU THANG BỘ	250	–	115	9.0
– LANH TÔ	250	5–>10	115	9.0

TRONG ĐÓ:
– RB: CƯỜNG ĐỘ TÍNH TOÁN NÉN DỌC TRỤC
– RBT: CƯỜNG ĐỘ TÍNH TOÁN KÉO DỌC TRỤC

BẢNG 2. KÍCH THƯỚC , CƯỜNG ĐỘ , KHỐI LƯỢNG VÀ DUNG SAI CỦA VẬT LIỆU THÉP SỬ DỤNG

ĐƯỜNG KÍNH DANH NGHĨA (MM)	DIỆN TÍCH MẶT CẮT NGANG (CM2)	LOẠI THÉP	TRỌNG LƯỢNG (KG/M DÀI)	RK (KG/CM2)	DUNG SAI (%)
6	0.283	CB240T	0.222	2100	± 8
8	0.503	CB240T	0.395	2100	± 8
10	0.785	CB300V	0.617	2600	± 5
12	1.131	CB300V	0.888	2600	± 5
14	1.540	CB300V	1.210	2600	± 5
16	2.010	CB300V	1.580	2600	± 5
18	2.545	CB400V	2.000	3500	± 5
20	3.140	CB400V	2.470	3500	± 5
22	3.800	CB400V	2.980	3500	± 4
25	4.900	CB400V	3.850	3500	± 4
28	6.155	CB400V	4.830	3500	± 4
30	7.065	CB400V	5.550	3500	± 4

CHỦ ĐẦU TƯ CẦN YÊU CẦU KỸ SƯ HIỆN TRƯỜNG KIỂM TRA - RÀ SOÁT BẢN VẼ TRƯỚC KHI THI CÔNG
NẾU CÓ THẮC MẮC VUI LÒNG LIÊN HỆ KIẾN TRÚC SƯ - KỸ SƯ THIẾT KẾ ĐỂ CÓ TƯ VẤN KỊP THỜI TRƯỚC KHI KHỞI CÔNG

HỖ TRỢ TƯ VẤN KỸ THUẬT XÂY DỰNG : 0924099999
LIÊN HỆ MUA VẬT LIỆU MAXHOME : 0921845555 (MIỄN PHÍ VẬN CHUYỂN TOÀN QUỐC)

–BÊ TÔNG LÓT MÓNG ĐÁ 4X6, MÁC 100 –BÊ TÔNG MÓNG, MÁC 250	–BÊ TÔNG CỘT, DẦM, SÀN MÁC 250 –LỚP BÊ TÔNG BẢO VỆ SÀN: 15MM	–LỚP BÊ TÔNG BẢO VỆ CỐT THÉP DẦM: 25MM –LỚP BÊ TÔNG BẢO VỆ CỐT THÉP CỘT: 25MM	–THÉP CB240T (ø<10) KÝ HIỆU (ø) CÓ RA=2100KG/CM2 –THÉP CB300V (10=<ø<=20) KÝ HIỆU (ø) CÓ RA=2600KG/CM2	–THÉP CB300V (20<ø) KÝ HIỆU (ø) CÓ RA=2600KG/CM2 –CHIỀU DÀI THÉP NEO TẠI CÁC VỊ TRÍ LẤY BẰNG 30D	–CẮT NỐI UỐN CỐT THÉP THEO TCXDVN 5574–2018. –KHI THI CÔNG CẦN KẾT HỢP BẢN VẼ KIẾN TRÚC

CÔNG TY TNHH DESIGN AND CONSTRUCTION NEW MAXHOME
HÀ NỘI
ĐC : TẦNG 25, TÒA NHÀ VP TTTM CHỢ MƠ
SỐ 459C PHỐ BẠCH MAI, P. BẠCH MAI
THÀNH PHỐ HÀ NỘI
TEL: 0964458888 - 0828133333

MAXHOME

Chủ đầu tư:
NGUYỄN THỊ ÁNH NGUYỆT

Địa điểm:
NAM HỒNG - HÀ TĨNH

Tên công trình:
NHÀ Ở GIA ĐÌNH

HỢP ĐỒNG SỐ /HĐ-TK/20.....

CHỦ NHIỆM THIẾT KẾ	
KTS: NGUYỄN VĂN CƯỜNG	
TRIỂN KHAI	
KS: HÀNG A LAO	
KIỂM DUYỆT	
KTS: NGUYỄN TẤT HỘI	


NỘI DUNG ĐIỀU CHỈNH

Lần	Ngày	Duyệt
1	.....	.....
2	.....	.....
3	.....	.....
4	.....	.....
5	.....	.....
6	.....	.....
7	.....	.....

Hạng mục:
KẾT CẤU

Tên bản vẽ:
GHI CHÚ CHUNG

	Hà Nội, 12-2025
Phát hành lần 01	Thiết kế
.....	**KC-00**

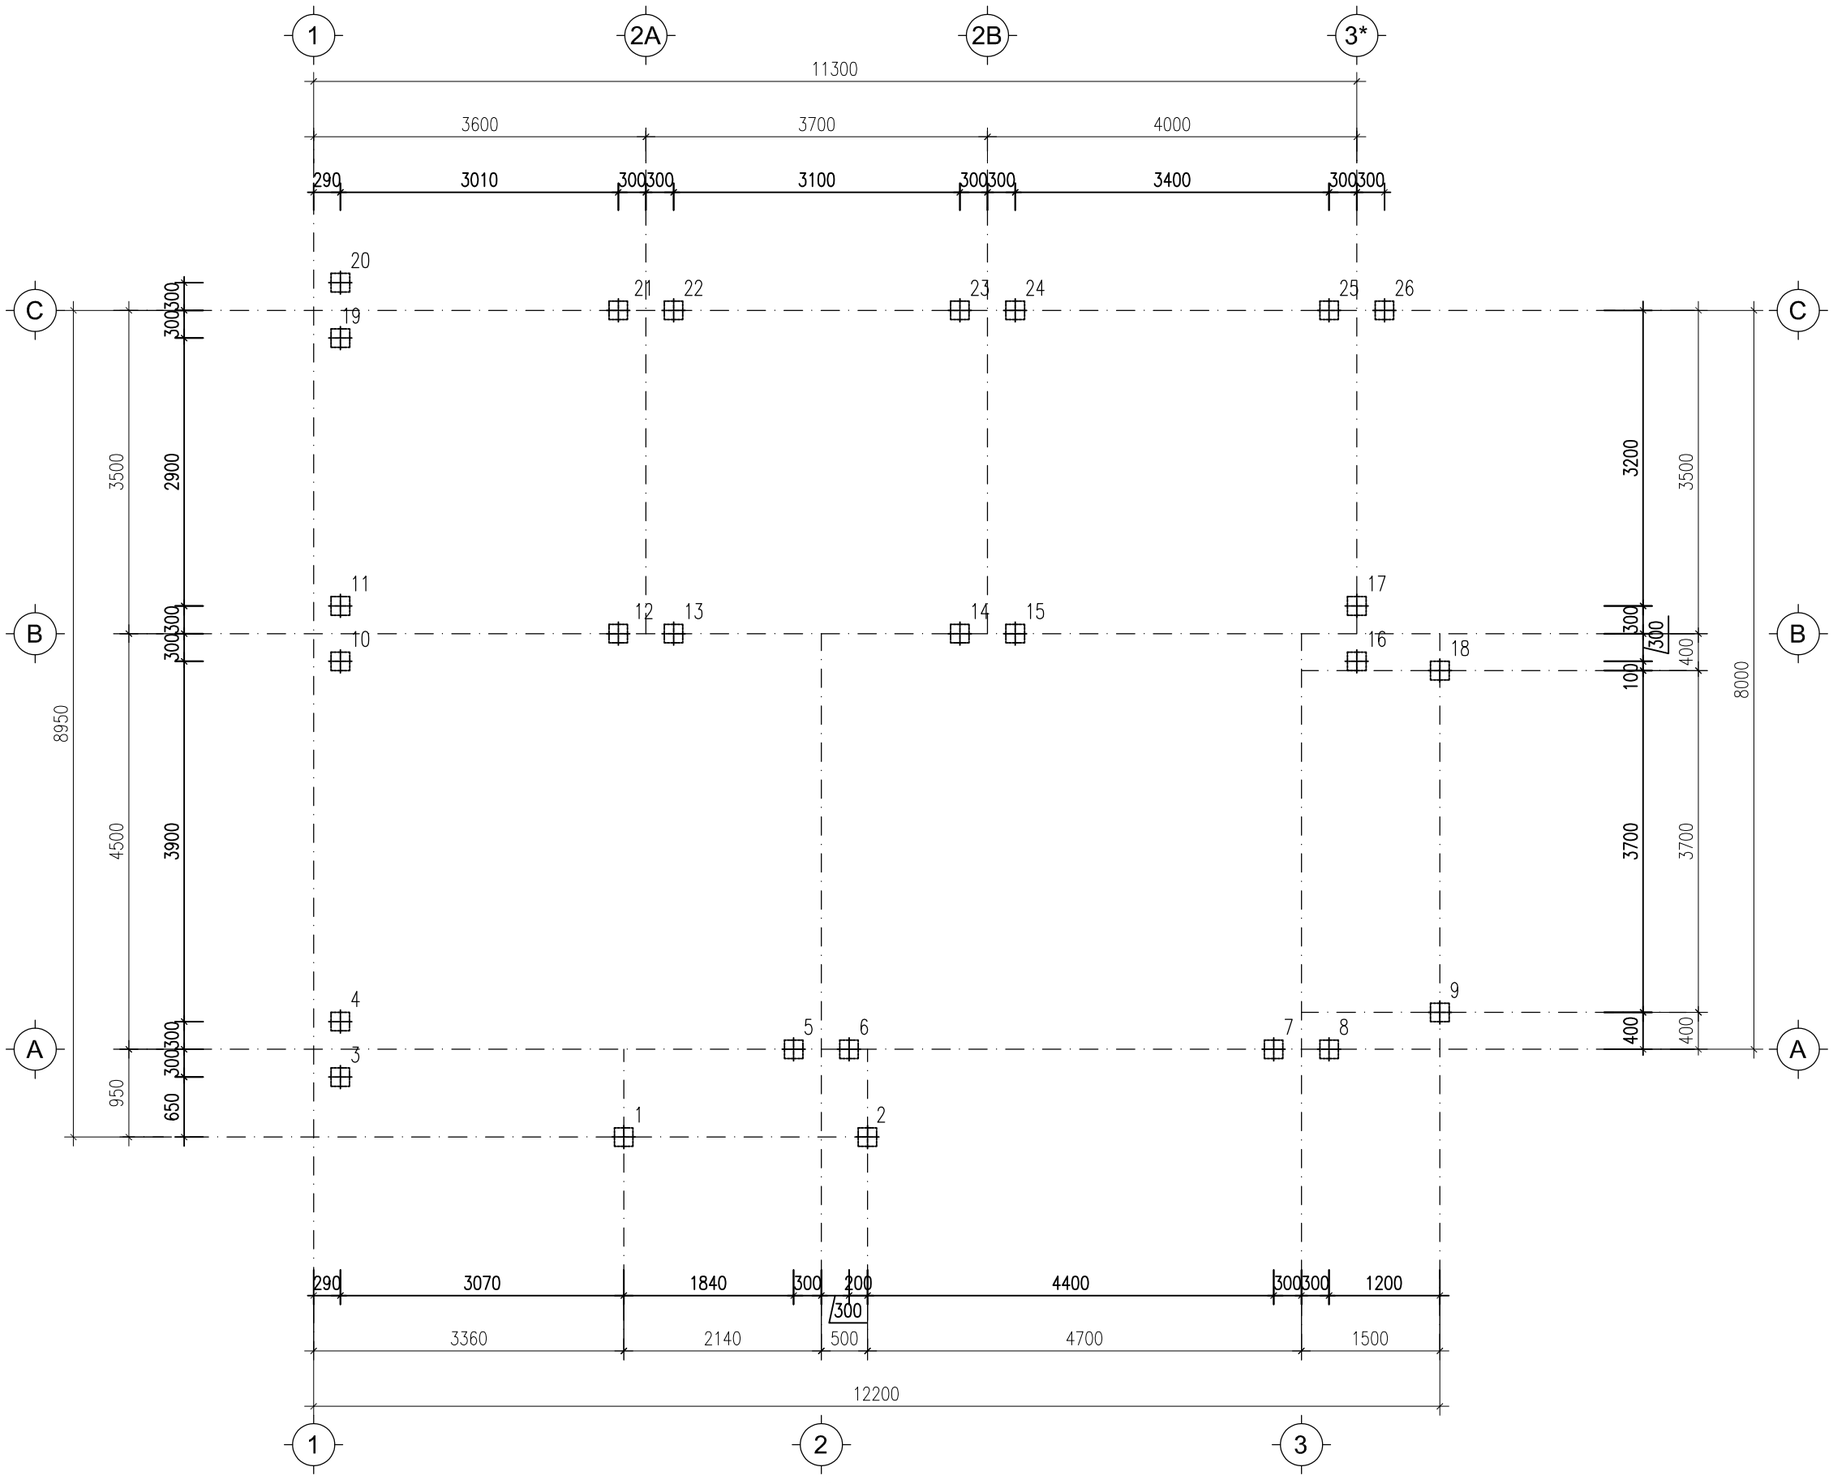

MẶT BẰNG ĐỊNH VỊ CỌC

CHỦ ĐẦU TƯ CẦN YÊU CẦU KỸ SƯ HIỆN TRƯỜNG KIỂM TRA - RÀ SOÁT BẢN VẼ TRƯỚC KHI THI CÔNG
NẾU CÓ THẮC MẮC VUI LÒNG LIÊN HỆ KIẾN TRÚC SƯ - KỸ SƯ THIẾT KẾ ĐỂ CÓ TƯ VẤN KỊP THỜI TRƯỚC KHI KHỞI CÔNG

HỖ TRỢ TƯ VẤN KỸ THUẬT XÂY DỰNG : 0924099999
LIÊN HỆ MUA VẬT LIỆU MAXHOME : 0921845555 (MIỄN PHÍ VẬN CHUYỂN TOÀN QUỐC)

-BÊ TÔNG LÓT MÓNG ĐÁ 4X6, MÁC 100 -BÊ TÔNG MÓNG, MÁC 250	-BÊ TÔNG CỘT, DẦM, SÀN MÁC 250 -LỚP BÊ TÔNG BẢO VỆ SÀN: 15MM	-LỚP BÊ TÔNG BẢO VỆ CỐT THÉP DẦM: 25MM -LỚP BÊ TÔNG BẢO VỆ CỐT THÉP CỘT: 25MM	-THÉP CB240T (ø<10) KÝ HIỆU (ø) CÓ RA=2100KG/CM2 -THÉP CB300V (10=<ø<=20) KÝ HIỆU (ø) CÓ RA=2600KG/CM2	-THÉP CB300V (20<ø) KÝ HIỆU (ø) CÓ RA=2600KG/CM2 -CHIỀU DÀI THÉP NEO TẠI CÁC VỊ TRÍ LẤY BẰNG 30D	-CẮT NỐI UỐN CỐT THÉP THEO TCXDVN 5574-2018. -KHI THI CÔNG CẦN KẾT HỢP BẢN VẼ KIẾN TRÚC

CÔNG TY TNHH DESIGN AND CONSTRUCTION NEW MAXHOME
HÀ NỘI
ĐC : TẦNG 25, TÒA NHÀ VP TTTM CHỢ MƠ
SỐ 459C PHỐ BẠCH MAI, P. BẠCH MAI
THÀNH PHỐ HÀ NỘI
TEL: 0964458888 - 0828133333

Chủ đầu tư:

NGUYỄN THỊ ÁNH NGUYỆT

Địa điểm:

NAM HỒNG - HÀ TĨNH

Tên công trình:

NHÀ Ở GIA ĐÌNH

HỢP ĐỒNG SỐ /HĐ-TK/20.....

CHỦ NHIỆM THIẾT KẾ KTS: NGUYỄN VĂN CƯỜNG	
TRIỂN KHAI KS: HÀNG A LAO	
KIỂM DUYỆT KTS: NGUYỄN TẤT HỘI	

NỘI DUNG ĐIỀU CHỈNH

Lần	Ngày	Duyệt
1	.....	.....
2	.....	.....
3	.....	.....
4	.....	.....
5	.....	.....
6	.....	.....
7	.....	.....


Hạng mục:

KẾT CẤU


Tên bản vẽ:

MBDV CỌC


	Hà Nội, 12-2025
Phát hành lần 01	Thiết kế
.....	**KC-01-01**

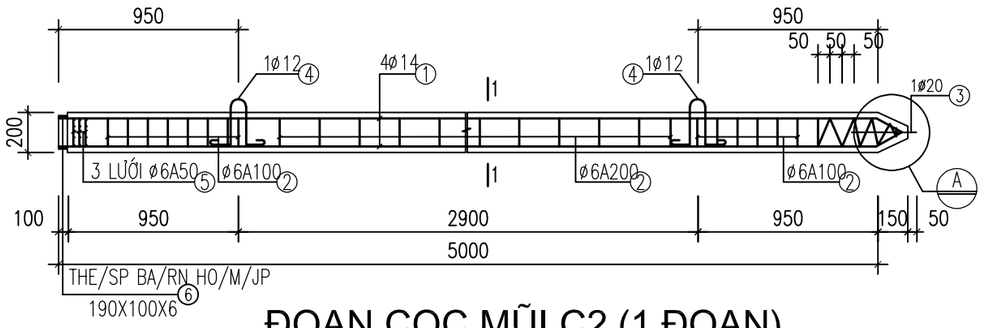


ĐOẠN CỌC MŨI C2 (1 ĐOẠN)

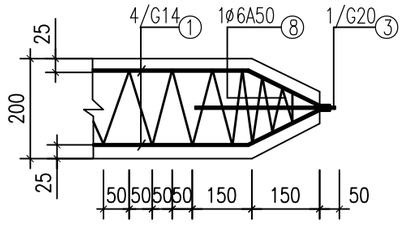


CHI TIẾT A

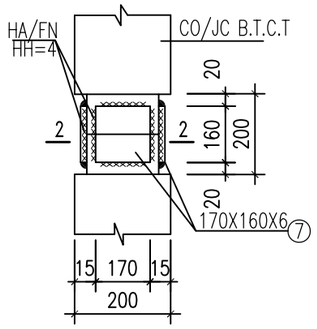


CHI TIẾT NỐI CỌC

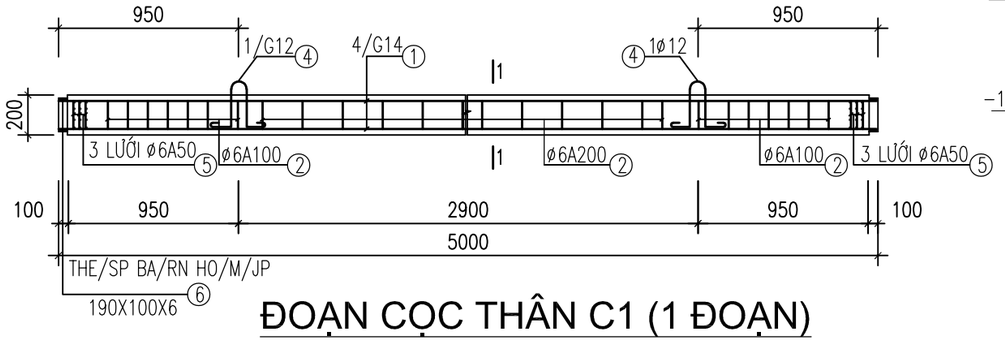


ĐOẠN CỌC THÂN C1 (1 ĐOẠN)

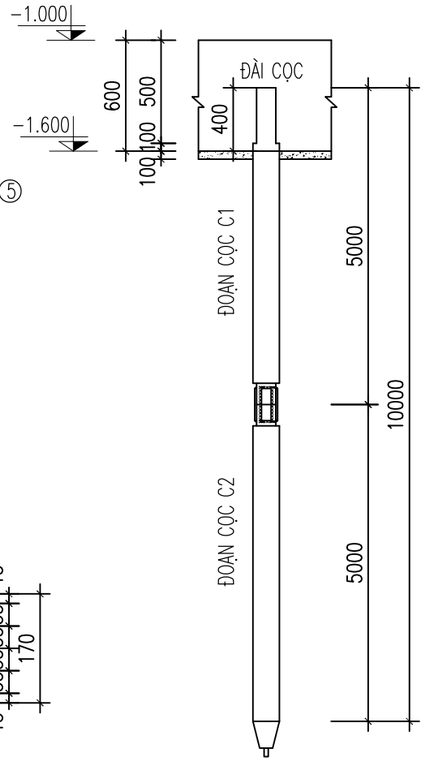


SƠ ĐỒ CỌC

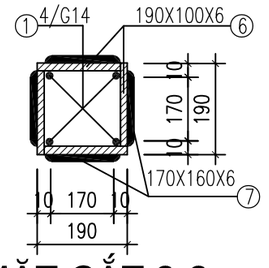


MẶT CẮT 2-2

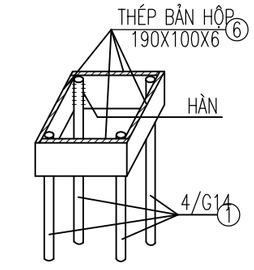

CHI TIẾT HÀN THÉP BẢN ĐẦU CỌC

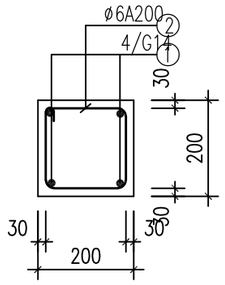

MẶT CẮT 1-1

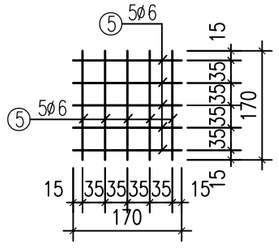

LƯỚI S1

GHI CHÚ:

- BÊ TÔNG CỌC MÁC 250# BẢO DƯỠNG ĐÚNG QUY PHẠM KỸ THUẬT
- KHI ĐẠT CƯỜNG ĐỘ 100% MỚI ĐƯỢC VẬN CHUYỂN THI CÔNG
- THÉP AI (ø<10) CÓ RA=2250 KG/CM2
- THÉP AII ('>=10) CÓ RA=2800 KG/CM2
- THÉP TẤM, THÉP GÓC LOẠI CT3 CÓ R=2100 KG/CM2
- QUE HÀN E42 HAY TƯƠNG ĐƯƠNG
- SỬ DỤNG CỌC BÊ TÔNG CỐT THÉP TIẾT DIỆN 200X200MM
- SỨC CHỊU TẢI THIẾT KẾ CỦA CỌC [P]=15T
- LỰC ÉP NHỎ NHẤT = 30 TẤN VÀ LỚN NHẤT 40 TẤN
- KHI CÓ KẾT QUẢ ÉP THÍ NGHIỆM CỌC MỚI ĐƯỢC ÉP CỌC ĐẠI TRÀ
- CHIỀU DÀI CỌC CÓ THỂ THAY ĐỔI SAU KHI CÓ KẾT QUẢ ÉP THỬ CỌC
- KHI THI CÔNG ĐÀI CẦN ĐẬP VỠ ĐẦU CỌC 40CM (LÀM SẠCH ĐẦU CỌC VÀ THÉP) ĐỂ LIÊN KẾT CỌC VỚI ĐÀI
- KHI TRIỂN KHAI THI CÔNG, ĐƠN VỊ THI CÔNG VÀ TƯ VẤN GIÁM SÁT CẦN THEO DÕI QUÁ TRÌNH ÉP CỌC VÀ PHẢI CẤP SỐ LIỆU LỰC ÉP TRÊN MÁY CHO TƯ VẤN THIẾT KẾ BIẾT ĐỂ CÓ BIỆN PHÁP ĐIỀU CHỈNH MÓNG
- TỔNG SỐ LƯỢNG CỌC ÉP ĐẠI TRÀ LÀ 26 CỌC. MỖI CỌC TẠM TÍNH DÀI 10.0M GỒM 1 ĐOẠN THÂN DÀI 5.0M VÀ 1 ĐOẠN MŨI DÀI 5.0M

CHỦ ĐẦU TƯ CẦN YÊU CẦU KỸ SƯ HIỆN TRƯỜNG KIỂM TRA - RÀ SOÁT BẢN VẼ TRƯỚC KHI THI CÔNG
NẾU CÓ THẮC MẮC VUI LÒNG LIÊN HỆ KIẾN TRÚC SƯ - KỸ SƯ THIẾT KẾ ĐỂ CÓ TƯ VẤN KỊP THỜI TRƯỚC KHI KHỞI CÔNG

HỖ TRỢ TƯ VẤN KỸ THUẬT XÂY DỰNG : 0924099999
LIÊN HỆ MUA VẬT LIỆU MAXHOME : 0921845555 (MIỄN PHÍ VẬN CHUYỂN TOÀN QUỐC)

-BÊ TÔNG LÓT MÓNG ĐÁ 4X6, MÁC 100 -BÊ TÔNG MÓNG, MÁC 250	-BÊ TÔNG CỘT, DẦM, SÀN MÁC 250 -LỚP BÊ TÔNG BẢO VỆ SÀN: 15MM	-LỚP BÊ TÔNG BẢO VỆ CỐT THÉP DẦM: 25MM -LỚP BÊ TÔNG BẢO VỆ CỐT THÉP CỘT: 25MM	-THÉP CB240T (ø<10) KÝ HIỆU (ø) CÓ RA=2100KG/CM2 -THÉP CB300V (10=<ø<=20) KÝ HIỆU (ø) CÓ RA=2600KG/CM2	-THÉP CB300V (20<ø) KÝ HIỆU (ø) CÓ RA=2600KG/CM2 -CHIỀU DÀI THÉP NEO TẠI CÁC VỊ TRÍ LẤY BẰNG 30D	-CẮT NỐI UỐN CỐT THÉP THEO TCXDVN 5574-2018. -KHI THI CÔNG CẦN KẾT HỢP BẢN VẼ KIẾN TRÚC

CÔNG TY TNHH DESIGN AND CONSTRUCTION NEW MAXHOME
HÀ NỘI
ĐC : TẦNG 25, TÒA NHÀ VP TTTM CHỢ MƠ
SỐ 459C PHỐ BẠCH MAI, P. BẠCH MAI
THÀNH PHỐ HÀ NỘI
TEL: 0964458888 - 0828133333

Chủ đầu tư:
NGUYỄN THỊ ÁNH NGUYỆT

Địa điểm:
NAM HỒNG - HÀ TĨNH

Tên công trình:
NHÀ Ở GIA ĐÌNH

HỢP ĐỒNG SỐ /HĐ-TK/20.....

CHỦ NHIỆM THIẾT KẾ KTS: NGUYỄN VĂN CƯỜNG	
TRIỂN KHAI KS: HÀNG A LAO	
KIỂM DUYỆT KTS: NGUYỄN TẤT HỘI	


NỘI DUNG ĐIỀU CHỈNH

Lần	Ngày	Duyệt
1	.....	.....
2	.....	.....
3	.....	.....
4	.....	.....
5	.....	.....
6	.....	.....
7	.....	.....

Hạng mục:
KẾT CẤU

Tên bản vẽ:
CHI TIẾT CỌC

	Hà Nội, 12-2025
Phát hành lần 01	Thiết kế
.....	**KC-01-02**

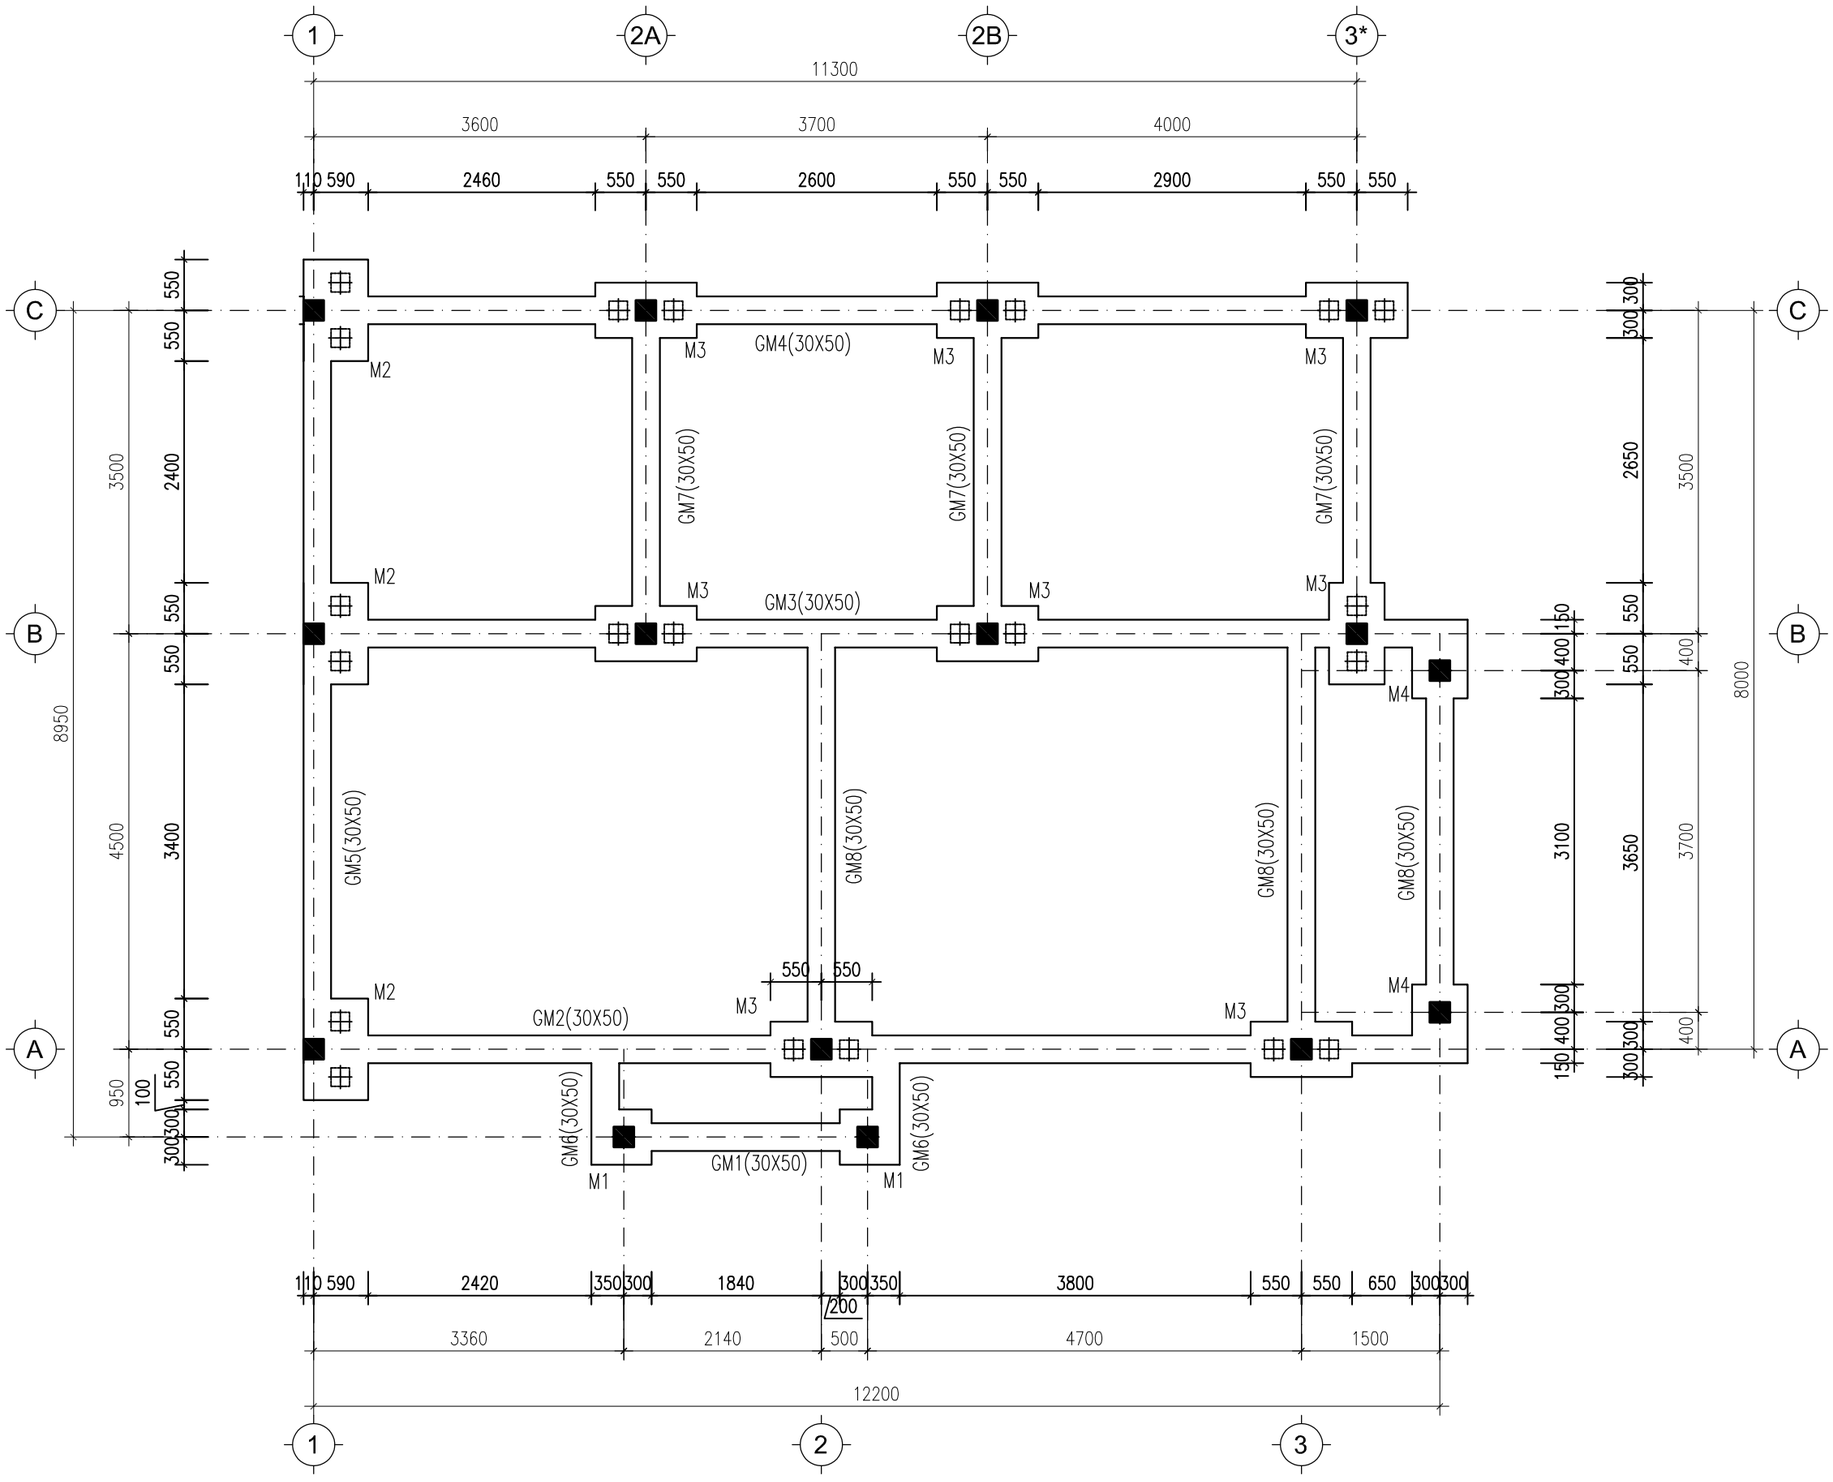

MẶT BẰNG MÓNG

CHỦ ĐẦU TƯ CẦN YÊU CẦU KỸ SƯ HIỆN TRƯỜNG KIỂM TRA - RÀ SOÁT BẢN VẼ TRƯỚC KHI THI CÔNG
NẾU CÓ THẮC MẮC VUI LÒNG LIÊN HỆ KIẾN TRÚC SƯ - KỸ SƯ THIẾT KẾ ĐỂ CÓ TƯ VẤN KỊP THỜI TRƯỚC KHI KHỞI CÔNG

HỖ TRỢ TƯ VẤN KỸ THUẬT XÂY DỰNG : 0924099999
LIÊN HỆ MUA VẬT LIỆU MAXHOME : 0921845555 (MIỄN PHÍ VẬN CHUYỂN TOÀN QUỐC)

-BÊ TÔNG LÓT MÓNG ĐÁ 4X6, MÁC 100 -BÊ TÔNG MÓNG, MÁC 250	-BÊ TÔNG CỘT, DẦM, SÀN MÁC 250 -LỚP BÊ TÔNG BẢO VỆ SÀN: 15MM	-LỚP BÊ TÔNG BẢO VỆ CỐT THÉP DẦM: 25MM -LỚP BÊ TÔNG BẢO VỆ CỐT THÉP CỘT: 25MM	-THÉP CB240T (ø<10) KÝ HIỆU (ø) CÓ RA=2100KG/CM2 -THÉP CB300V (10=<ø<=20) KÝ HIỆU (ø) CÓ RA=2600KG/CM2	-THÉP CB300V (20<ø) KÝ HIỆU (ø) CÓ RA=2600KG/CM2 -CHIỀU DÀI THÉP NEO TẠI CÁC VỊ TRÍ LẤY BẰNG 30D	-CẮT NỐI UỐN CỐT THÉP THEO TCXDVN 5574-2018. -KHI THI CÔNG CẦN KẾT HỢP BẢN VẼ KIẾN TRÚC

CÔNG TY TNHH DESIGN AND CONSTRUCTION NEW MAXHOME
HÀ NỘI
ĐC : TẦNG 25, TÒA NHÀ VP TTTM CHỢ MƠ
SỐ 459C PHỐ BẠCH MAI, P. BẠCH MAI
THÀNH PHỐ HÀ NỘI
TEL: 0964458888 - 0828133333

MAXHOME

Chủ đầu tư:

NGUYỄN THỊ ÁNH NGUYỆT

Địa điểm:

NAM HỒNG - HÀ TĨNH

Tên công trình:

NHÀ Ở GIA ĐÌNH

HỢP ĐỒNG SỐ /HĐ-TK/20.....

CHỦ NHIỆM THIẾT KẾ KTS: NGUYỄN VĂN CƯỜNG	
TRIỂN KHAI KS: HÀNG A LAO	
KIỂM DUYỆT KTS: NGUYỄN TẤT HỘI	

NỘI DUNG ĐIỀU CHỈNH

Lần	Ngày	Duyệt
1	.....	.....
2	.....	.....
3	.....	.....
4	.....	.....
5	.....	.....
6	.....	.....
7	.....	.....


Hạng mục:

KẾT CẤU

Tên bản vẽ:

MB MÓNG

	Hà Nội, 12-2025
Phát hành lần 01	Thiết kế
.....	**KC-01-03**

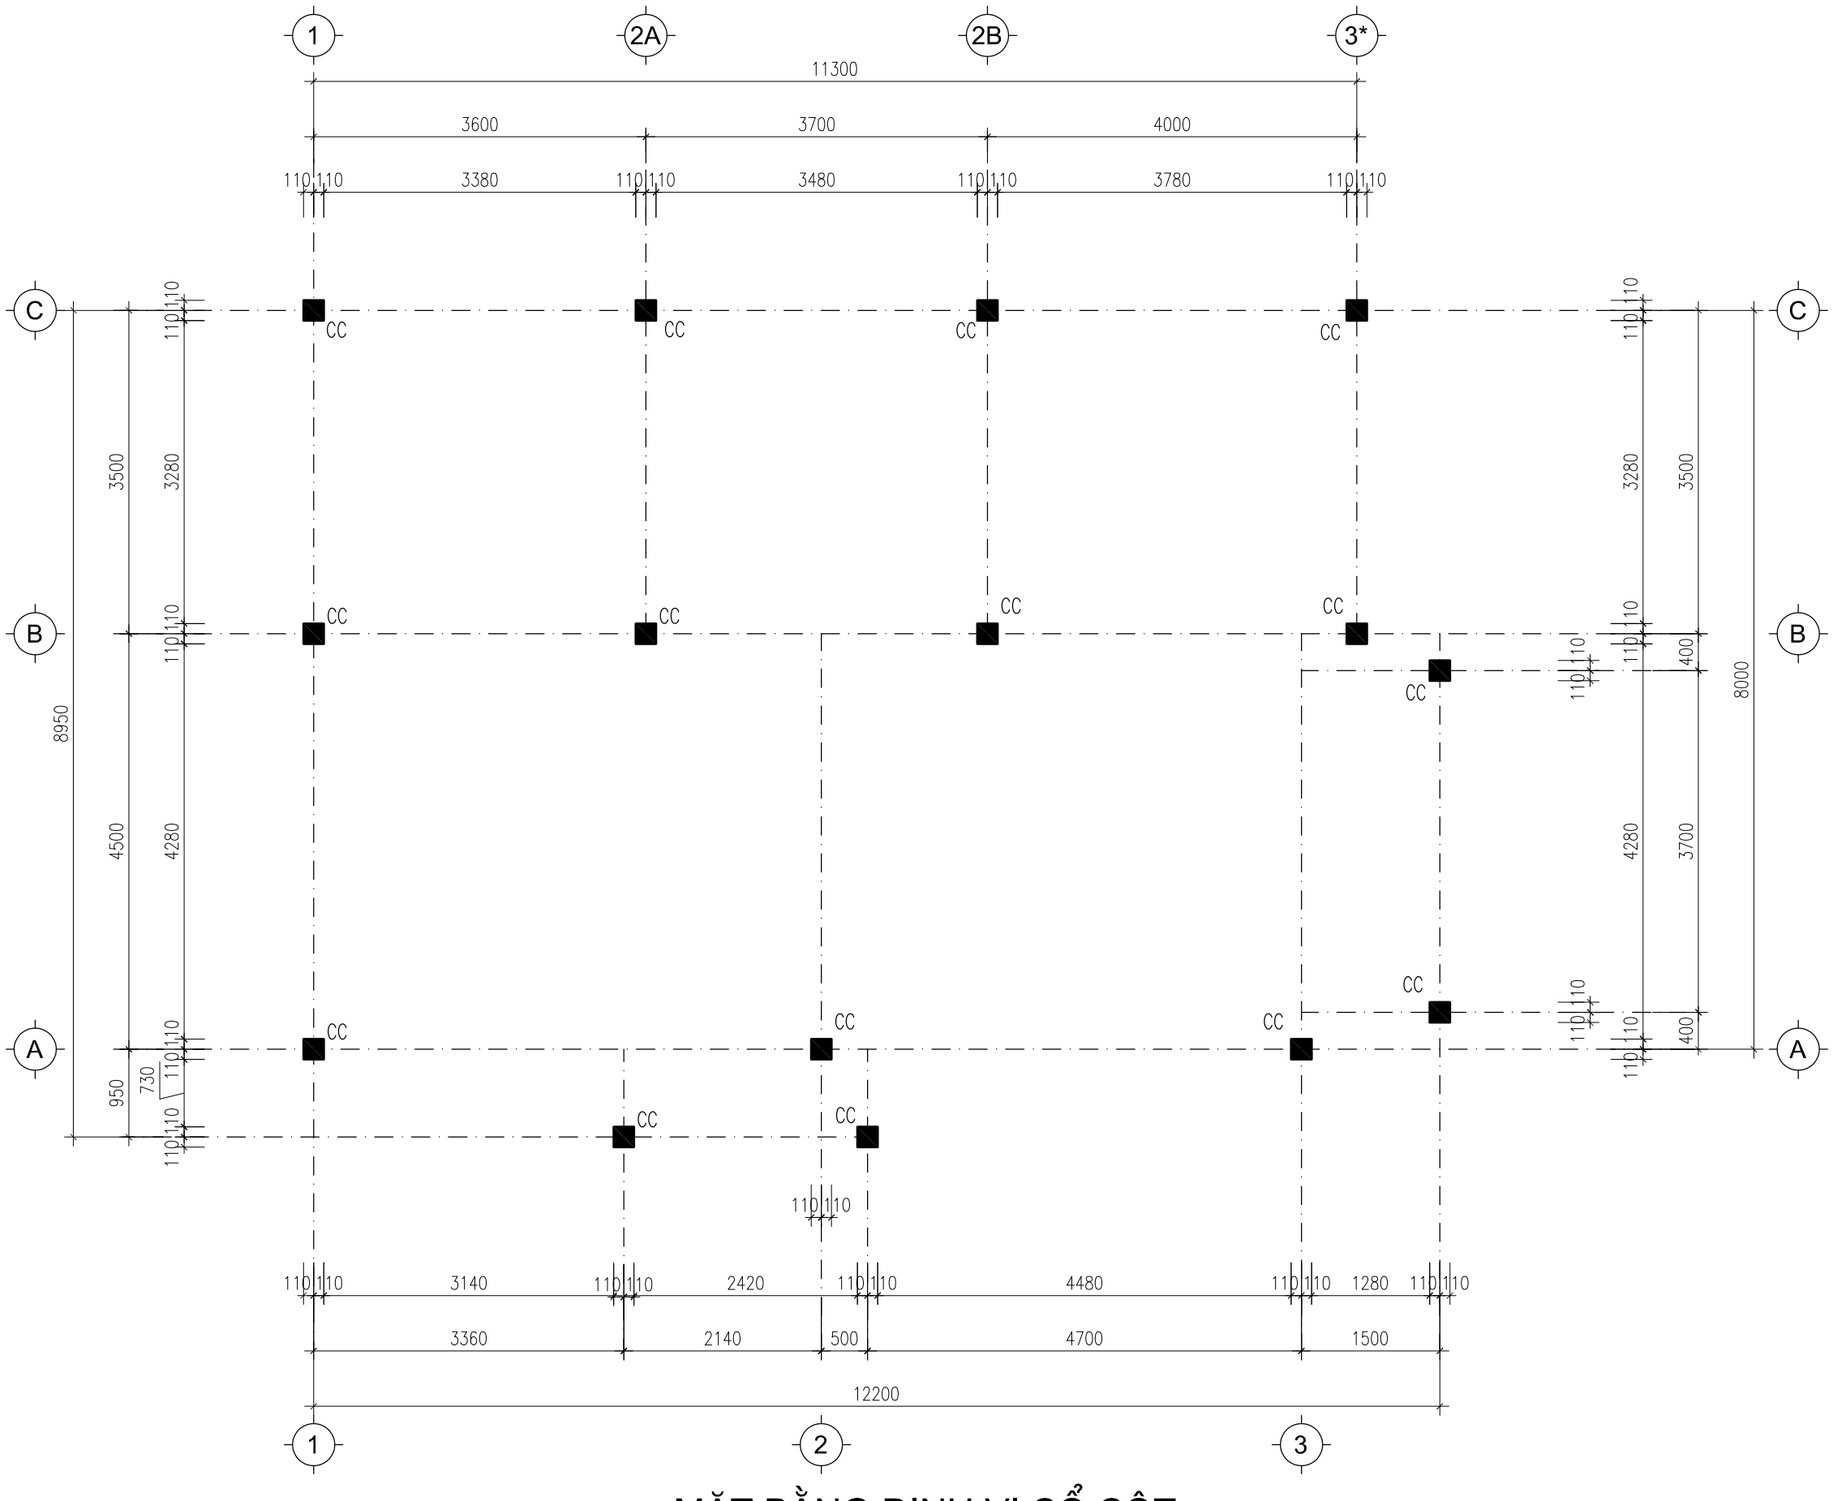

MẶT BẰNG ĐỊNH VỊ CỔ CỘT

CHỦ ĐẦU TƯ CẦN YÊU CẦU KỸ SƯ HIỆN TRƯỜNG KIỂM TRA - RÀ SOÁT BẢN VẼ TRƯỚC KHI THI CÔNG
NẾU CÓ THẮC MẮC VUI LÒNG LIÊN HỆ KIẾN TRÚC SƯ - KỸ SƯ THIẾT KẾ ĐỂ CÓ TƯ VẤN KỊP THỜI TRƯỚC KHI KHỞI CÔNG

HỖ TRỢ TƯ VẤN KỸ THUẬT XÂY DỰNG : 0924099999
LIÊN HỆ MUA VẬT LIỆU MAXHOME : 0921845555 (MIỄN PHÍ VẬN CHUYỂN TOÀN QUỐC)

-BÊ TÔNG LÓT MÓNG ĐÁ 4X6, MÁC 100 -BÊ TÔNG MÓNG, MÁC 250	-BÊ TÔNG CỘT, DẦM, SÀN MÁC 250 -LỚP BÊ TÔNG BẢO VỆ SÀN: 15MM	-LỚP BÊ TÔNG BẢO VỆ CỐT THÉP DẦM: 25MM -LỚP BÊ TÔNG BẢO VỆ CỐT THÉP CỘT: 25MM	-THÉP CB240T (ø<10) KÝ HIỆU (ø) CÓ RA=2100KG/CM2 -THÉP CB300V (10=<ø<=20) KÝ HIỆU (ø) CÓ RA=2600KG/CM2	-THÉP CB300V (20<ø) KÝ HIỆU (ø) CÓ RA=2600KG/CM2 -CHIỀU DÀI THÉP NEO TẠI CÁC VỊ TRÍ LẤY BẰNG 30D	-CẮT NỐI UỐN CỐT THÉP THEO TCXDVN 5574-2018. -KHI THI CÔNG CẦN KẾT HỢP BẢN VẼ KIẾN TRÚC

CÔNG TY TNHH DESIGN AND CONSTRUCTION NEW MAXHOME
HÀ NỘI
ĐC : TẦNG 25, TÒA NHÀ VP TTTM CHỢ MƠ
SỐ 459C PHỐ BẠCH MAI, P. BẠCH MAI
THÀNH PHỐ HÀ NỘI
TEL: 0964458888 - 0828133333

Chủ đầu tư:

NGUYỄN THỊ ÁNH NGUYỆT

Địa điểm:

NAM HỒNG - HÀ TĨNH

Tên công trình:

NHÀ Ở GIA ĐÌNH

HỢP ĐỒNG SỐ /HĐ-TK/20.....

CHỦ NHIỆM THIẾT KẾ KTS: NGUYỄN VĂN CƯỜNG	
TRIỂN KHAI KS: HÀNG A LAO	
KIỂM DUYỆT KTS: NGUYỄN TẤT HỘI	

NỘI DUNG ĐIỀU CHỈNH

Lần	Ngày	Duyệt
1	.....	.....
2	.....	.....
3	.....	.....
4	.....	.....
5	.....	.....
6	.....	.....
7	.....	.....


Hạng mục:

KẾT CẤU

Tên bản vẽ:

MBDV CỔ CỘT

	Hà Nội, 12-2025
Phát hành lần 01	Thiết kế
.....	**KC-01-04**

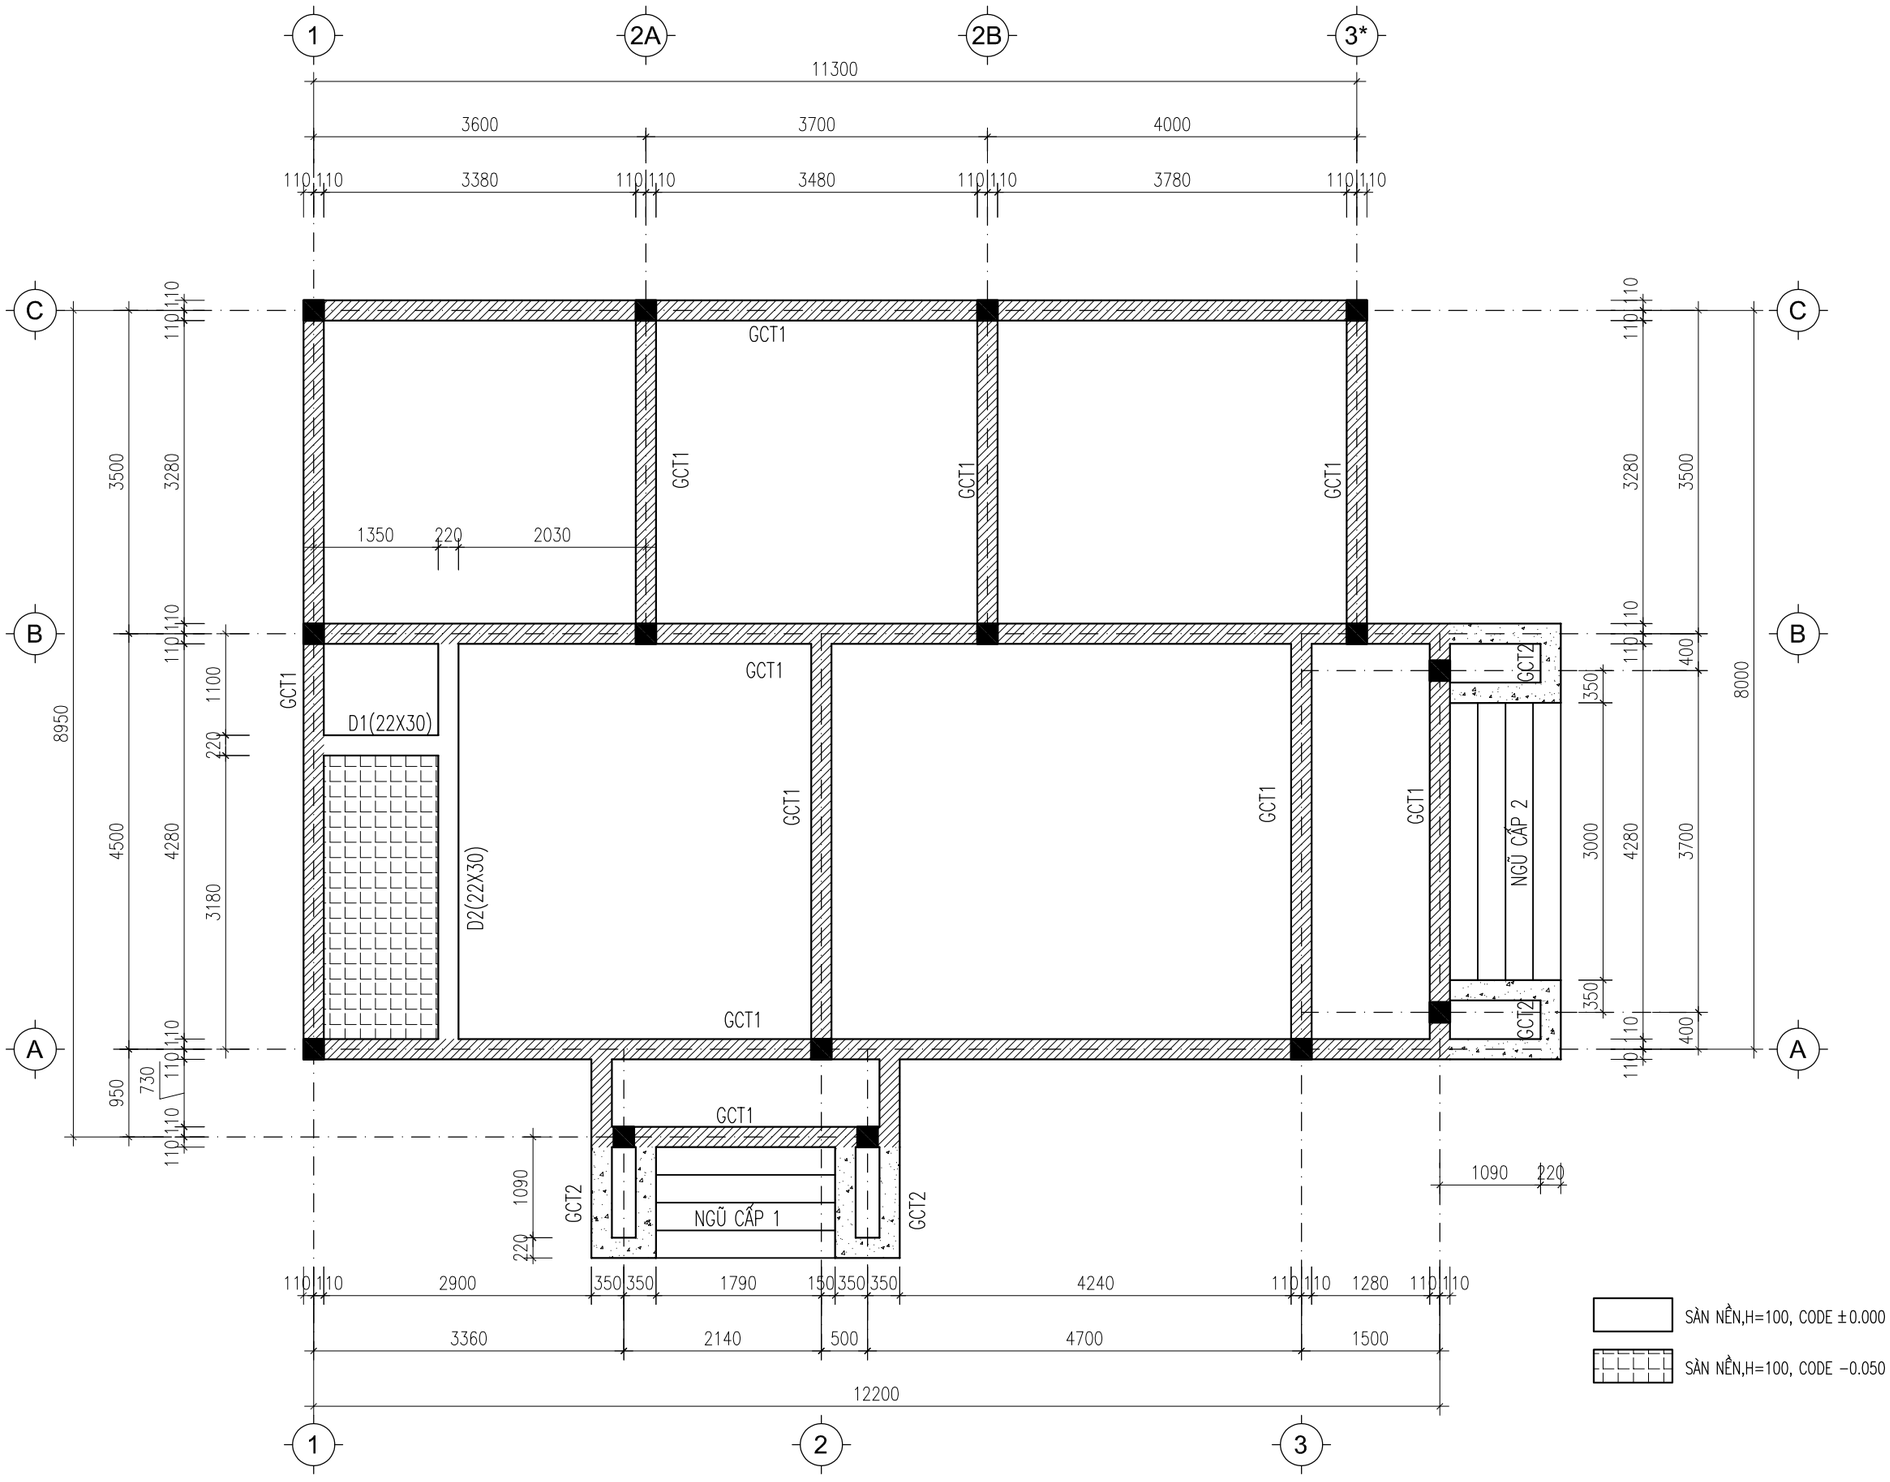

MẶT BẰNG GIẰNG CHÂN TƯỜNG

CHỦ ĐẦU TƯ CẦN YÊU CẦU KỸ SƯ HIỆN TRƯỜNG KIỂM TRA - RÀ SOÁT BẢN VẼ TRƯỚC KHI THI CÔNG
NẾU CÓ THẮC MẮC VUI LÒNG LIÊN HỆ KIẾN TRÚC SƯ - KỸ SƯ THIẾT KẾ ĐỂ CÓ TƯ VẤN KỊP THỜI TRƯỚC KHI KHỞI CÔNG

HỖ TRỢ TƯ VẤN KỸ THUẬT XÂY DỰNG : 0924099999
LIÊN HỆ MUA VẬT LIỆU MAXHOME : 0921845555 (MIỄN PHÍ VẬN CHUYỂN TOÀN QUỐC)

-BÊ TÔNG LÓT MÓNG ĐÁ 4X6, MÁC 100 -BÊ TÔNG MÓNG, MÁC 250	-BÊ TÔNG CỘT, DẦM, SÀN MÁC 250 -LỚP BÊ TÔNG BẢO VỆ SÀN: 15MM	-LỚP BÊ TÔNG BẢO VỆ CỐT THÉP DẦM: 25MM -LỚP BÊ TÔNG BẢO VỆ CỐT THÉP CỘT: 25MM	-THÉP CB240T (ø<10) KÝ HIỆU (ø) CÓ RA=2100KG/CM2 -THÉP CB300V (10=<ø<=20) KÝ HIỆU (ø) CÓ RA=2600KG/CM2	-THÉP CB300V (20<ø) KÝ HIỆU (ø) CÓ RA=2600KG/CM2 -CHIỀU DÀI THÉP NEO TẠI CÁC VỊ TRÍ LẤY BẰNG 30D	-CẮT NỐI UỐN CỐT THÉP THEO TCXDVN 5574-2018. -KHI THI CÔNG CẦN KẾT HỢP BẢN VẼ KIẾN TRÚC

CÔNG TY TNHH DESIGN AND CONSTRUCTION NEW MAXHOME
HÀ NỘI
ĐC : TẦNG 25, TÒA NHÀ VP TTTM CHỢ MƠ
SỐ 459C PHỐ BẠCH MAI, P. BẠCH MAI
THÀNH PHỐ HÀ NỘI
TEL: 0964458888 - 0828133333

Chủ đầu tư:

NGUYỄN THỊ ÁNH NGUYỆT

Địa điểm:

NAM HỒNG - HÀ TĨNH

Tên công trình:

NHÀ Ở GIA ĐÌNH

HỢP ĐỒNG SỐ /HĐ-TK/20.....

CHỦ NHIỆM THIẾT KẾ KTS: NGUYỄN VĂN CƯỜNG	
TRIỂN KHAI KS: HÀNG A LAO	
KIỂM DUYỆT KTS: NGUYỄN TẤT HỘI	

NỘI DUNG ĐIỀU CHỈNH

Lần	Ngày	Duyệt
1	.....	.....
2	.....	.....
3	.....	.....
4	.....	.....
5	.....	.....
6	.....	.....
7	.....	.....


Hạng mục:

KẾT CẤU

Tên bản vẽ:

MB GIẰNG CHÂN TƯỜNG

	Hà Nội, 12-2025
Phát hành lần 01	Thiết kế
.....	**KC-01-05**

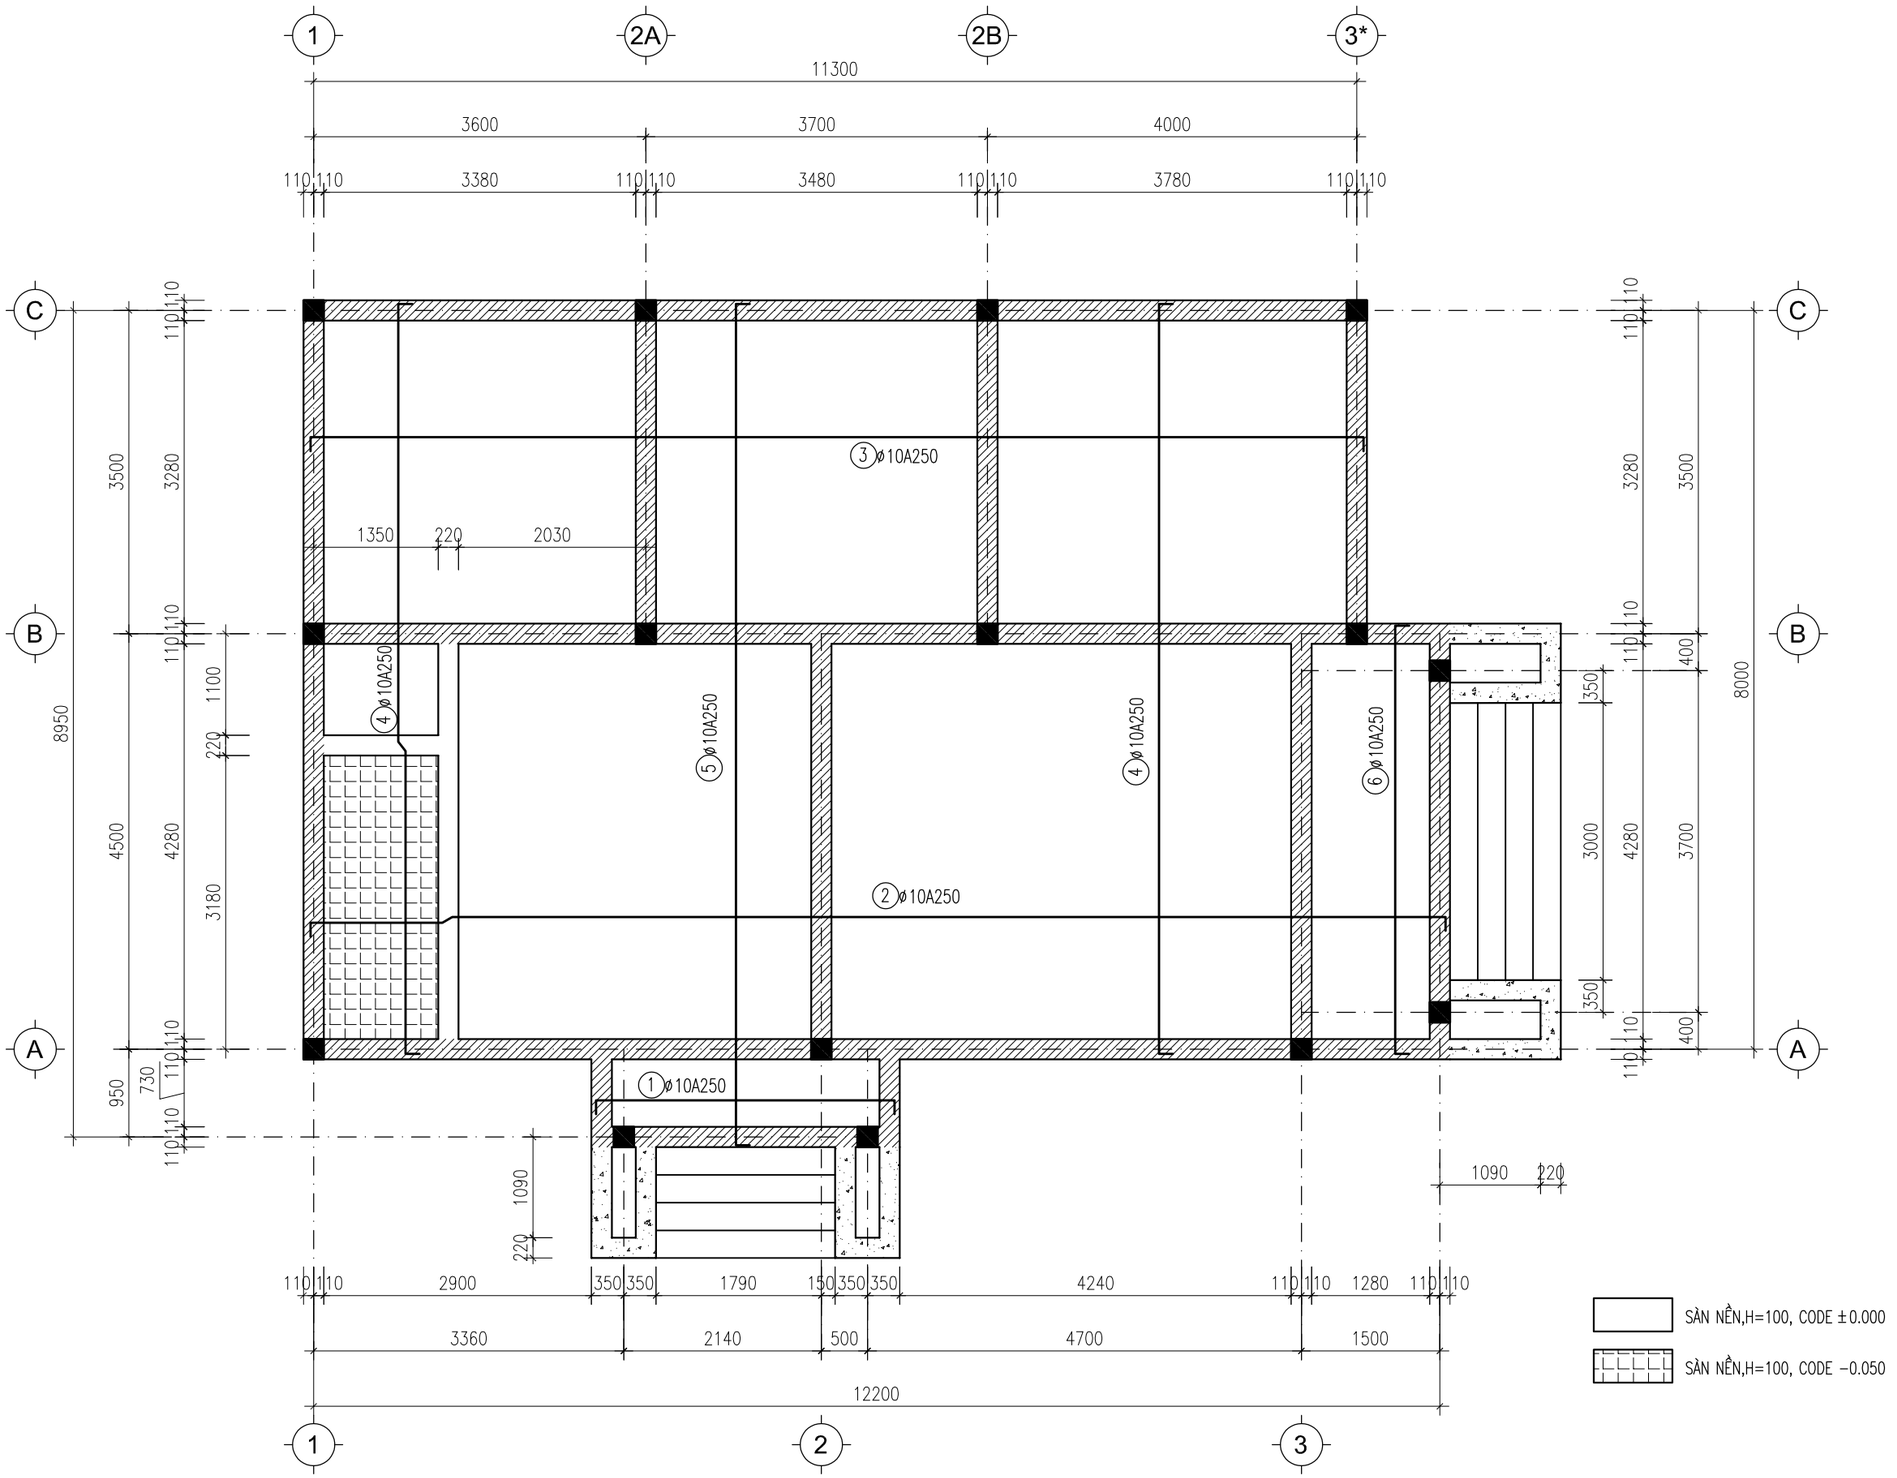

MẶT BẰNG THÉP SÀN NỀN TẦNG 1

CHỦ ĐẦU TƯ CẦN YÊU CẦU KỸ SƯ HIỆN TRƯỜNG KIỂM TRA - RÀ SOÁT BẢN VẼ TRƯỚC KHI THI CÔNG
NẾU CÓ THẮC MẮC VUI LÒNG LIÊN HỆ KIẾN TRÚC SƯ - KỸ SƯ THIẾT KẾ ĐỂ CÓ TƯ VẤN KỊP THỜI TRƯỚC KHI KHỞI CÔNG

HỖ TRỢ TƯ VẤN KỸ THUẬT XÂY DỰNG : 0924099999
LIÊN HỆ MUA VẬT LIỆU MAXHOME : 0921845555 (MIỄN PHÍ VẬN CHUYỂN TOÀN QUỐC)

-BÊ TÔNG LÓT MÓNG ĐÁ 4X6, MÁC 100 -BÊ TÔNG MÓNG, MÁC 250	-BÊ TÔNG CỘT, DẦM, SÀN MÁC 250 -LỚP BÊ TÔNG BẢO VỆ SÀN: 15MM	-LỚP BÊ TÔNG BẢO VỆ CỐT THÉP DẦM: 25MM -LỚP BÊ TÔNG BẢO VỆ CỐT THÉP CỘT: 25MM	-THÉP CB240T (ø<10) KÝ HIỆU (ø) CÓ RA=2100KG/CM2 -THÉP CB300V (10=<ø<=20) KÝ HIỆU (ø) CÓ RA=2600KG/CM2	-THÉP CB300V (20<ø) KÝ HIỆU (ø) CÓ RA=2600KG/CM2 -CHIỀU DÀI THÉP NEO TẠI CÁC VỊ TRÍ LẤY BẰNG 30D	-CẮT NỐI UỐN CỐT THÉP THEO TCXDVN 5574-2018. -KHI THI CÔNG CẦN KẾT HỢP BẢN VẼ KIẾN TRÚC

CÔNG TY TNHH DESIGN AND CONSTRUCTION NEW MAXHOME
HÀ NỘI
ĐC : TẦNG 25, TÒA NHÀ VP TTTM CHỢ MƠ
SỐ 459C PHỐ BẠCH MAI, P. BẠCH MAI
THÀNH PHỐ HÀ NỘI
TEL: 0964458888 - 0828133333

Chủ đầu tư:

NGUYỄN THỊ ÁNH NGUYỆT

Địa điểm:

NAM HỒNG - HÀ TĨNH

Tên công trình:

NHÀ Ở GIA ĐÌNH

HỢP ĐỒNG SỐ /HĐ-TK/20.....

CHỦ NHIỆM THIẾT KẾ KTS: NGUYỄN VĂN CƯỜNG	
TRIỂN KHAI KS: HÀNG A LAO	
KIỂM DUYỆT KTS: NGUYỄN TẤT HỘI	

NỘI DUNG ĐIỀU CHỈNH

Lần	Ngày	Duyệt
1	.....	.....
2	.....	.....
3	.....	.....
4	.....	.....
5	.....	.....
6	.....	.....
7	.....	.....

Hạng mục:

KẾT CẤU


Tên bản vẽ:

MB THÉP SÀN NỀN TẦNG 1

	Hà Nội, 12-2025
Phát hành lần 01	Thiết kế
.....	**KC-01-06**

MÓNG M1

SL: 02

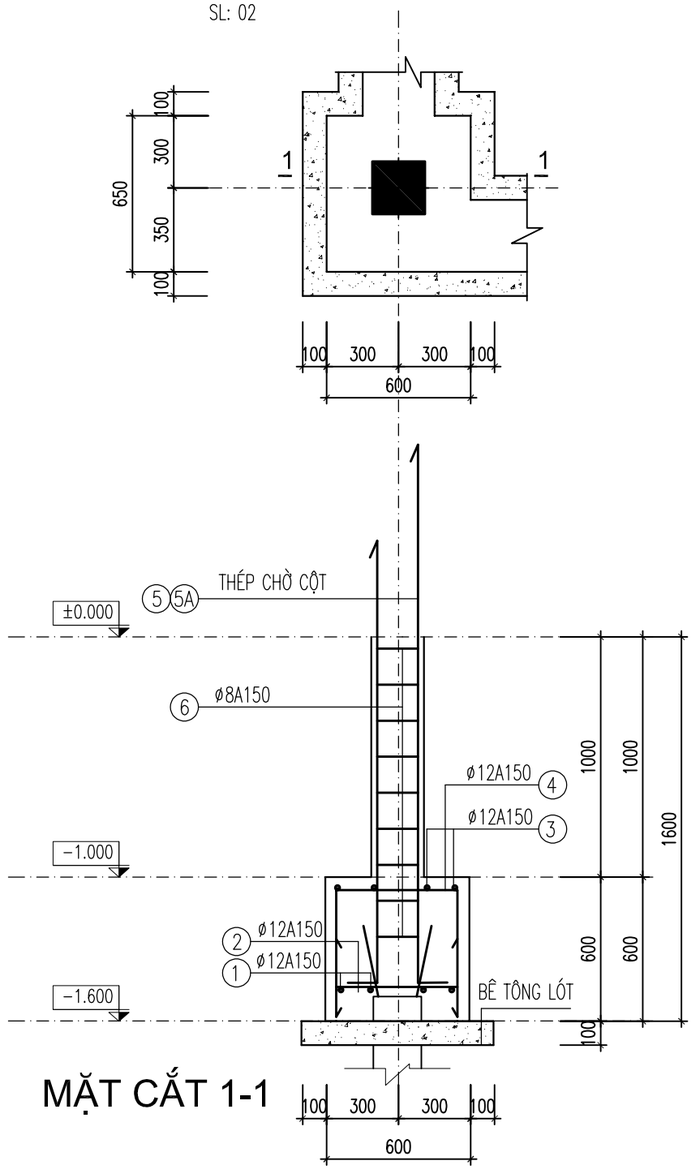


MẶT CẮT 1-1

CHIỀU SÂU MÓNG THI CÔNG THEO THỰC TẾ

MÓNG M2

SL: 03

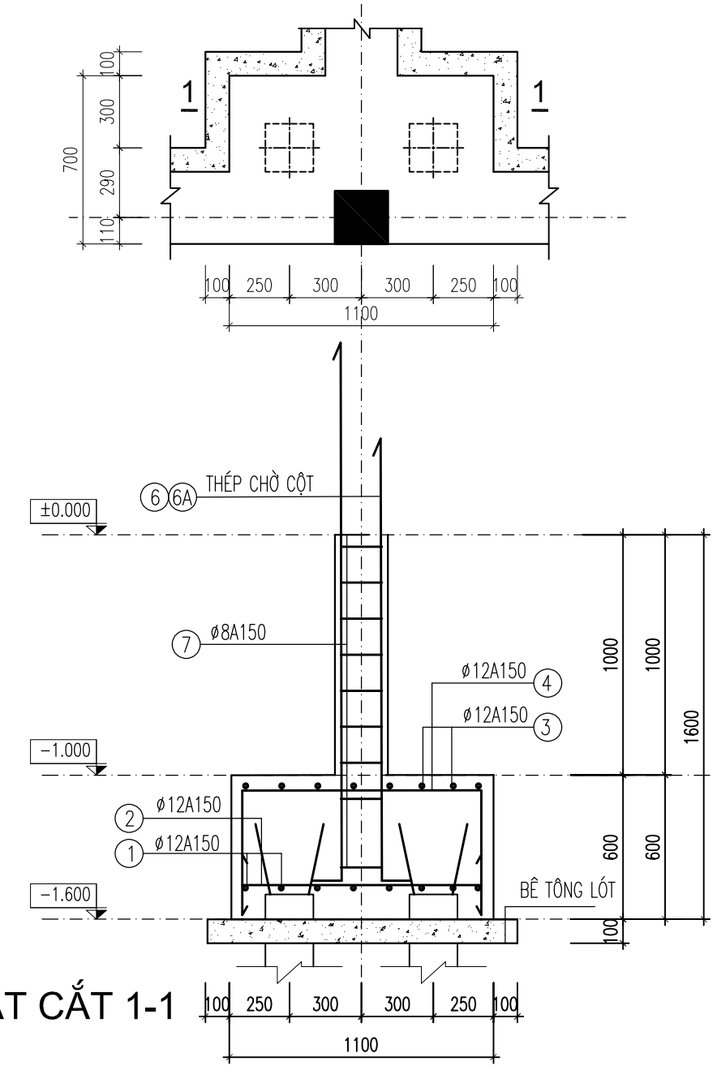

MẶT CẮT 1-1

CHIỀU SÂU MÓNG THI CÔNG THEO THỰC TẾ

CHỦ ĐẦU TƯ CẦN YÊU CẦU KỸ SƯ HIỆN TRƯỜNG KIỂM TRA - RÀ SOÁT BẢN VẼ TRƯỚC KHI THI CÔNG
NẾU CÓ THẮC MẮC VUI LÒNG LIÊN HỆ KIẾN TRÚC SƯ - KỸ SƯ THIẾT KẾ ĐỂ CÓ TƯ VẤN KỊP THỜI TRƯỚC KHI KHỞI CÔNG

HỖ TRỢ TƯ VẤN KỸ THUẬT XÂY DỰNG : 0924099999
LIÊN HỆ MUA VẬT LIỆU MAXHOME : 0921845555 (MIỄN PHÍ VẬN CHUYỂN TOÀN QUỐC)

-BÊ TÔNG LÓT MÓNG ĐÁ 4X6, MÁC 100 -BÊ TÔNG MÓNG, MÁC 250	-BÊ TÔNG CỘT, DẦM, SÀN MÁC 250 -LỚP BÊ TÔNG BẢO VỆ SÀN: 15MM	-LỚP BÊ TÔNG BẢO VỆ CỐT THÉP DẦM: 25MM -LỚP BÊ TÔNG BẢO VỆ CỐT THÉP CỘT: 25MM	-THÉP CB240T (ø<10) KÝ HIỆU (ø) CÓ RA=2100KG/CM2 -THÉP CB300V (10=<ø<=20) KÝ HIỆU (ø) CÓ RA=2600KG/CM2	-THÉP CB300V (20<ø) KÝ HIỆU (ø) CÓ RA=2600KG/CM2 -CHIỀU DÀI THÉP NEO TẠI CÁC VỊ TRÍ LẤY BẰNG 30D	-CẮT NỐI UỐN CỐT THÉP THEO TCXDVN 5574-2018. -KHI THI CÔNG CẦN KẾT HỢP BẢN VẼ KIẾN TRÚC

CÔNG TY TNHH DESIGN AND CONSTRUCTION NEW MAXHOME
HÀ NỘI
ĐC : TẦNG 25, TÒA NHÀ VP TTTM CHỢ MƠ
SỐ 459C PHỐ BẠCH MAI, P. BẠCH MAI
THÀNH PHỐ HÀ NỘI
TEL: 0964458888 - 0828133333

Chủ đầu tư:

NGUYỄN THỊ ÁNH NGUYỆT

Địa điểm:

NAM HỒNG - HÀ TĨNH

Tên công trình:

NHÀ Ở GIA ĐÌNH

HỢP ĐỒNG SỐ /HĐ-TK/20.....

CHỦ NHIỆM THIẾT KẾ KTS: NGUYỄN VĂN CƯỜNG	
TRIỂN KHAI KS: HÀNG A LAO	
KIỂM DUYỆT KTS: NGUYỄN TẤT HỘI	

NỘI DUNG ĐIỀU CHỈNH

Lần	Ngày	Duyệt
1	.....	.....
2	.....	.....
3	.....	.....
4	.....	.....
5	.....	.....
6	.....	.....
7	.....	.....

Hạng mục:

KẾT CẤU


Tên bản vẽ:


CHI TIẾT MÓNG

	Hà Nội, 12-2025
Phát hành lần 01	Thiết kế
.....	**KC-01-07**

MÓNG M3

SL: 08

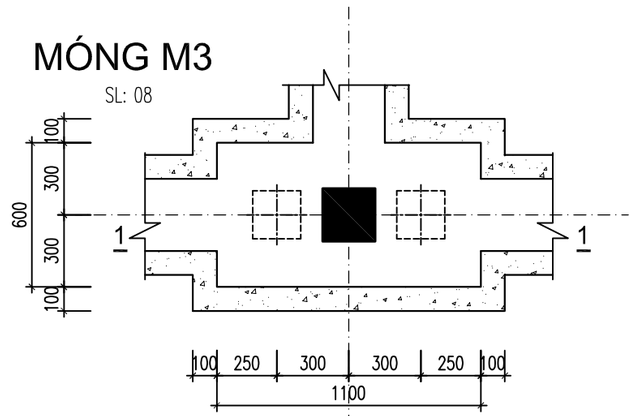

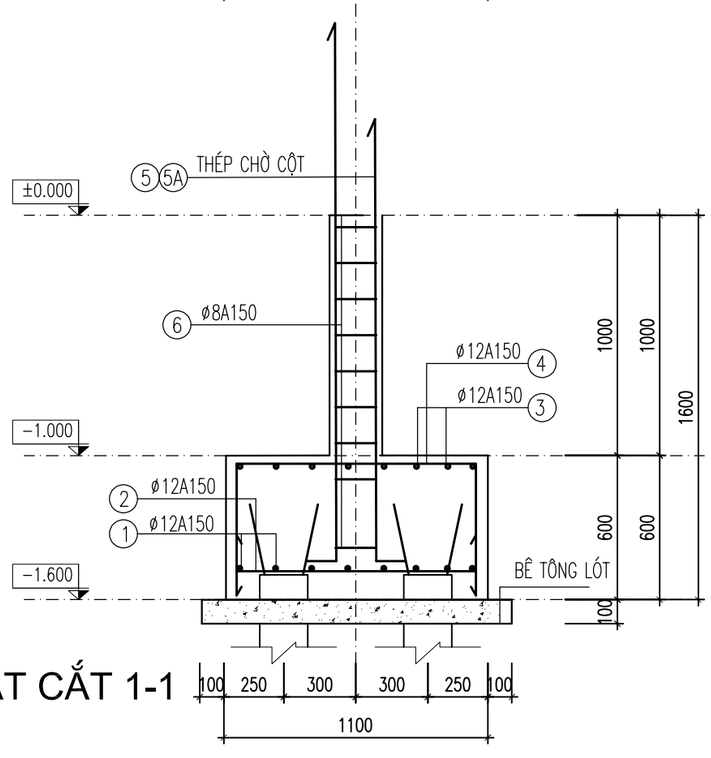



MẶT CẮT 1-1

CHIỀU SÂU MÓNG THI CÔNG THEO THỰC TẾ

MÓNG M4

SL: 02

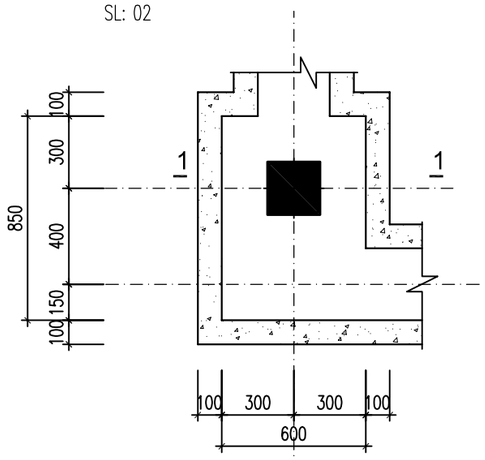

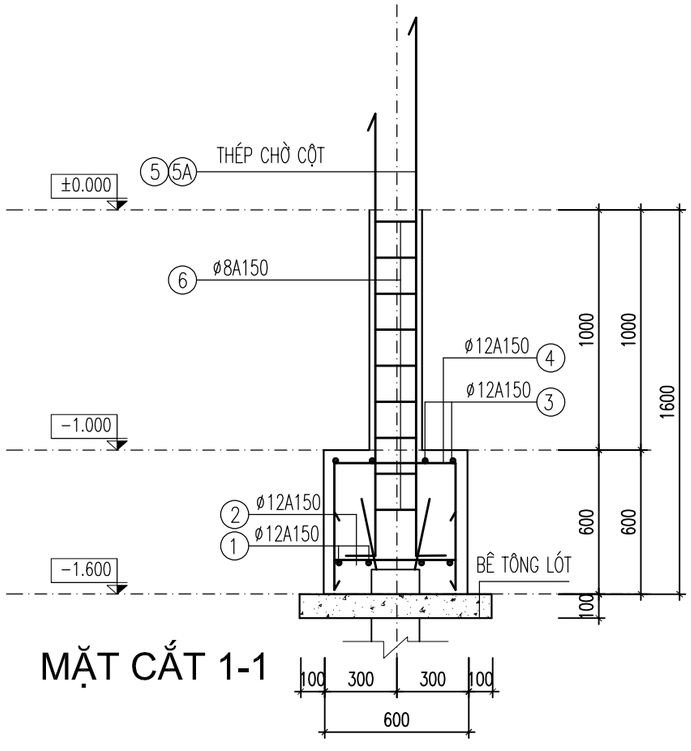

MẶT CẮT 1-1

CHIỀU SÂU MÓNG THI CÔNG THEO THỰC TẾ

CHỦ ĐẦU TƯ CẦN YÊU CẦU KỸ SƯ HIỆN TRƯỜNG KIỂM TRA - RÀ SOÁT BẢN VẼ TRƯỚC KHI THI CÔNG
NẾU CÓ THẮC MẮC VUI LÒNG LIÊN HỆ KIẾN TRÚC SƯ - KỸ SƯ THIẾT KẾ ĐỂ CÓ TƯ VẤN KỊP THỜI TRƯỚC KHI KHỞI CÔNG

HỖ TRỢ TƯ VẤN KỸ THUẬT XÂY DỰNG : 0924099999
LIÊN HỆ MUA VẬT LIỆU MAXHOME : 0921845555 (MIỄN PHÍ VẬN CHUYỂN TOÀN QUỐC)

-BÊ TÔNG LÓT MÓNG ĐÁ 4X6, MÁC 100 -BÊ TÔNG MÓNG, MÁC 250	-BÊ TÔNG CỘT, DẦM, SÀN MÁC 250 -LỚP BÊ TÔNG BẢO VỆ SÀN: 15MM	-LỚP BÊ TÔNG BẢO VỆ CỐT THÉP DẦM: 25MM -LỚP BÊ TÔNG BẢO VỆ CỐT THÉP CỘT: 25MM	-THÉP CB240T (ø<10) KÝ HIỆU (ø) CÓ RA=2100KG/CM2 -THÉP CB300V (10=<ø<=20) KÝ HIỆU (ø) CÓ RA=2600KG/CM2	-THÉP CB300V (20<ø) KÝ HIỆU (ø) CÓ RA=2600KG/CM2 -CHIỀU DÀI THÉP NEO TẠI CÁC VỊ TRÍ LẤY BẰNG 30D	-CẮT NỐI UỐN CỐT THÉP THEO TCXDVN 5574-2018. -KHI THI CÔNG CẦN KẾT HỢP BẢN VẼ KIẾN TRÚC

CÔNG TY TNHH DESIGN AND CONSTRUCTION NEW MAXHOME
HÀ NỘI
ĐC : TẦNG 25, TÒA NHÀ VP TTTM CHỢ MƠ
SỐ 459C PHỐ BẠCH MAI, P. BẠCH MAI
THÀNH PHỐ HÀ NỘI
TEL: 0964458888 - 0828133333

Chủ đầu tư:

NGUYỄN THỊ ÁNH NGUYỆT

Địa điểm:

NAM HỒNG - HÀ TĨNH

Tên công trình:

NHÀ Ở GIA ĐÌNH

HỢP ĐỒNG SỐ /HĐ-TK/20.....

CHỦ NHIỆM THIẾT KẾ KTS: NGUYỄN VĂN CƯỜNG	
TRIỂN KHAI KS: HÀNG A LAO	
KIỂM DUYỆT KTS: NGUYỄN TẤT HỘI	

NỘI DUNG ĐIỀU CHỈNH

Lần	Ngày	Duyệt
1	.....	.....
2	.....	.....
3	.....	.....
4	.....	.....
5	.....	.....
6	.....	.....
7	.....	.....

Hạng mục:


KẾT CẤU

Tên bản vẽ:

CHI TIẾT MÓNG


	Hà Nội, 12-2025
Phát hành lần 01	Thiết kế
.....	**KC-01-08**

CHI TIẾT CỔ CỘT

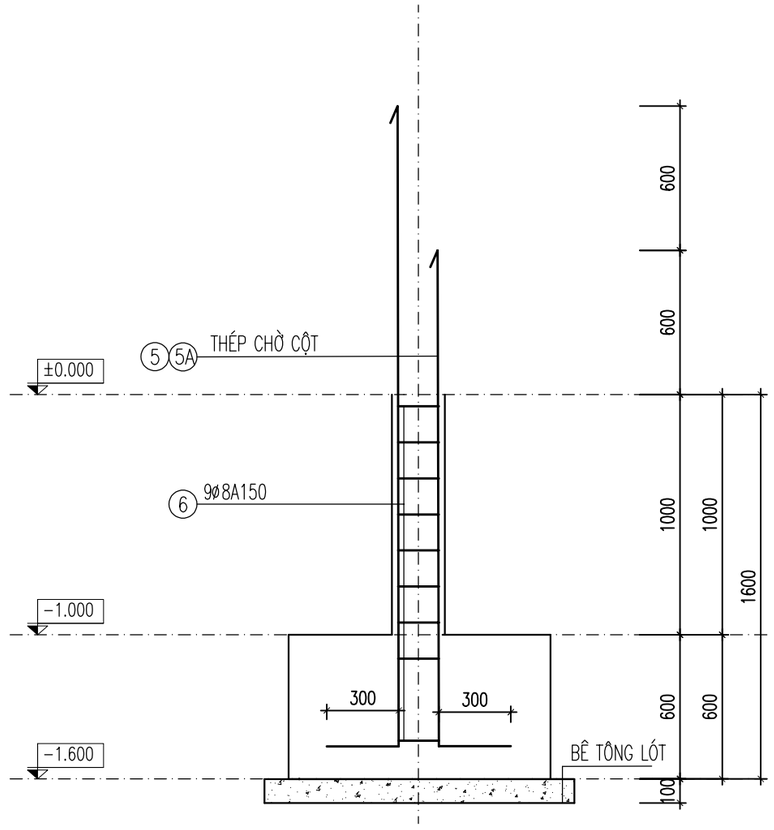

CC

SL: 15

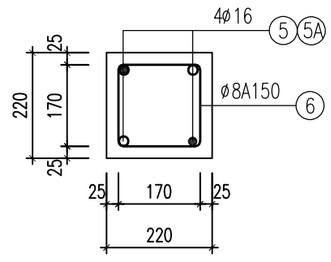

CHIỀU SÂU MÓNG THI CÔNG THEO THỰC TẾ

CHỦ ĐẦU TƯ CẦN YÊU CẦU KỸ SƯ HIỆN TRƯỜNG KIỂM TRA - RÀ SOÁT BẢN VẼ TRƯỚC KHI THI CÔNG
NẾU CÓ THẮC MẮC VUI LÒNG LIÊN HỆ KIẾN TRÚC SƯ - KỸ SƯ THIẾT KẾ ĐỂ CÓ TƯ VẤN KỊP THỜI TRƯỚC KHI KHỞI CÔNG

HỖ TRỢ TƯ VẤN KỸ THUẬT XÂY DỰNG : 0924099999
LIÊN HỆ MUA VẬT LIỆU MAXHOME : 0921845555 (MIỄN PHÍ VẬN CHUYỂN TOÀN QUỐC)

-BÊ TÔNG LÓT MÓNG ĐÁ 4X6, MÁC 100 -BÊ TÔNG MÓNG, MÁC 250	-BÊ TÔNG CỘT, DẦM, SÀN MÁC 250 -LỚP BÊ TÔNG BẢO VỆ SÀN: 15MM	-LỚP BÊ TÔNG BẢO VỆ CỐT THÉP DẦM: 25MM -LỚP BÊ TÔNG BẢO VỆ CỐT THÉP CỘT: 25MM	-THÉP CB240T (ø<10) KÝ HIỆU (ø) CÓ RA=2100KG/CM2 -THÉP CB300V (10=<ø<=20) KÝ HIỆU (ø) CÓ RA=2600KG/CM2	-THÉP CB300V (20<ø) KÝ HIỆU (ø) CÓ RA=2600KG/CM2 -CHIỀU DÀI THÉP NEO TẠI CÁC VỊ TRÍ LẤY BẰNG 30D	-CẮT NỐI UỐN CỐT THÉP THEO TCXDVN 5574-2018. -KHI THI CÔNG CẦN KẾT HỢP BẢN VẼ KIẾN TRÚC

CÔNG TY TNHH DESIGN AND CONSTRUCTION NEW MAXHOME
HÀ NỘI
ĐC : TẦNG 25, TÒA NHÀ VP TTTM CHỢ MƠ
SỐ 459C PHỐ BẠCH MAI, P. BẠCH MAI
THÀNH PHỐ HÀ NỘI
TEL: 0964458888 - 0828133333

Chủ đầu tư:

NGUYỄN THỊ ÁNH NGUYỆT

Địa điểm:

NAM HỒNG - HÀ TĨNH

Tên công trình:

NHÀ Ở GIA ĐÌNH

HỢP ĐỒNG SỐ /HĐ-TK/20.....

CHỦ NHIỆM THIẾT KẾ KTS: NGUYỄN VĂN CƯỜNG	
TRIỂN KHAI KS: HÀNG A LAO	
KIỂM DUYỆT KTS: NGUYỄN TẤT HỘI	

NỘI DUNG ĐIỀU CHỈNH

Lần	Ngày	Duyệt
1	.....	.....
2	.....	.....
3	.....	.....
4	.....	.....
5	.....	.....
6	.....	.....
7	.....	.....

Hạng mục:

KẾT CẤU


Tên bản vẽ:

CHI TIẾT MÓNG

	Hà Nội, 12-2025
Phát hành lần 01	Thiết kế
.....	**KC-01-09**


GM1(30X50)

SL: 01; L=3340MM

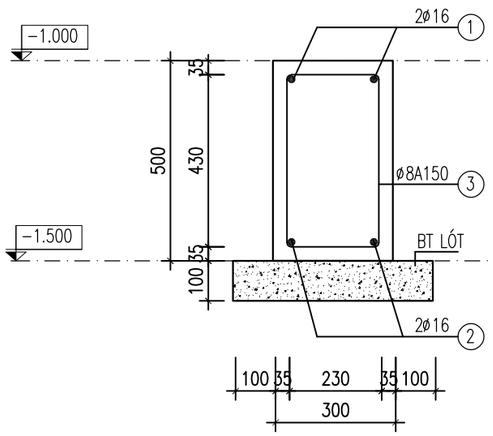


GM2(30X50)

SL: 01; L=12460MM

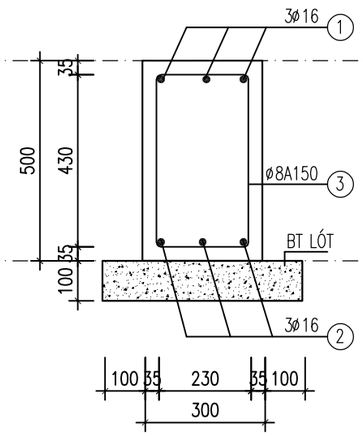


GM3(30X50)

SL: 01; L=12460MM

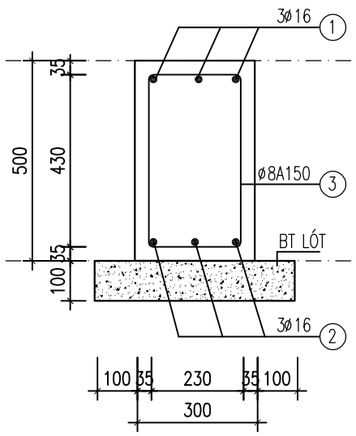


GM4(30X50)

SL: 01; L=11560MM

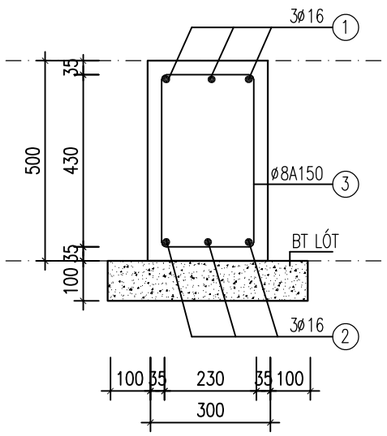


GM5(30X50)

SL: 01; L=8300MM

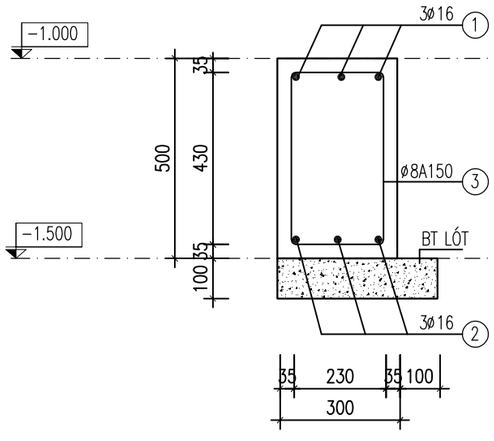


GM6(30X50)

SL: 02; L=1250MM

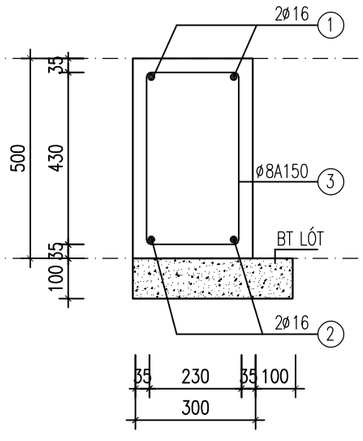


GM7(30X50)

SL: 03; L=3800MM

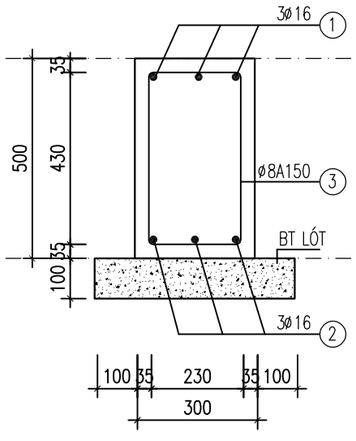

GM8(30X50)

SL: 03; L=4800MM

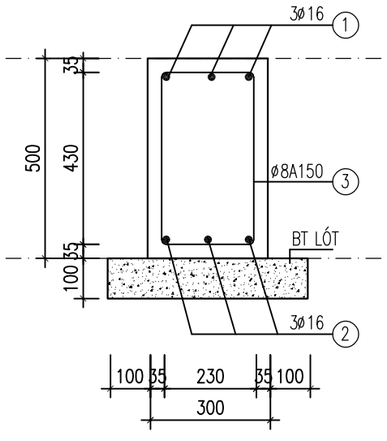

CHỦ ĐẦU TƯ CẦN YÊU CẦU KỸ SƯ HIỆN TRƯỜNG KIỂM TRA - RÀ SOÁT BẢN VẼ TRƯỚC KHI THI CÔNG
NẾU CÓ THẮC MẮC VUI LÒNG LIÊN HỆ KIẾN TRÚC SƯ - KỸ SƯ THIẾT KẾ ĐỂ CÓ TƯ VẤN KỊP THỜI TRƯỚC KHI KHỞI CÔNG

HỖ TRỢ TƯ VẤN KỸ THUẬT XÂY DỰNG : 0924099999
LIÊN HỆ MUA VẬT LIỆU MAXHOME : 0921845555 (MIỄN PHÍ VẬN CHUYỂN TOÀN QUỐC)

-BÊ TÔNG LÓT MÓNG ĐÁ 4X6, MÁC 100 -BÊ TÔNG MÓNG, MÁC 250	-BÊ TÔNG CỘT, DẦM, SÀN MÁC 250 -LỚP BÊ TÔNG BẢO VỆ SÀN: 15MM	-LỚP BÊ TÔNG BẢO VỆ CỐT THÉP DẦM: 25MM -LỚP BÊ TÔNG BẢO VỆ CỐT THÉP CỘT: 25MM	-THÉP CB240T (ø<10) KÝ HIỆU (ø) CÓ RA=2100KG/CM2 -THÉP CB300V (10=<ø<=20) KÝ HIỆU (ø) CÓ RA=2600KG/CM2	-THÉP CB300V (20<ø) KÝ HIỆU (ø) CÓ RA=2600KG/CM2 -CHIỀU DÀI THÉP NEO TẠI CÁC VỊ TRÍ LẤY BẰNG 30D	-CẮT NỐI UỐN CỐT THÉP THEO TCXDVN 5574-2018. -KHI THI CÔNG CẦN KẾT HỢP BẢN VẼ KIẾN TRÚC

CÔNG TY TNHH DESIGN AND CONSTRUCTION NEW MAXHOME
HÀ NỘI
ĐC : TẦNG 25, TÒA NHÀ VP TTTM CHỢ MƠ
SỐ 459C PHỐ BẠCH MAI, P. BẠCH MAI
THÀNH PHỐ HÀ NỘI
TEL: 0964458888 - 0828133333

Chủ đầu tư:

NGUYỄN THỊ ÁNH NGUYỆT

Địa điểm:

NAM HỒNG - HÀ TĨNH

Tên công trình:

NHÀ Ở GIA ĐÌNH

HỢP ĐỒNG SỐ /HĐ-TK/20.....

CHỦ NHIỆM THIẾT KẾ	
KTS: NGUYỄN VĂN CƯỜNG	
TRIỂN KHAI	
KS: HÀNG A LAO	
KIỂM DUYỆT	
KTS: NGUYỄN TẤT HỘI	

NỘI DUNG ĐIỀU CHỈNH

Lần	Ngày	Duyệt
1	.....	.....
2	.....	.....
3	.....	.....
4	.....	.....
5	.....	.....
6	.....	.....
7	.....	.....

Hạng mục:

KẾT CẤU


Tên bản vẽ:

CHI TIẾT MÓNG

	Hà Nội, 12-2025
Phát hành lần 01	Thiết kế
.....	**KC-01-10**


GCT1

SL: 01; L=74700MM

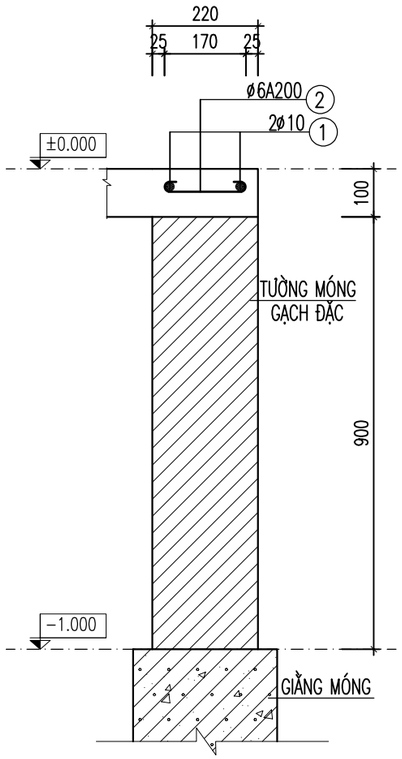


GCT2

SL: 01; L=13600MM

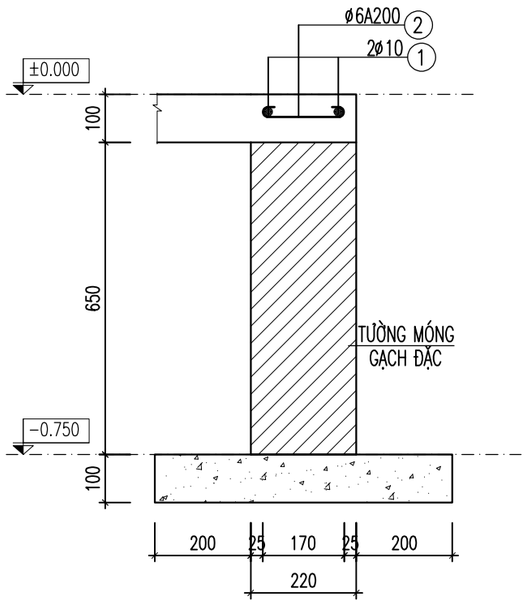


D1(22X30)


SL: 01; L=1680MM

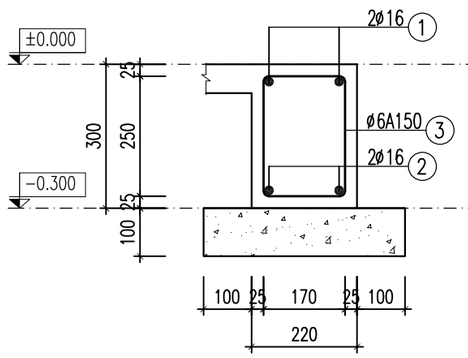

D2(22X30)

SL: 01; L=4720MM

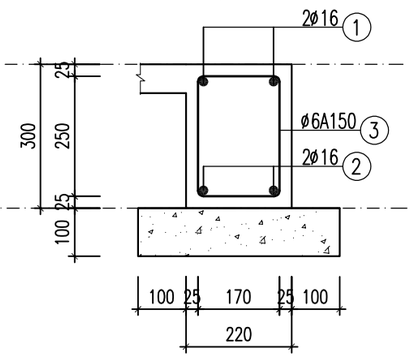

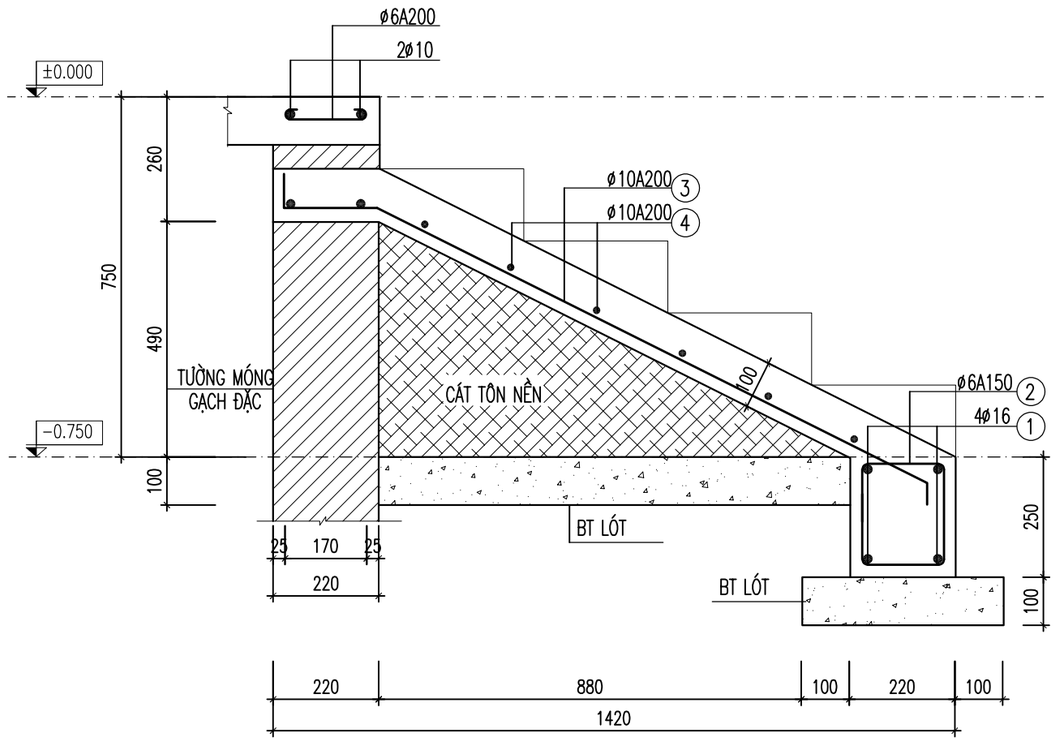

CHI TIẾT NGŨ CẤP 1, 2

CHỦ ĐẦU TƯ CẦN YÊU CẦU KỸ SƯ HIỆN TRƯỜNG KIỂM TRA - RÀ SOÁT BẢN VẼ TRƯỚC KHI THI CÔNG
NẾU CÓ THẮC MẮC VUI LÒNG LIÊN HỆ KIẾN TRÚC SƯ - KỸ SƯ THIẾT KẾ ĐỂ CÓ TƯ VẤN KỊP THỜI TRƯỚC KHI KHỞI CÔNG

HỖ TRỢ TƯ VẤN KỸ THUẬT XÂY DỰNG : 0924099999
LIÊN HỆ MUA VẬT LIỆU MAXHOME : 0921845555 (MIỄN PHÍ VẬN CHUYỂN TOÀN QUỐC)

-BÊ TÔNG LÓT MÓNG ĐÁ 4X6, MÁC 100 -BÊ TÔNG MÓNG, MÁC 250	-BÊ TÔNG CỘT, DẦM, SÀN MÁC 250 -LỚP BÊ TÔNG BẢO VỆ SÀN: 15MM	-LỚP BÊ TÔNG BẢO VỆ CỐT THÉP DẦM: 25MM -LỚP BÊ TÔNG BẢO VỆ CỐT THÉP CỘT: 25MM	-THÉP CB240T (ø<10) KÝ HIỆU (ø) CÓ RA=2100KG/CM2 -THÉP CB300V (10=<ø<=20) KÝ HIỆU (ø) CÓ RA=2600KG/CM2	-THÉP CB300V (20<ø) KÝ HIỆU (ø) CÓ RA=2600KG/CM2 -CHIỀU DÀI THÉP NEO TẠI CÁC VỊ TRÍ LẤY BẰNG 30D	-CẮT NỐI UỐN CỐT THÉP THEO TCXDVN 5574-2018. -KHI THI CÔNG CẦN KẾT HỢP BẢN VẼ KIẾN TRÚC

CÔNG TY TNHH DESIGN AND CONSTRUCTION NEW MAXHOME
HÀ NỘI
ĐC : TẦNG 25, TÒA NHÀ VP TTTM CHỢ MƠ
SỐ 459C PHỐ BẠCH MAI, P. BẠCH MAI
THÀNH PHỐ HÀ NỘI
TEL: 0964458888 - 0828133333

Chủ đầu tư:

NGUYỄN THỊ ÁNH NGUYỆT

Địa điểm:

NAM HỒNG - HÀ TĨNH

Tên công trình:

NHÀ Ở GIA ĐÌNH

HỢP ĐỒNG SỐ /HĐ-TK/20.....

CHỦ NHIỆM THIẾT KẾ	
KTS: NGUYỄN VĂN CƯỜNG	
TRIỂN KHAI	
KS: HÀNG A LAO	
KIỂM DUYỆT	
KTS: NGUYỄN TẤT HỘI	

NỘI DUNG ĐIỀU CHỈNH

Lần	Ngày	Duyệt
1	.....	.....
2	.....	.....
3	.....	.....
4	.....	.....
5	.....	.....
6	.....	.....
7	.....	.....

Hạng mục:

KẾT CẤU

Tên bản vẽ:

CHI TIẾT MÓNG

	Hà Nội, 12-2025
Phát hành lần 01	Thiết kế
.....	**KC-01-11**

BẢNG THỐNG KÊ CỐT THÉP

TÊN C.KIỆN	SỐ HIỆU	HÌNH DẠNG - KÍCH THƯỚC	ĐƯỜNG KÍNH (mm)	CHIỀU DÀI 1 THANH (mm)	SỐ LƯỢNG 1 C.KIỆN	SỐ LƯỢNG T.BỘ	TỔNG CHIỀU DÀI (m)	TỔNG T.LƯỢNG (Kg)
M1 Số lượng: 2	1	200 | 600 | 200	12	1000	4	8	8	7.10
	2	200 | 550 | 200	12	950	5	10	9.5	8.43
	3	500 | 600 | 500	12	1600	4	8	12.8	11.36
	4	500 | 550 | 500	12	1550	5	10	15.5	13.76
M2 Số lượng: 3	1	200 | 650 | 200	12	1050	8	24	25.2	22.37
	2	200 | 1050 | 200	12	1450	5	15	21.75	19.31
	3	500 | 650 | 500	12	1650	8	24	39.6	35.16
	4	500 | 1050 | 500	12	2050	5	15	30.75	27.30
M3 Số lượng: 8	1	200 | 550 | 200	12	950	8	64	60.8	53.98
	2	200 | 1050 | 200	12	1450	4	32	46.4	41.19
	3	500 | 550 | 500	12	1550	8	64	99.2	88.07
	4	500 | 1050 | 500	12	2050	4	32	65.6	58.24
M4 Số lượng: 2	1	200 | 800 | 200	12	1200	4	8	9.6	8.52
	2	200 | 550 | 200	12	950	5	10	9.5	8.43
	3	500 | 800 | 500	12	1800	4	8	14.4	12.78
	4	500 | 550 | 500	12	1550	5	10	15.5	13.76
CC Số lượng: 15	5	300 | 2100	16	2400	2	30	72	113.64
	5A	300 | 2700	16	3000	2	30	90	142.05
	6	170 | 170 | 80	8	840	9	135	113.4	44.75

- Trọng lượng thép có đường kính Φ8 = 44.75 kg; Chiều dài = 113.4 mét
- Trọng lượng thép có đường kính Φ12 = 429.76 kg; Chiều dài = 484.1 mét
- Trọng lượng thép có đường kính Φ16 = 255.69 kg; Chiều dài = 162 mét

BẢNG THỐNG KÊ CỐT THÉP

TÊN C.KIỆN	SỐ HIỆU	HÌNH DẠNG - KÍCH THƯỚC	ĐƯỜNG KÍNH (mm)	CHIỀU DÀI 1 THANH (mm)	SỐ LƯỢNG 1 C.KIỆN	SỐ LƯỢNG T.BỘ	TỔNG CHIỀU DÀI (m)	TỔNG T.LƯỢNG (Kg)
GM1 Số lượng: 1	1	400 | 3250 | 400	16	4050	2	2	8.1	12.78
	2	3250	16	3250	2	2	6.5	10.26
	3	430 | 230 | 80	8	1480	21	21	31.08	12.26
GM2 Số lượng: 1	1	400 | 12400 | 400	16	13680	3	3	41.04	64.77
	2	12400	16	12880	3	3	38.64	60.99
	3	430 | 230 | 80	8	1480	82	82	121.36	47.89
GM3 Số lượng: 1	1	400 | 12400 | 400	16	13680	3	3	41.04	64.77
	2	12400	16	12880	3	3	38.64	60.99
	3	430 | 230 | 80	8	1480	82	82	121.36	47.89
GM4 Số lượng: 1	1	400 | 11500 | 400	16	12780	3	3	38.34	60.51
	2	11500	16	11500	3	3	34.5	54.45
	3	430 | 230 | 80	8	1480	76	76	112.48	44.38
GM5 Số lượng: 1	1	400 | 8250 | 400	16	9050	3	3	27.15	42.85
	2	8250	16	8250	3	3	24.75	39.06
	3	430 | 230 | 80	8	1480	55	55	81.4	32.12
GM6 Số lượng: 2	1	400 | 1200 | 400	16	2000	2	4	8	12.63
	2	1200	16	1200	2	4	4.8	7.58
	3	430 | 230 | 80	8	1480	8	16	23.68	9.34
GM7 Số lượng: 3	1	400 | 3750 | 400	16	4550	3	9	40.95	64.63
	2	3750	16	3750	3	9	33.75	53.27
	3	430 | 230 | 80	8	1480	24	72	106.56	42.05
GM8 Số lượng: 3	1	400 | 4750 | 400	16	5550	3	9	49.95	78.84
	2	4750	16	4750	3	9	42.75	67.47
	3	430 | 230 | 80	8	1480	31	93	137.64	54.31

- Trọng lượng thép có đường kính Φ8 = 290.24 kg; Chiều dài = 735.56 mét
- Trọng lượng thép có đường kính Φ16 = 755.85 kg; Chiều dài = 478.9 mét

CHỦ ĐẦU TƯ CẦN YÊU CẦU KỸ SƯ HIỆN TRƯỜNG KIỂM TRA - RÀ SOÁT BẢN VẼ TRƯỚC KHI THI CÔNG
NẾU CÓ THẮC MẮC VUI LÒNG LIÊN HỆ KIẾN TRÚC SƯ - KỸ SƯ THIẾT KẾ ĐỂ CÓ TƯ VẤN KỊP THỜI TRƯỚC KHI KHỞI CÔNG

HỖ TRỢ TƯ VẤN KỸ THUẬT XÂY DỰNG : 0924099999
LIÊN HỆ MUA VẬT LIỆU MAXHOME : 0921845555 (MIỄN PHÍ VẬN CHUYỂN TOÀN QUỐC)

- BÊ TÔNG LÓT MÓNG ĐÁ 4X6, MÁC 100
- BÊ TÔNG MÓNG, MÁC 250
- BÊ TÔNG CỘT, DẦM, SÀN MÁC 250
- LỚP BÊ TÔNG BẢO VỆ SÀN: 15MM
- LỚP BÊ TÔNG BẢO VỆ CỐT THÉP DẦM: 25MM
- LỚP BÊ TÔNG BẢO VỆ CỐT THÉP CỘT: 25MM
- THÉP CB240T (ø<10) KÝ HIỆU (ø) CÓ RA=2100KG/CM2
- THÉP CB300V (10=<ø<=20) KÝ HIỆU (ø) CÓ RA=2600KG/CM2
- THÉP CB300V (20<ø) KÝ HIỆU (ø) CÓ RA=2600KG/CM2
- CHIỀU DÀI THÉP NEO TẠI CÁC VỊ TRÍ LẤY BẰNG 30D
- CẮT NỐI UỐN CỐT THÉP THEO TCXDVN 5574-2018.
- KHI THI CÔNG CẦN KẾT HỢP BẢN VẼ KIẾN TRÚC

CÔNG TY TNHH DESIGN AND CONSTRUCTION NEW MAXHOME
HÀ NỘI
ĐC : TẦNG 25, TÒA NHÀ VP TTTM CHỢ MƠ
SỐ 459C PHỐ BẠCH MAI, P. BẠCH MAI
THÀNH PHỐ HÀ NỘI
TEL: 0964458888 - 0828133333

Chủ đầu tư:

NGUYỄN THỊ ÁNH NGUYỆT

Địa điểm:

NAM HỒNG - HÀ TĨNH

Tên công trình:

NHÀ Ở GIA ĐÌNH

HỢP ĐỒNG SỐ /HĐ-TK/20.....

CHỦ NHIỆM THIẾT KẾ KTS: NGUYỄN VĂN CƯỜNG	
TRIỂN KHAI KS: HÀNG A LAO	
KIỂM DUYỆT KTS: NGUYỄN TẤT HỘI	

NỘI DUNG ĐIỀU CHỈNH

Lần	Ngày	Duyệt
1	.....	.....
2	.....	.....
3	.....	.....
4	.....	.....
5	.....	.....
6	.....	.....
7	.....	.....

Hạng mục:

KẾT CẤU

Tên bản vẽ:

TK THÉP MÓNG

	Hà Nội, 12-2025
Phát hành lần 01	Thiết kế
.....	**KC-01-12**

BẢNG THỐNG KÊ CỐT THÉP

TÊN C.KIỆN	SỐ HIỆU	HÌNH DẠNG - KÍCH THƯỚC	ĐƯỜNG KÍNH (mm)	CHIỀU DÀI 1 THANH (mm)	SỐ LƯỢNG		TỔNG CHIỀU DÀI (m)	TỔNG T.LƯỢNG (Kg)
					1 C.KIỆN	T.BỘ		
GCT1 Số lượng: 1	1	74700	10	76500	2	2	153	94.33
	2	50 170 50	6	270	373	373	100.71	22.35
GCT2 Số lượng: 1	1	13600	10	13900	2	2	27.8	17.14
	2	50 170 50	6	270	68	68	18.36	4.08
D1 Số lượng: 1	1	250 1600 250	16	2100	2	2	4.2	6.63
	2	1600	16	1600	2	2	3.2	5.05
	3	250 170 50	6	940	10	10	9.4	2.09
D2 Số lượng: 1	1	250 4650 250	16	5150	2	2	10.3	16.26
	2	4650	16	4650	2	2	9.3	14.68
	3	250 170 50	6	940	30	30	28.2	6.26
NGŨ CẤP 1 Số lượng: 1	1	200 2300 200	16	2700	4	4	10.8	17.05
	2	200 170 50	6	840	15	15	12.6	2.80
	3	100 1600 100	10	1800	11	11	19.8	12.21
	4	80 2300 80	10	2460	8	8	19.68	12.13
NGŨ CẤP 2 Số lượng: 1	1	200 3400 200	16	3800	4	4	15.2	23.99
	2	200 170 50	6	840	22	22	18.48	4.10
	3	100 1600 100	10	1800	17	17	30.6	18.87
	4	80 3400 80	10	3560	8	8	28.48	17.56
SÀN NỀN Số lượng: 1	1	80 3300 80	10	3460	3	3	10.38	6.40
	2	80 12350 80	10	12810	17	17	217.77	134.26
	3	80 11450 80	10	11610	13	13	150.93	93.05
	4	80 8150 80	10	8310	32	32	265.92	163.95
	5	80 9100 80	10	9260	12	12	111.12	68.51
	6	80 4650 80	10	4810	4	4	19.24	11.86

- Trọng lượng thép có đường kính Φ6 = 41.68 kg; Chiều dài = 187.75 mét
- Trọng lượng thép có đường kính Φ10 = 650.27 kg; Chiều dài = 1054.72 mét
- Trọng lượng thép có đường kính Φ16 = 83.66 kg; Chiều dài = 53 mét

CHỦ ĐẦU TƯ CẦN YÊU CẦU KỸ SƯ HIỆN TRƯỜNG KIỂM TRA - RÀ SOÁT BẢN VẼ TRƯỚC KHI THI CÔNG
NẾU CÓ THẮC MẮC VUI LÒNG LIÊN HỆ KIẾN TRÚC SƯ - KỸ SƯ THIẾT KẾ ĐỂ CÓ TƯ VẤN KỊP THỜI TRƯỚC KHI KHỞI CÔNG

HỖ TRỢ TƯ VẤN KỸ THUẬT XÂY DỰNG : 0924099999
LIÊN HỆ MUA VẬT LIỆU MAXHOME : 0921845555 (MIỄN PHÍ VẬN CHUYỂN TOÀN QUỐC)

-BÊ TÔNG LÓT MÓNG ĐÁ 4X6, MÁC 100 -BÊ TÔNG MÓNG, MÁC 250	-BÊ TÔNG CỘT, DẦM, SÀN MÁC 250 -LỚP BÊ TÔNG BẢO VỆ SÀN: 15MM	-LỚP BÊ TÔNG BẢO VỆ CỐT THÉP DẦM: 25MM -LỚP BÊ TÔNG BẢO VỆ CỐT THÉP CỘT: 25MM	-THÉP CB240T (ø<10) KÝ HIỆU (ø) CÓ RA=2100KG/CM2 -THÉP CB300V (10=<ø<=20) KÝ HIỆU (ø) CÓ RA=2600KG/CM2	-THÉP CB300V (20<ø) KÝ HIỆU (ø) CÓ RA=2600KG/CM2 -CHIỀU DÀI THÉP NEO TẠI CÁC VỊ TRÍ LẤY BẰNG 30D	-CẮT NỐI UỐN CỐT THÉP THEO TCXDVN 5574-2018. -KHI THI CÔNG CẦN KẾT HỢP BẢN VẼ KIẾN TRÚC

CÔNG TY TNHH DESIGN AND CONSTRUCTION NEW MAXHOME
HÀ NỘI
ĐC : TẦNG 25, TÒA NHÀ VP TTTM CHỢ MƠ
SỐ 459C PHỐ BẠCH MAI, P. BẠCH MAI
THÀNH PHỐ HÀ NỘI
TEL: 0964458888 - 0828133333

Chủ đầu tư:

NGUYỄN THỊ ÁNH NGUYỆT

Địa điểm:

NAM HỒNG - HÀ TĨNH

Tên công trình:

NHÀ Ở GIA ĐÌNH

HỢP ĐỒNG SỐ /HĐ-TK/20.....

CHỦ NHIỆM THIẾT KẾ	
KTS: NGUYỄN VĂN CƯỜNG	
TRIỂN KHAI	
KS: HÀNG A LAO	
KIỂM DUYỆT	
KTS: NGUYỄN TẤT HỘI	

NỘI DUNG ĐIỀU CHỈNH

Lần	Ngày	Duyệt
1	.....	.....
2	.....	.....
3	.....	.....
4	.....	.....
5	.....	.....
6	.....	.....
7	.....	.....

Hạng mục:


KẾT CẤU

Tên bản vẽ:


TK THÉP MÓNG

	Hà Nội, 12-2025
Phát hành lần 01	Thiết kế
.....	**KC-01-13**

MẶT BẰNG BỂ PHỐT

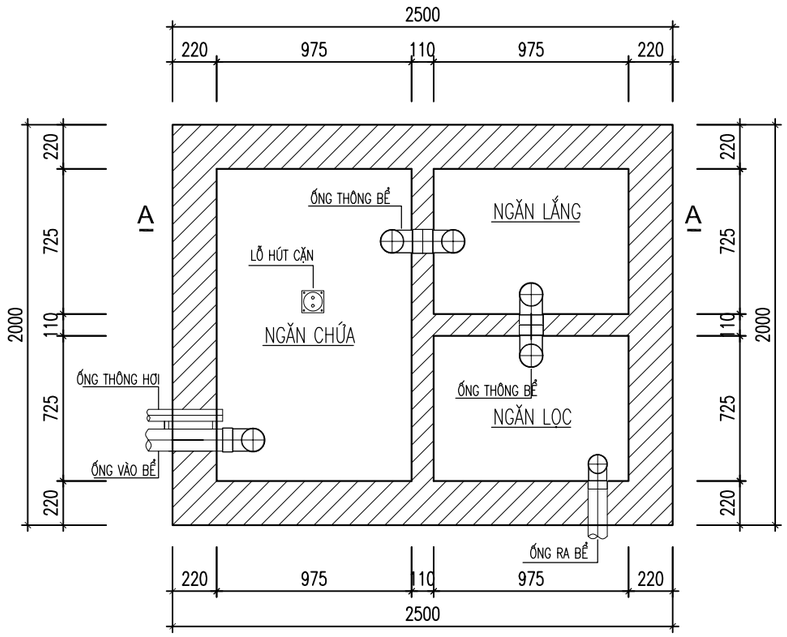


MẶT BẰNG KÊ TẤM ĐAN

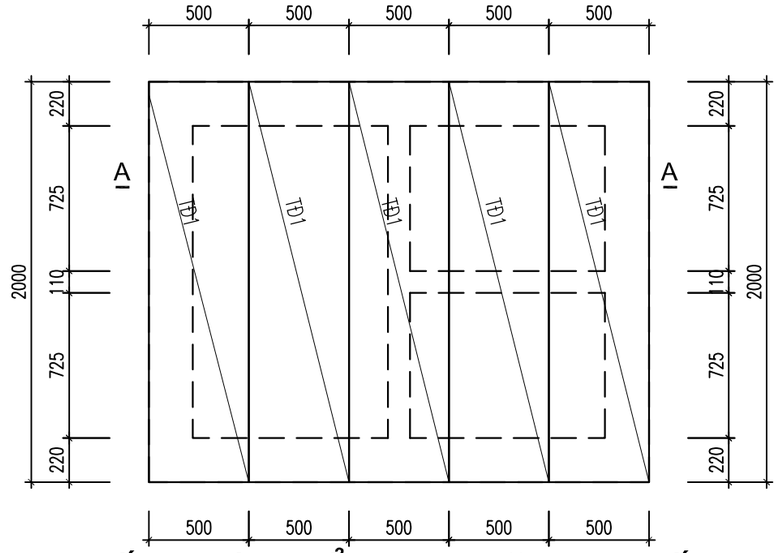


TẤM ĐAN


TĐ1; SL:5

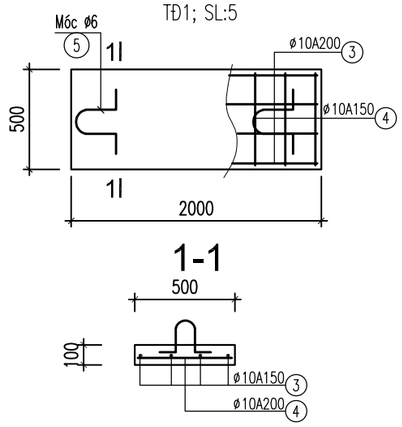


MẶT CẮT A-A

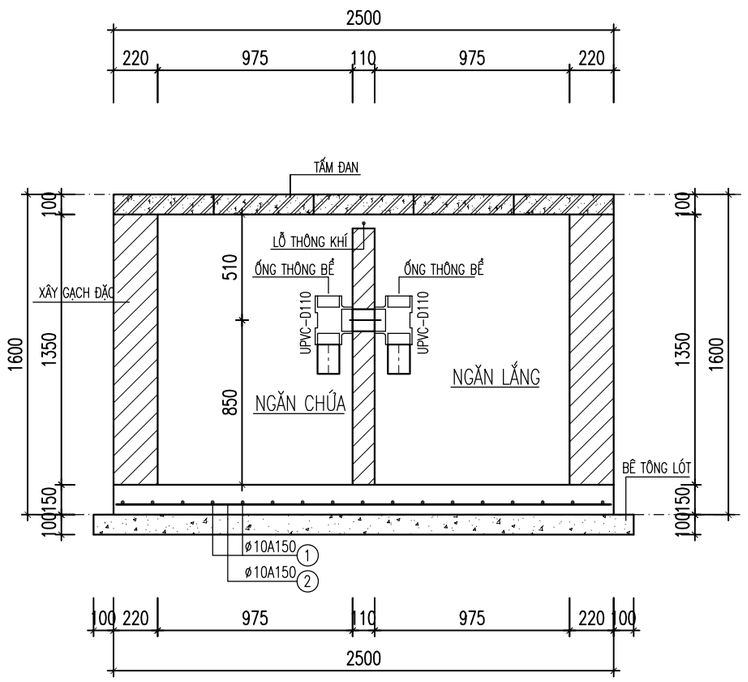


ỐNG VÀO BỂ + HÚT CẶN

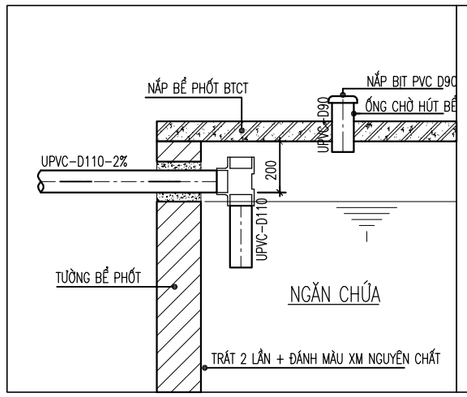

ỐNG THÔNG HƠI

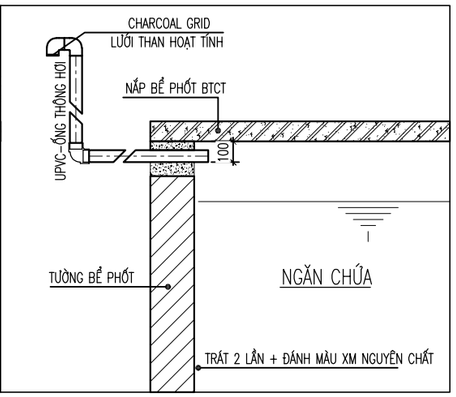

ỐNG RA BỂ

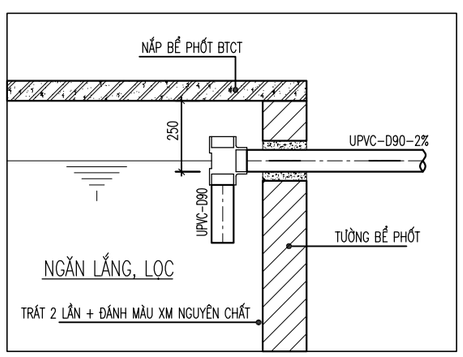

CÔNG TY TNHH DESIGN AND CONSTRUCTION NEW MAXHOME
HÀ NỘI
ĐC : TẦNG 25, TÒA NHÀ VP TTTM CHỢ MƠ
SỐ 459C PHỐ BẠCH MAI, P. BẠCH MAI
THÀNH PHỐ HÀ NỘI
TEL: 0964458888 - 0828133333

Chủ đầu tư:

NGUYỄN THỊ ÁNH NGUYỆT

Địa điểm:

NAM HỒNG - HÀ TĨNH

Tên công trình:

NHÀ Ở GIA ĐÌNH

HỢP ĐỒNG SỐ /HĐ-TK/20.....

CHỦ NHIỆM THIẾT KẾ	
KTS: NGUYỄN VĂN CƯỜNG	
TRIỂN KHAI	
KS: HÀNG A LAO	
KIỂM DUYỆT	
KTS: NGUYỄN TẤT HỘI	

NỘI DUNG ĐIỀU CHỈNH

Lần	Ngày	Duyệt
1	.....	.....
2	.....	.....
3	.....	.....
4	.....	.....
5	.....	.....
6	.....	.....
7	.....	.....

Hạng mục:

KẾT CẤU

Tên bản vẽ:

CHI TIẾT BỂ PHỐT

CHỦ ĐẦU TƯ CẦN YÊU CẦU KỸ SƯ HIỆN TRƯỜNG KIỂM TRA - RÀ SOÁT BẢN VẼ TRƯỚC KHI THI CÔNG
NẾU CÓ THẮC MẮC VUI LÒNG LIÊN HỆ KIẾN TRÚC SƯ - KỸ SƯ THIẾT KẾ ĐỂ CÓ TƯ VẤN KỊP THỜI TRƯỚC KHI KHỞI CÔNG

HỖ TRỢ TƯ VẤN KỸ THUẬT XÂY DỰNG : 0924099999
LIÊN HỆ MUA VẬT LIỆU MAXHOME : 0921845555 (MIỄN PHÍ VẬN CHUYỂN TOÀN QUỐC)

-BÊ TÔNG LÓT MÓNG ĐÁ 4X6, MÁC 100 -BÊ TÔNG MÓNG, MÁC 250	-BÊ TÔNG CỘT, DẦM, SÀN MÁC 250 -LỚP BÊ TÔNG BẢO VỆ SÀN: 15MM	-LỚP BÊ TÔNG BẢO VỆ CỐT THÉP DẦM: 25MM -LỚP BÊ TÔNG BẢO VỆ CỐT THÉP CỘT: 25MM	-THÉP CB240T (ø<10) KÝ HIỆU (ø) CÓ RA=2100KG/CM2 -THÉP CB300V (10=<ø<=20) KÝ HIỆU (ø) CÓ RA=2600KG/CM2	-THÉP CB300V (20<ø) KÝ HIỆU (ø) CÓ RA=2600KG/CM2 -CHIỀU DÀI THÉP NEO TẠI CÁC VỊ TRÍ LẤY BẰNG 30D	-CẮT NỐI UỐN CỐT THÉP THEO TCXDVN 5574-2018. -KHI THI CÔNG CẦN KẾT HỢP BẢN VẼ KIẾN TRÚC

	Hà Nội, 12-2025
Phát hành lần 01	Thiết kế
.....	**KC-02-01**

BẢNG THỐNG KÊ CỐT THÉP

TÊN C.KIỆN	SỐ HIỆU	HÌNH DẠNG - KÍCH THƯỚC	ĐƯỜNG KÍNH (mm)	CHIỀU DÀI 1 THANH (mm)	SỐ LƯỢNG		TỔNG CHIỀU DÀI (m)	TỔNG T.LƯỢNG (Kg)
					1 C.KIỆN	T.BỘ		
ĐÁY BỂ Số lượng: 1	1	2450	10	2450	12	12	29.4	18.13
	2	1950	10	1950	15	15	29.25	18.03
TẤM ĐAN Số lượng: 5	3	1950	10	1950	4	20	39	24.04
	4	460	10	460	13	65	29.9	18.43
	5	60 → 150 150 150 150	6	788.4	2	10	7.884	1.75

- Trọng lượng thép có đường kính Φ6 = 1.75 kg; Chiều dài = 7.88 mét
- Trọng lượng thép có đường kính Φ10 = 78.63 kg; Chiều dài = 127.55 mét

CHỦ ĐẦU TƯ CẦN YÊU CẦU KỸ SƯ HIỆN TRƯỜNG KIỂM TRA - RÀ SOÁT BẢN VẼ TRƯỚC KHI THI CÔNG
NẾU CÓ THẮC MẮC VUI LÒNG LIÊN HỆ KIẾN TRÚC SƯ - KỸ SƯ THIẾT KẾ ĐỂ CÓ TƯ VẤN KỊP THỜI TRƯỚC KHI KHỞI CÔNG

HỖ TRỢ TƯ VẤN KỸ THUẬT XÂY DỰNG : 0924099999
LIÊN HỆ MUA VẬT LIỆU MAXHOME : 0921845555 (MIỄN PHÍ VẬN CHUYỂN TOÀN QUỐC)

-BÊ TÔNG LÓT MÓNG ĐÁ 4X6, MÁC 100 -BÊ TÔNG MÓNG, MÁC 250	-BÊ TÔNG CỘT, DẦM, SÀN MÁC 250 -LỚP BÊ TÔNG BẢO VỆ SÀN: 15MM	-LỚP BÊ TÔNG BẢO VỆ CỐT THÉP DẦM: 25MM -LỚP BÊ TÔNG BẢO VỆ CỐT THÉP CỘT: 25MM	-THÉP CB240T (ø<10) KÝ HIỆU (ø) CÓ RA=2100KG/CM2 -THÉP CB300V (10=<ø<=20) KÝ HIỆU (ø) CÓ RA=2600KG/CM2	-THÉP CB300V (20<ø) KÝ HIỆU (ø) CÓ RA=2600KG/CM2 -CHIỀU DÀI THÉP NEO TẠI CÁC VỊ TRÍ LẤY BẰNG 30D	-CẮT NỐI UỐN CỐT THÉP THEO TCXDVN 5574-2018. -KHI THI CÔNG CẦN KẾT HỢP BẢN VẼ KIẾN TRÚC

CÔNG TY TNHH DESIGN AND CONSTRUCTION NEW MAXHOME
HÀ NỘI
ĐC : TẦNG 25, TÒA NHÀ VP TTTM CHỢ MƠ
SỐ 459C PHỐ BẠCH MAI, P. BẠCH MAI
THÀNH PHỐ HÀ NỘI
TEL: 0964458888 - 0828133333

Chủ đầu tư:
NGUYỄN THỊ ÁNH NGUYỆT

Địa điểm:
NAM HỒNG - HÀ TĨNH

Tên công trình:
NHÀ Ở GIA ĐÌNH

HỢP ĐỒNG SỐ /HĐ-TK/20.....

CHỦ NHIỆM THIẾT KẾ KTS: NGUYỄN VĂN CƯỜNG	
TRIỂN KHAI KS: HÀNG A LAO	
KIỂM DUYỆT KTS: NGUYỄN TẤT HỘI	


NỘI DUNG ĐIỀU CHỈNH

Lần	Ngày	Duyệt
1	.....	.....
2	.....	.....
3	.....	.....
4	.....	.....
5	.....	.....
6	.....	.....
7	.....	.....


Hạng mục:
KẾT CẤU

Tên bản vẽ:
TK THÉP BỂ PHỐT


	Hà Nội, 12-2025
Phát hành lần 01	Thiết kế
.....	**KC-02-02**

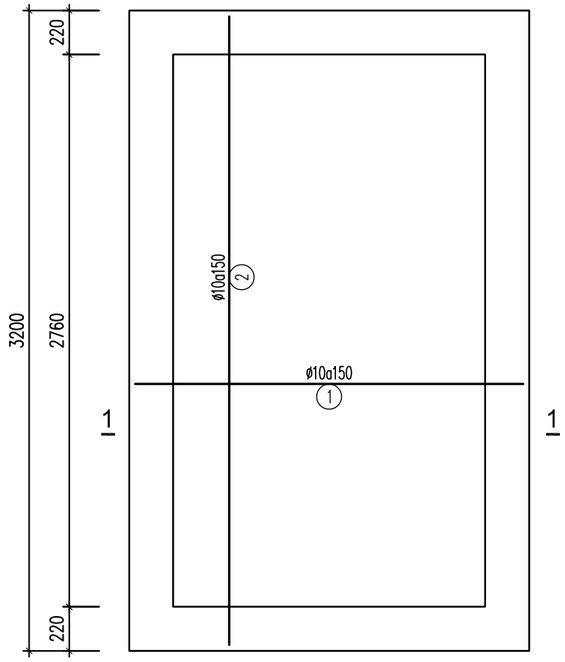


MẶT BẰNG ĐÁY BỂ NƯỚC

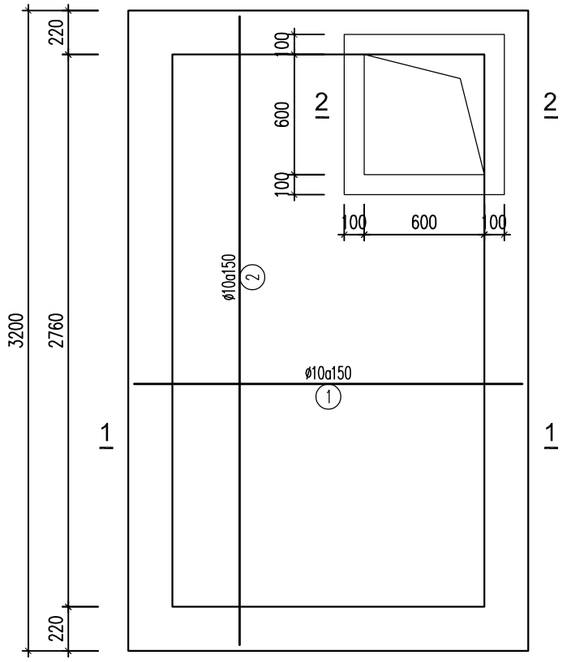


MẶT BẰNG NẮP BỂ NƯỚC

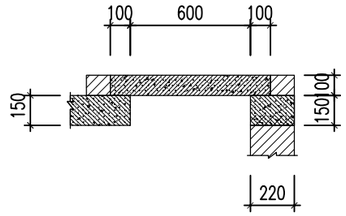


MẶT CẮT 2-2

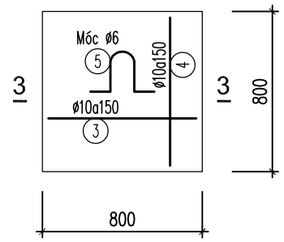

CHI TIẾT NẮP BỂ NƯỚC

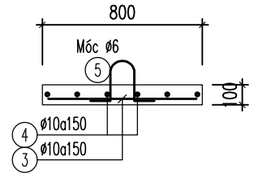

MẶT CẮT 3-3

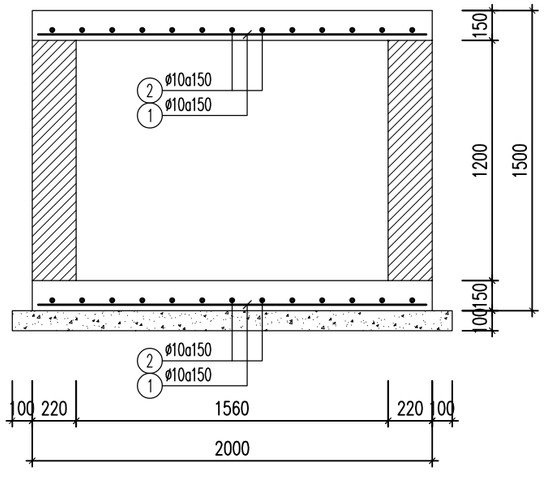

MẶT CẮT 1-1

BẢNG THỐNG KÊ CỐT THÉP

TÊN C.KIỆN	SỐ HIỆU	HÌNH DẠNG - KÍCH THƯỚC	ĐƯỜNG KÍNH (mm)	CHIỀU DÀI 1 THANH (mm)	SỐ LƯỢNG 1 C.KIỆN	SỐ LƯỢNG T.BỘ	TỔNG CHIỀU DÀI (m)	TỔNG T.LƯỢNG (Kg)
BỂ NƯỚC Số lượng: 1	1	1920	10	1920	42	42	80.64	49.72
	2	3170	10	3170	27	27	85.59	52.77
	3	720	10	720	4	4	2.88	1.78
	4	720	10	720	4	4	2.88	1.78
	5	60, 150, 150, 150, 150	6	788.4	1	1	0.7884	0.17

- Trọng lượng thép có đường kính Φ6 = 0.17 kg; Chiều dài = 0.79 mét
- Trọng lượng thép có đường kính Φ10 = 106.05 kg; Chiều dài = 171.99 mét

CHỦ ĐẦU TƯ CẦN YÊU CẦU KỸ SƯ HIỆN TRƯỜNG KIỂM TRA - RÀ SOÁT BẢN VẼ TRƯỚC KHI THI CÔNG
NẾU CÓ THẮC MẮC VUI LÒNG LIÊN HỆ KIẾN TRÚC SƯ - KỸ SƯ THIẾT KẾ ĐỂ CÓ TƯ VẤN KỊP THỜI TRƯỚC KHI KHỞI CÔNG

HỖ TRỢ TƯ VẤN KỸ THUẬT XÂY DỰNG : 0924099999
LIÊN HỆ MUA VẬT LIỆU MAXHOME : 0921845555 (MIỄN PHÍ VẬN CHUYỂN TOÀN QUỐC)

-BÊ TÔNG LÓT MÓNG ĐÁ 4X6, MÁC 100 -BÊ TÔNG MÓNG, MÁC 250	-BÊ TÔNG CỘT, DẦM, SÀN MÁC 250 -LỚP BÊ TÔNG BẢO VỆ SÀN: 15MM	-LỚP BÊ TÔNG BẢO VỆ CỐT THÉP DẦM: 25MM -LỚP BÊ TÔNG BẢO VỆ CỐT THÉP CỘT: 25MM	-THÉP CB240T (ø<10) KÝ HIỆU (ø) CÓ RA=2100KG/CM2 -THÉP CB300V (10=<ø<=20) KÝ HIỆU (ø) CÓ RA=2600KG/CM2	-THÉP CB300V (20<ø) KÝ HIỆU (ø) CÓ RA=2600KG/CM2 -CHIỀU DÀI THÉP NEO TẠI CÁC VỊ TRÍ LẤY BẰNG 30D	-CẮT NỐI UỐN CỐT THÉP THEO TCXDVN 5574-2018. -KHI THI CÔNG CẦN KẾT HỢP BẢN VẼ KIẾN TRÚC

CÔNG TY TNHH DESIGN AND CONSTRUCTION NEW MAXHOME
HÀ NỘI
ĐC : TẦNG 25, TÒA NHÀ VP TTTM CHỢ MƠ
SỐ 459C PHỐ BẠCH MAI, P. BẠCH MAI
THÀNH PHỐ HÀ NỘI
TEL: 0964458888 - 0828133333

Chủ đầu tư:
NGUYỄN THỊ ÁNH NGUYỆT

Địa điểm:
NAM HỒNG - HÀ TĨNH

Tên công trình:
NHÀ Ở GIA ĐÌNH

HỢP ĐỒNG SỐ /HĐ-TK/20.....

CHỦ NHIỆM THIẾT KẾ KTS: NGUYỄN VĂN CƯỜNG	
TRIỂN KHAI KS: HÀNG A LAO	
KIỂM DUYỆT KTS: NGUYỄN TẤT HỘI	


NỘI DUNG ĐIỀU CHỈNH

Lần	Ngày	Duyệt
1	.....	.....
2	.....	.....
3	.....	.....
4	.....	.....
5	.....	.....
6	.....	.....
7	.....	.....

Hạng mục:
KẾT CẤU

Tên bản vẽ:
CHI TIẾT BỂ NƯỚC

	Hà Nội, 12-2025
Phát hành lần 01	Thiết kế
.....	**KC-02-03**

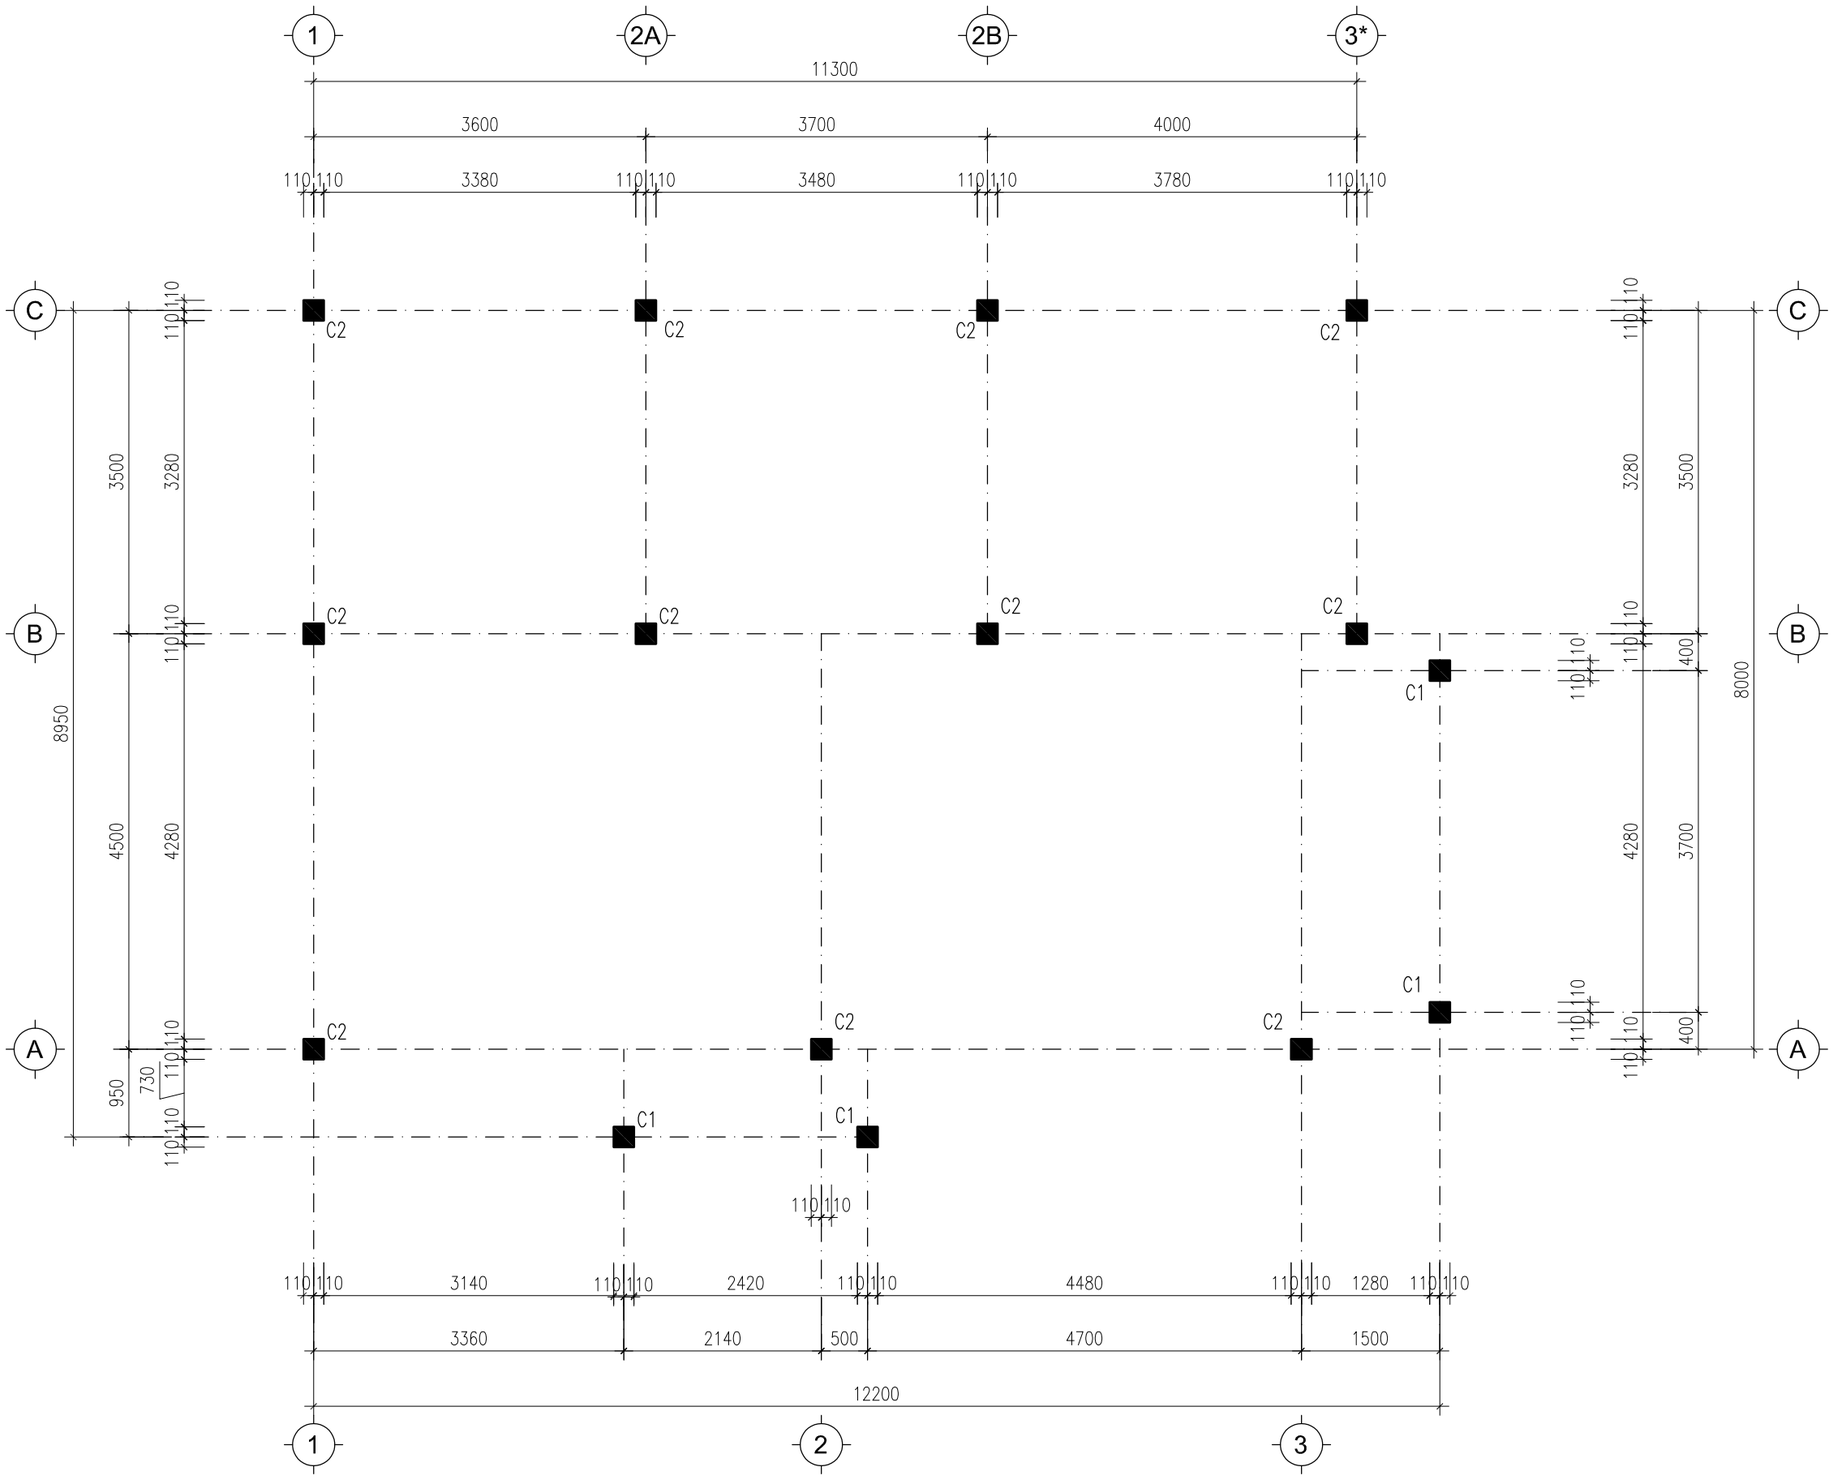

MẶT BẰNG ĐỊNH VỊ CỘT TẦNG 1

CHỦ ĐẦU TƯ CẦN YÊU CẦU KỸ SƯ HIỆN TRƯỜNG KIỂM TRA - RÀ SOÁT BẢN VẼ TRƯỚC KHI THI CÔNG
NẾU CÓ THẮC MẮC VUI LÒNG LIÊN HỆ KIẾN TRÚC SƯ - KỸ SƯ THIẾT KẾ ĐỂ CÓ TƯ VẤN KỊP THỜI TRƯỚC KHI KHỞI CÔNG

HỖ TRỢ TƯ VẤN KỸ THUẬT XÂY DỰNG : 0924099999
LIÊN HỆ MUA VẬT LIỆU MAXHOME : 0921845555 (MIỄN PHÍ VẬN CHUYỂN TOÀN QUỐC)

-BÊ TÔNG LÓT MÓNG ĐÁ 4X6, MÁC 100 -BÊ TÔNG MÓNG, MÁC 250	-BÊ TÔNG CỘT, DẦM, SÀN MÁC 250 -LỚP BÊ TÔNG BẢO VỆ SÀN: 15MM	-LỚP BÊ TÔNG BẢO VỆ CỐT THÉP DẦM: 25MM -LỚP BÊ TÔNG BẢO VỆ CỐT THÉP CỘT: 25MM	-THÉP CB240T (ø<10) KÝ HIỆU (ø) CÓ RA=2100KG/CM2 -THÉP CB300V (10=<ø<=20) KÝ HIỆU (ø) CÓ RA=2600KG/CM2	-THÉP CB300V (20<ø) KÝ HIỆU (ø) CÓ RA=2600KG/CM2 -CHIỀU DÀI THÉP NEO TẠI CÁC VỊ TRÍ LẤY BẰNG 30D	-CẮT NỐI UỐN CỐT THÉP THEO TCXDVN 5574-2018. -KHI THI CÔNG CẦN KẾT HỢP BẢN VẼ KIẾN TRÚC

CÔNG TY TNHH DESIGN AND CONSTRUCTION NEW MAXHOME
HÀ NỘI
ĐC : TẦNG 25, TÒA NHÀ VP TTTM CHỢ MƠ
SỐ 459C PHỐ BẠCH MAI, P. BẠCH MAI
THÀNH PHỐ HÀ NỘI
TEL: 0964458888 - 0828133333

MAXHOME

Chủ đầu tư:

NGUYỄN THỊ ÁNH NGUYỆT

Địa điểm:

NAM HỒNG - HÀ TĨNH

Tên công trình:

NHÀ Ở GIA ĐÌNH

HỢP ĐỒNG SỐ /HĐ-TK/20.....

CHỦ NHIỆM THIẾT KẾ KTS: NGUYỄN VĂN CƯỜNG	
TRIỂN KHAI KS: HÀNG A LAO	
KIỂM DUYỆT KTS: NGUYỄN TẤT HỘI	

NỘI DUNG ĐIỀU CHỈNH

Lần	Ngày	Duyệt
1	.....	.....
2	.....	.....
3	.....	.....
4	.....	.....
5	.....	.....
6	.....	.....
7	.....	.....


Hạng mục:

KẾT CẤU

Tên bản vẽ:


MBDV CỘT TẦNG 1

	Hà Nội, 12-2025
Phát hành lần 01	Thiết kế
.....	**KC-03-01**

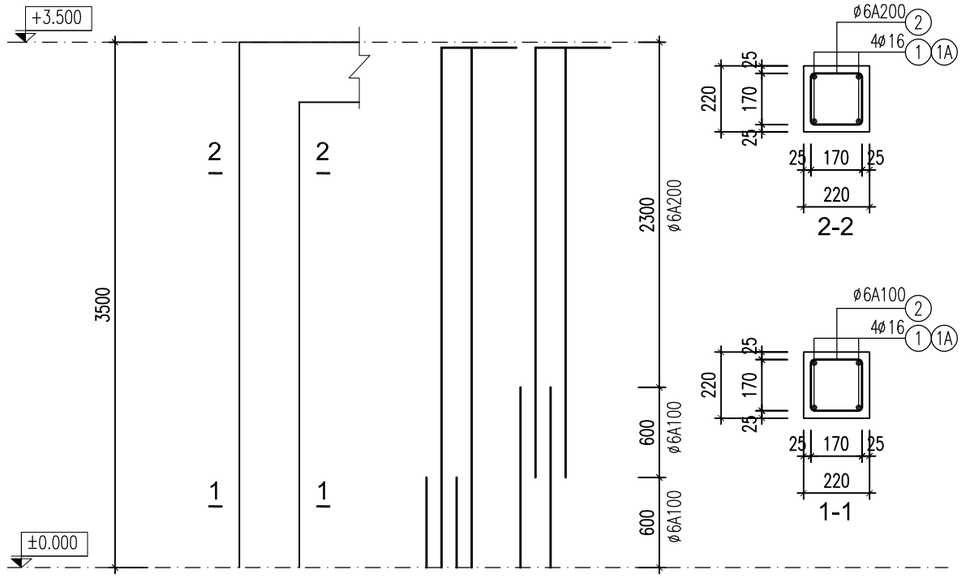

CHI TIẾT CỘT C1

SỐ LƯỢNG: 04

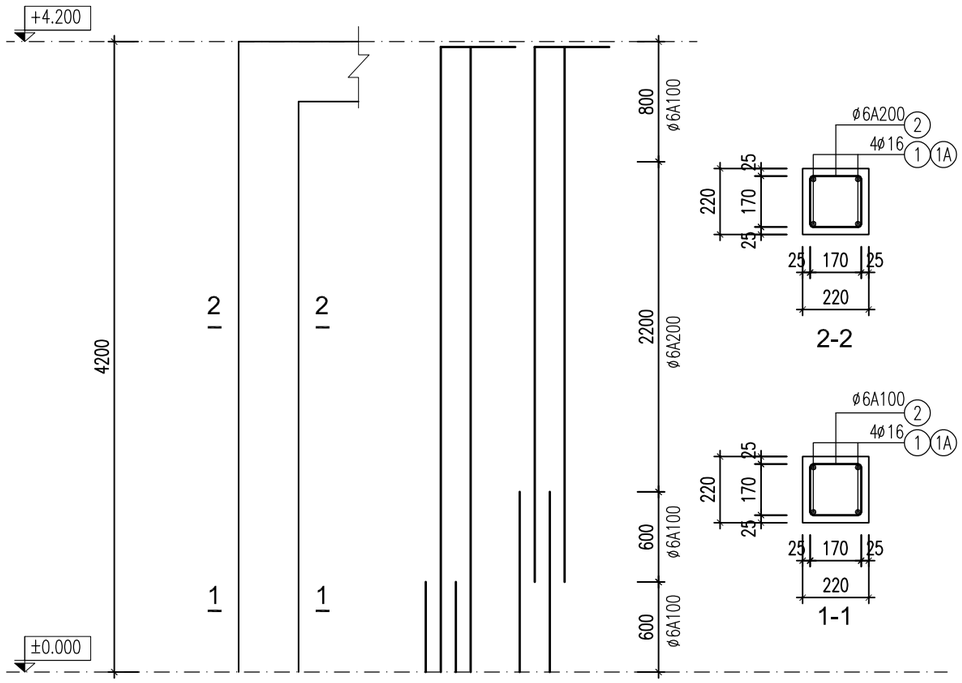

CHI TIẾT CỘT C2

SỐ LƯỢNG: 11

BẢNG THỐNG KÊ CỐT THÉP

TÊN C.KIỆN	SỐ HIỆU	HÌNH DẠNG - KÍCH THƯỚC	ĐƯỜNG KÍNH (mm)	CHIỀU DÀI 1 THANH (mm)	SỐ LƯỢNG		TỔNG CHIỀU DÀI (m)	TỔNG T.LƯỢNG (Kg)
					1 C.KIỆN	T.BỘ		
C1 Số lượng: 4	1	300 \ 3450	16	3750	2	8	30	47.35
	1A	300 \ 2850	16	3150	2	8	25.2	39.77
	2	170 \ 170 \ 50	6	780	23	92	71.76	15.93
C2 Số lượng: 11	1	300 \ 4150	16	4450	2	22	97.9	154.52
	1A	300 \ 3550	16	3850	2	22	84.7	133.69
	2	170 \ 170 \ 50	6	780	30	330	257.4	57.13

- Trọng lượng thép có đường kính Φ6 = 73.06 kg; Chiều dài = 329.16 mét
- Trọng lượng thép có đường kính Φ16 = 375.33 kg; Chiều dài = 237.8 mét

CHỦ ĐẦU TƯ CẦN YÊU CẦU KỸ SƯ HIỆN TRƯỜNG KIỂM TRA - RÀ SOÁT BẢN VẼ TRƯỚC KHI THI CÔNG
NẾU CÓ THẮC MẮC VUI LÒNG LIÊN HỆ KIẾN TRÚC SƯ - KỸ SƯ THIẾT KẾ ĐỂ CÓ TƯ VẤN KỊP THỜI TRƯỚC KHI KHỞI CÔNG

HỖ TRỢ TƯ VẤN KỸ THUẬT XÂY DỰNG : 0924099999
LIÊN HỆ MUA VẬT LIỆU MAXHOME : 0921845555 (MIỄN PHÍ VẬN CHUYỂN TOÀN QUỐC)

-BÊ TÔNG LÓT MÓNG ĐÁ 4X6, MÁC 100 -BÊ TÔNG MÓNG, MÁC 250	-BÊ TÔNG CỘT, DẦM, SÀN MÁC 250 -LỚP BÊ TÔNG BẢO VỆ SÀN: 15MM	-LỚP BÊ TÔNG BẢO VỆ CỐT THÉP DẦM: 25MM -LỚP BÊ TÔNG BẢO VỆ CỐT THÉP CỘT: 25MM	-THÉP CB240T (ϕ<10) KÝ HIỆU (ϕ) CÓ RA=2100KG/CM2 -THÉP CB300V (10=<ϕ<=20) KÝ HIỆU (ϕ) CÓ RA=2600KG/CM2	-THÉP CB300V (20<ϕ) KÝ HIỆU (ϕ) CÓ RA=2600KG/CM2 -CHIỀU DÀI THÉP NEO TẠI CÁC VỊ TRÍ LẤY BẰNG 30D	-CẮT NỐI UỐN CỐT THÉP THEO TCXDVN 5574-2018. -KHI THI CÔNG CẦN KẾT HỢP BẢN VẼ KIẾN TRÚC

CÔNG TY TNHH DESIGN AND CONSTRUCTION NEW MAXHOME
HÀ NỘI
ĐC : TẦNG 25, TÒA NHÀ VP TTTM CHỢ MƠ
SỐ 459C PHỐ BẠCH MAI, P. BẠCH MAI
THÀNH PHỐ HÀ NỘI
TEL: 0964458888 - 0828133333

Chủ đầu tư:

NGUYỄN THỊ ÁNH NGUYỆT

Địa điểm:

NAM HỒNG - HÀ TĨNH

Tên công trình:

NHÀ Ở GIA ĐÌNH

HỢP ĐỒNG SỐ /HĐ-TK/20.....

CHỦ NHIỆM THIẾT KẾ	
KTS: NGUYỄN VĂN CƯỜNG	
TRIỂN KHAI	
KS: HÀNG A LAO	
KIỂM DUYỆT	
KTS: NGUYỄN TẤT HỘI	

NỘI DUNG ĐIỀU CHỈNH

Lần	Ngày	Duyệt
1	.....	.....
2	.....	.....
3	.....	.....
4	.....	.....
5	.....	.....
6	.....	.....
7	.....	.....


Hạng mục:

KẾT CẤU

Tên bản vẽ:

CHI TIẾT CỘT

	Hà Nội, 12-2025
Phát hành lần 01	Thiết kế
.....	**KC-03-02**

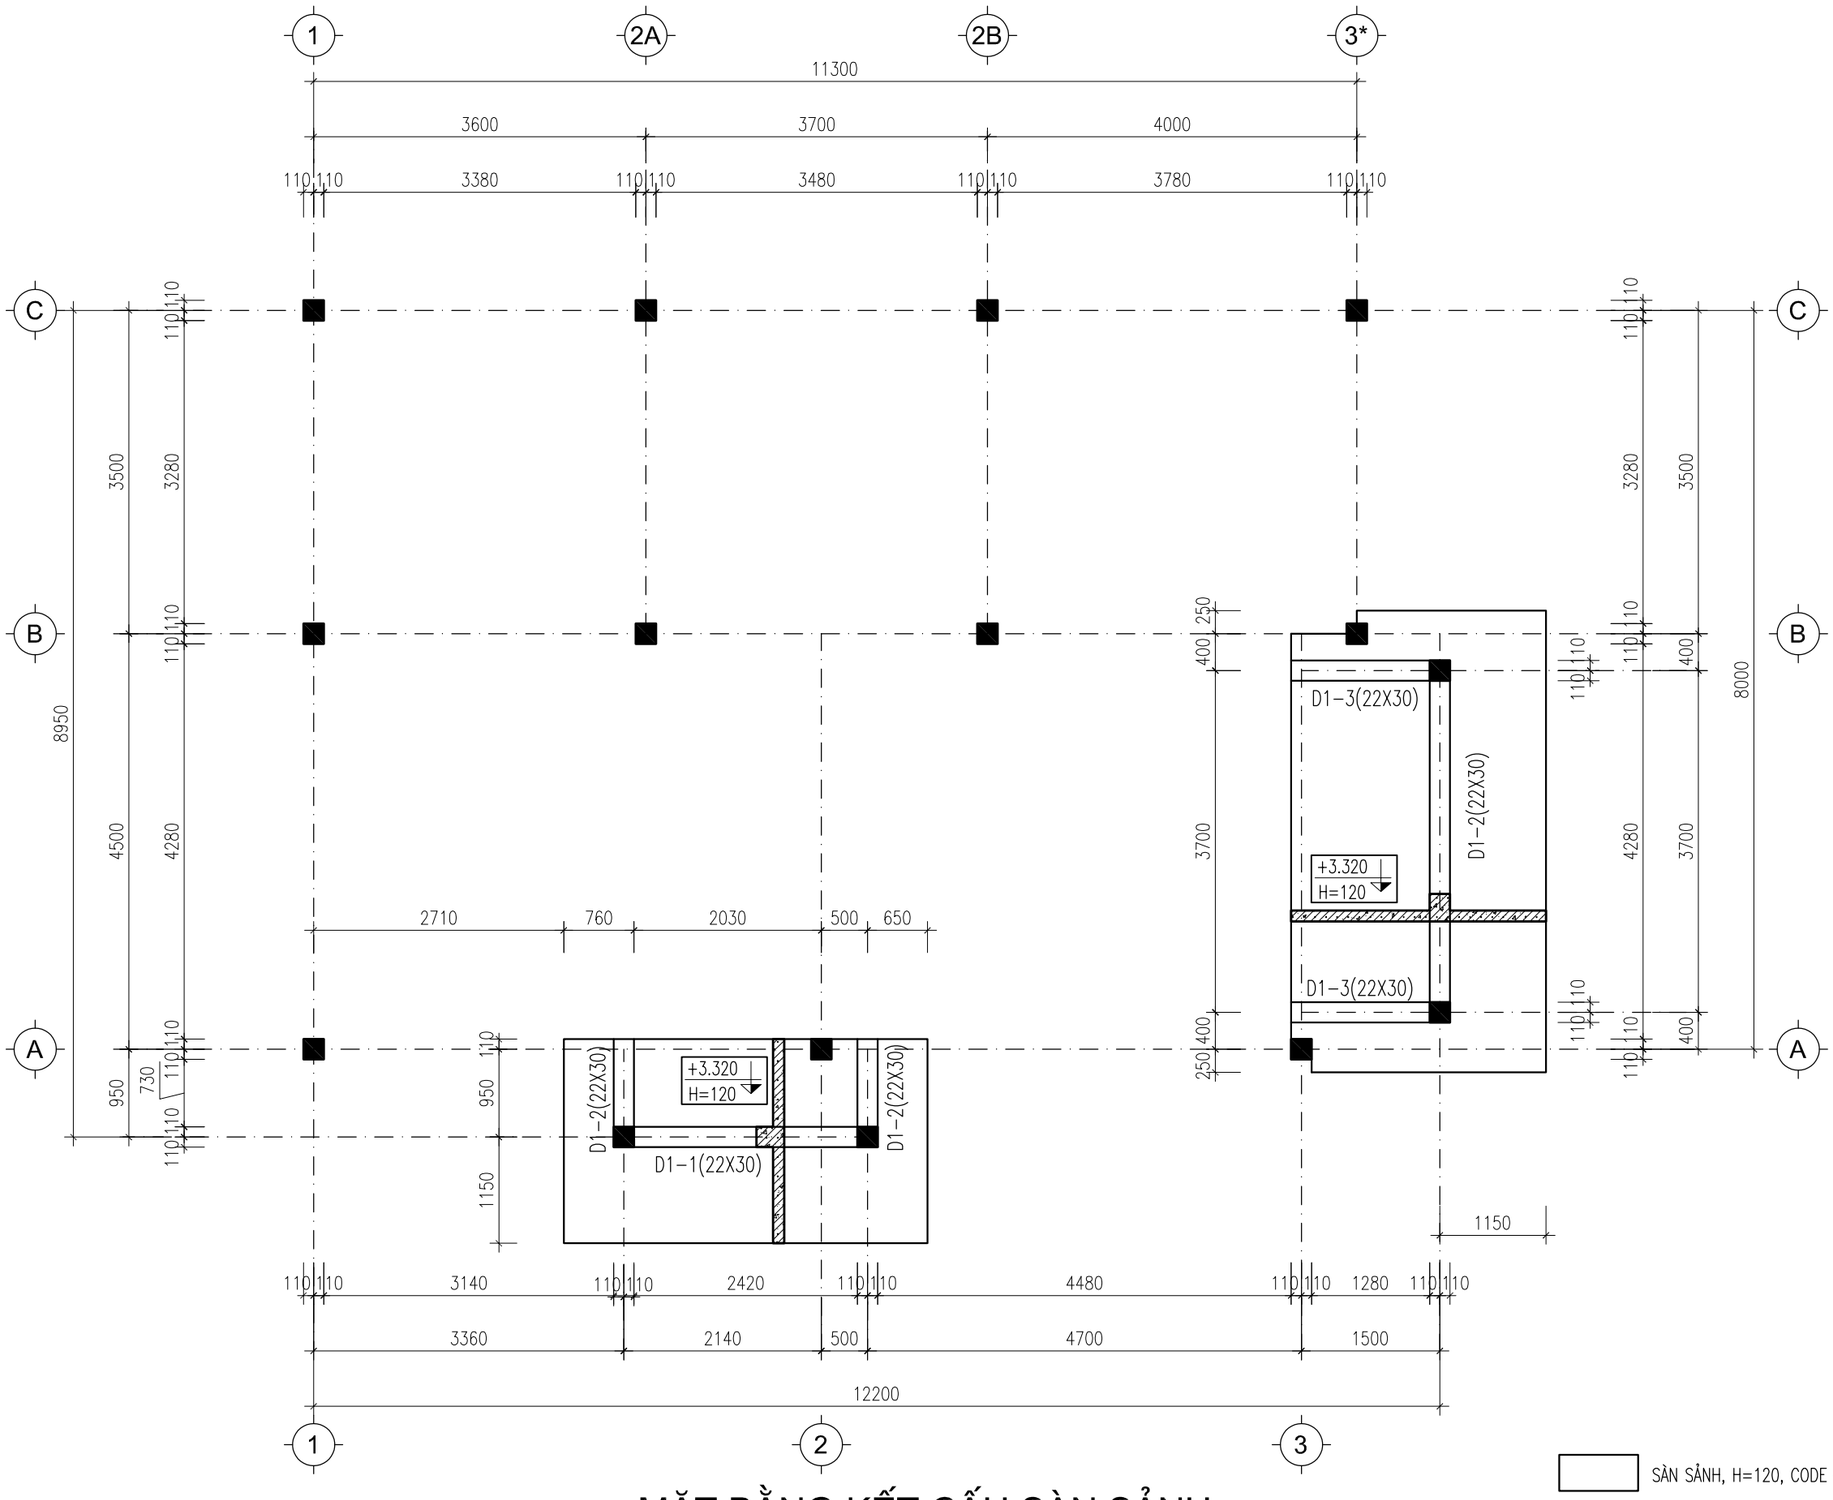

MẶT BẰNG KẾT CẤU SÀN SẢNH

CHỦ ĐẦU TƯ CẦN YÊU CẦU KỸ SƯ HIỆN TRƯỜNG KIỂM TRA - RÀ SOÁT BẢN VẼ TRƯỚC KHI THI CÔNG
NẾU CÓ THẮC MẮC VUI LÒNG LIÊN HỆ KIẾN TRÚC SƯ - KỸ SƯ THIẾT KẾ ĐỂ CÓ TƯ VẤN KỊP THỜI TRƯỚC KHI KHỞI CÔNG

HỖ TRỢ TƯ VẤN KỸ THUẬT XÂY DỰNG : 0924099999
LIÊN HỆ MUA VẬT LIỆU MAXHOME : 0921845555 (MIỄN PHÍ VẬN CHUYỂN TOÀN QUỐC)

-BÊ TÔNG LÓT MÓNG ĐÁ 4X6, MÁC 100 -BÊ TÔNG MÓNG, MÁC 250	-BÊ TÔNG CỘT, DẦM, SÀN MÁC 250 -LỚP BÊ TÔNG BẢO VỆ SÀN: 15MM	-LỚP BÊ TÔNG BẢO VỆ CỐT THÉP DẦM: 25MM -LỚP BÊ TÔNG BẢO VỆ CỐT THÉP CỘT: 25MM	-THÉP CB240T (ø<10) KÝ HIỆU (ø) CÓ RA=2100KG/CM2 -THÉP CB300V (10=<ø<=20) KÝ HIỆU (ø) CÓ RA=2600KG/CM2	-THÉP CB300V (20<ø) KÝ HIỆU (ø) CÓ RA=2600KG/CM2 -CHIỀU DÀI THÉP NEO TẠI CÁC VỊ TRÍ LẤY BẰNG 30D	-CẮT NỐI UỐN CỐT THÉP THEO TCXDVN 5574-2018. -KHI THI CÔNG CẦN KẾT HỢP BẢN VẼ KIẾN TRÚC

CÔNG TY TNHH DESIGN AND CONSTRUCTION NEW MAXHOME
HÀ NỘI
ĐC : TẦNG 25, TÒA NHÀ VP TTTM CHỢ MƠ
SỐ 459C PHỐ BẠCH MAI, P. BẠCH MAI
THÀNH PHỐ HÀ NỘI
TEL: 0964458888 - 0828133333

Chủ đầu tư:

NGUYỄN THỊ ÁNH NGUYỆT

Địa điểm:

NAM HỒNG - HÀ TĨNH

Tên công trình:

NHÀ Ở GIA ĐÌNH

HỢP ĐỒNG SỐ /HĐ-TK/20.....

CHỦ NHIỆM THIẾT KẾ KTS: NGUYỄN VĂN CƯỜNG	
TRIỂN KHAI KS: HÀNG A LAO	
KIỂM DUYỆT KTS: NGUYỄN TẤT HỘI	

NỘI DUNG ĐIỀU CHỈNH

Lần	Ngày	Duyệt
1	.....	.....
2	.....	.....
3	.....	.....
4	.....	.....
5	.....	.....
6	.....	.....
7	.....	.....


Hạng mục:

KẾT CẤU

Tên bản vẽ:

MBKC SÀN SẢNH

	Hà Nội, 12-2025
Phát hành lần 01	Thiết kế
.....	**KC-04-01**

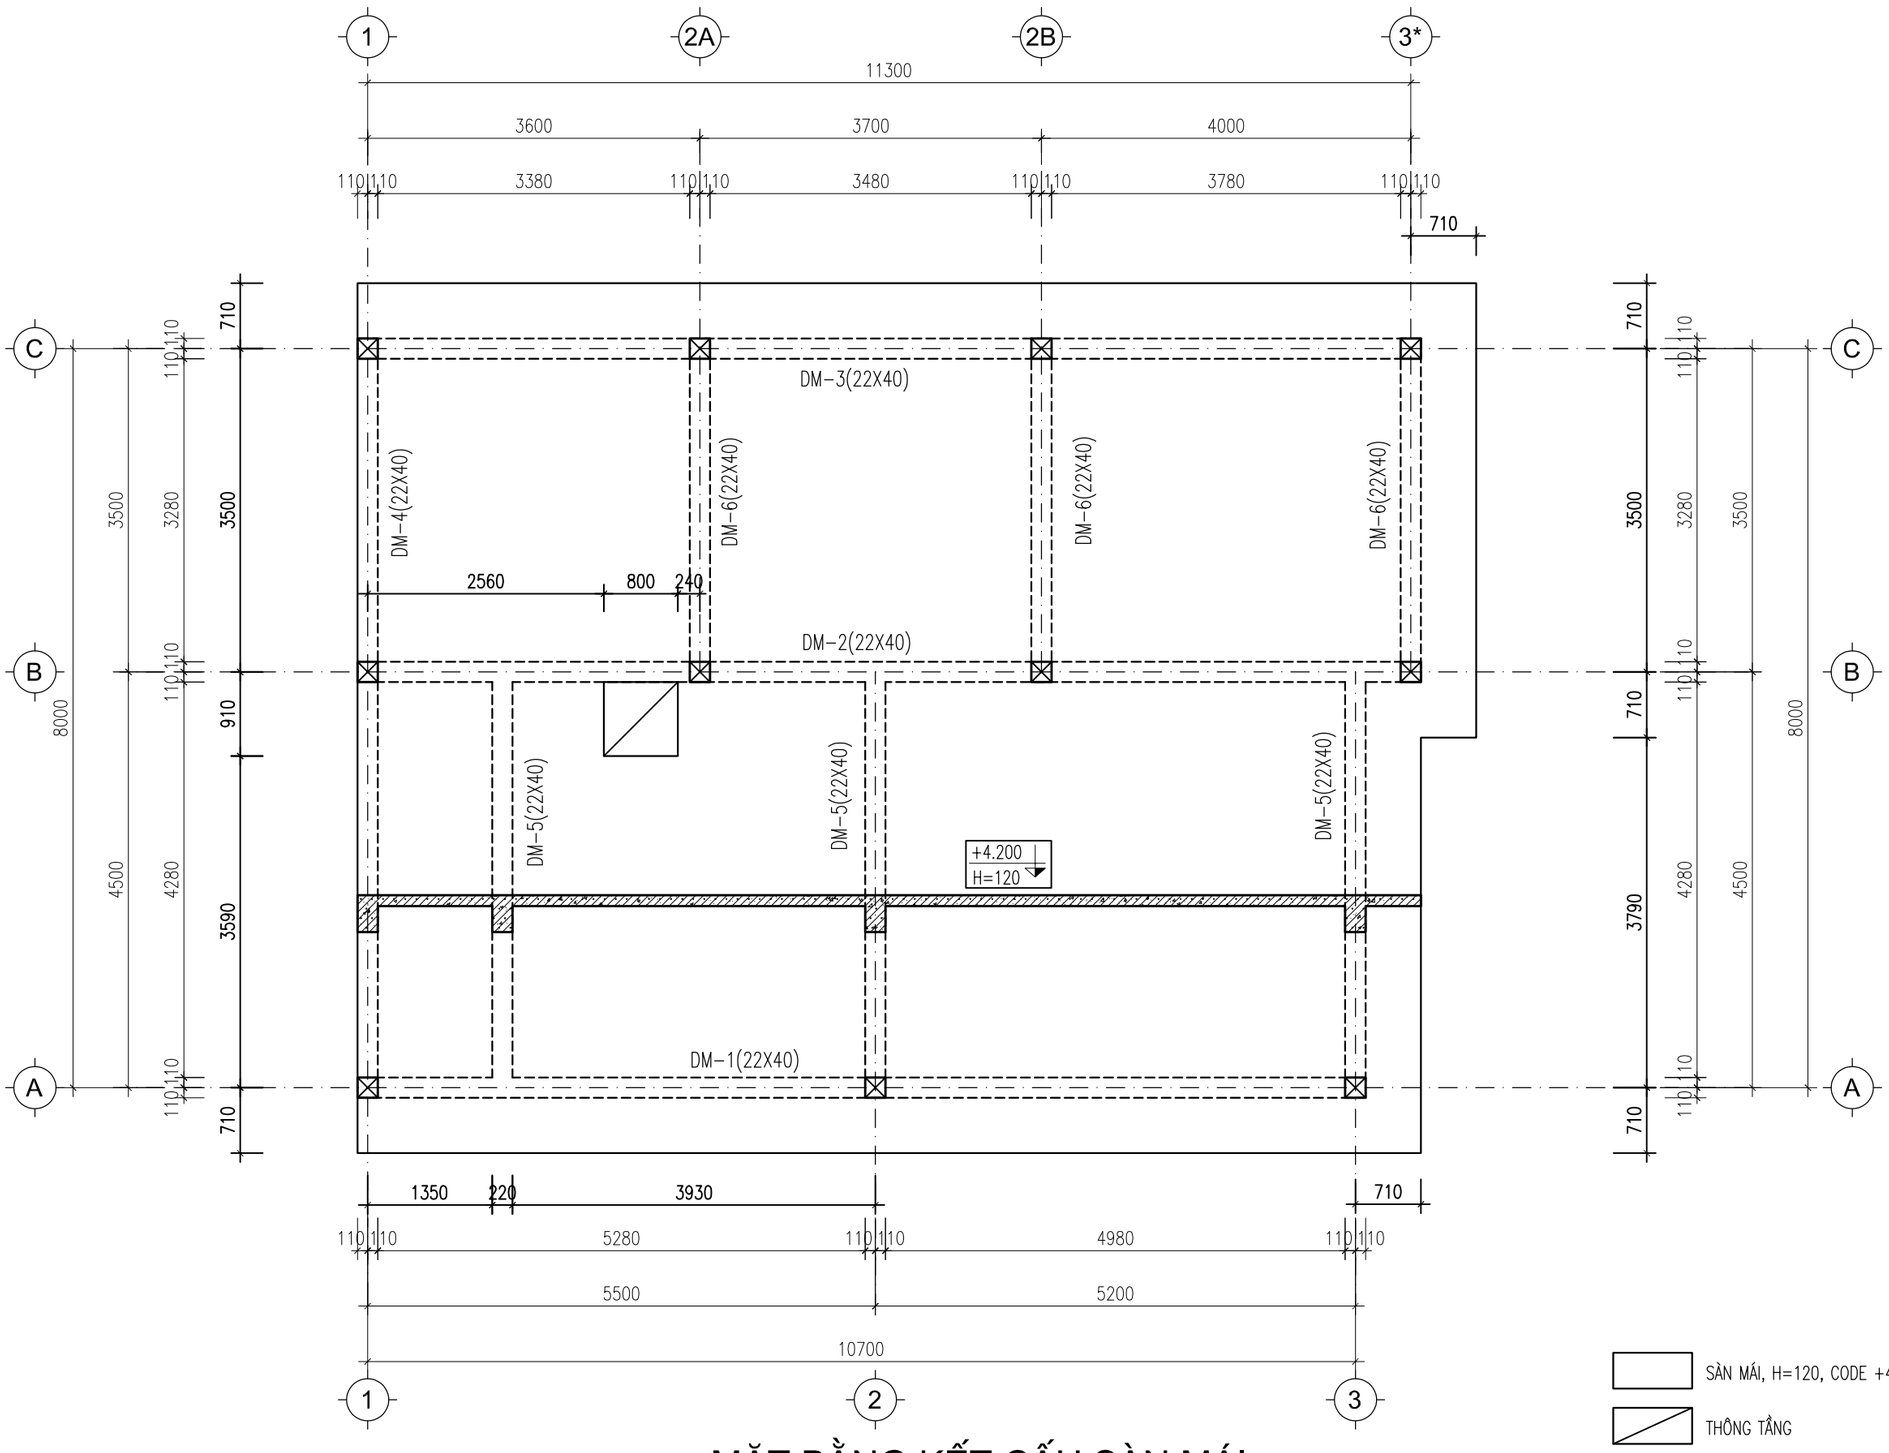

MẶT BẰNG KẾT CẤU SÀN MÁI

CHỦ ĐẦU TƯ CẦN YÊU CẦU KỸ SƯ HIỆN TRƯỜNG KIỂM TRA - RÀ SOÁT BẢN VẼ TRƯỚC KHI THI CÔNG
NẾU CÓ THẮC MẮC VUI LÒNG LIÊN HỆ KIẾN TRÚC SƯ - KỸ SƯ THIẾT KẾ ĐỂ CÓ TƯ VẤN KỊP THỜI TRƯỚC KHI KHỞI CÔNG

HỖ TRỢ TƯ VẤN KỸ THUẬT XÂY DỰNG : 0924099999
LIÊN HỆ MUA VẬT LIỆU MAXHOME : 0921845555 (MIỄN PHÍ VẬN CHUYỂN TOÀN QUỐC)

-BÊ TÔNG LÓT MÓNG ĐÁ 4X6, MÁC 100 -BÊ TÔNG MÓNG, MÁC 250	-BÊ TÔNG CỘT, DẦM, SÀN MÁC 250 -LỚP BÊ TÔNG BẢO VỆ SÀN: 15MM	-LỚP BÊ TÔNG BẢO VỆ CỐT THÉP DẦM: 25MM -LỚP BÊ TÔNG BẢO VỆ CỐT THÉP CỘT: 25MM	-THÉP CB240T (ø<10) KÝ HIỆU (ø) CÓ RA=2100KG/CM2 -THÉP CB300V (10=<ø<=20) KÝ HIỆU (ø) CÓ RA=2600KG/CM2	-THÉP CB300V (20<ø) KÝ HIỆU (ø) CÓ RA=2600KG/CM2 -CHIỀU DÀI THÉP NEO TẠI CÁC VỊ TRÍ LẤY BẰNG 30D	-CẮT NỐI UỐN CỐT THÉP THEO TCXDVN 5574-2018. -KHI THI CÔNG CẦN KẾT HỢP BẢN VẼ KIẾN TRÚC

CÔNG TY TNHH DESIGN AND CONSTRUCTION NEW MAXHOME
HÀ NỘI
ĐC : TẦNG 25, TÒA NHÀ VP TTTM CHỢ MƠ
SỐ 459C PHỐ BẠCH MAI, P. BẠCH MAI
THÀNH PHỐ HÀ NỘI
TEL: 0964458888 - 0828133333

Chủ đầu tư:

NGUYỄN THỊ ÁNH NGUYỆT

Địa điểm:

NAM HỒNG - HÀ TĨNH

Tên công trình:

NHÀ Ở GIA ĐÌNH

HỢP ĐỒNG SỐ /HĐ-TK/20.....

CHỦ NHIỆM THIẾT KẾ KTS: NGUYỄN VĂN CƯỜNG	
TRIỂN KHAI KS: HÀNG A LAO	
KIỂM DUYỆT KTS: NGUYỄN TẤT HỘI	

NỘI DUNG ĐIỀU CHỈNH

Lần	Ngày	Duyệt
1	.....	.....
2	.....	.....
3	.....	.....
4	.....	.....
5	.....	.....
6	.....	.....
7	.....	.....


Hạng mục:

KẾT CẤU

Tên bản vẽ:


MBKC SÀN MÁI

	Hà Nội, 12-2025
Phát hành lần 01	Thiết kế
.....	**KC-04-02**

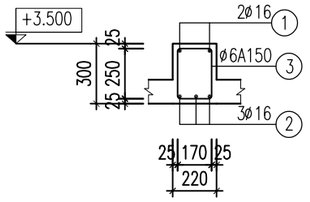


D1-1(22X30)

SL:1; L=2860MM

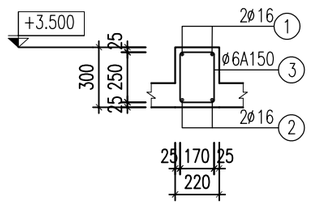


D1-2(22X30)

SL:2; L=1170MM

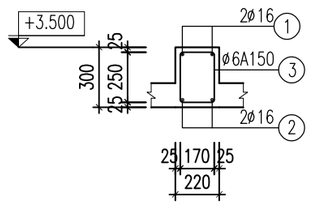


D1-3(22X30)

SL:2; L=1720MM

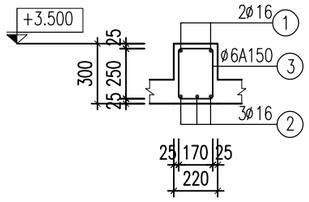


D1-4(22X30)

SL:1; L=3920MM

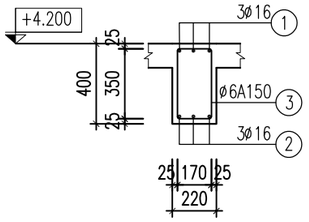


DM-2(22X40)

SL:1; L=11520MM

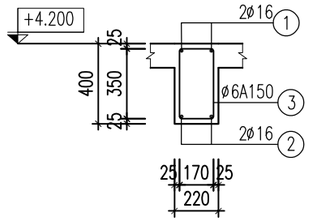


DM-3(22X40)

SL:1; L=11520MM

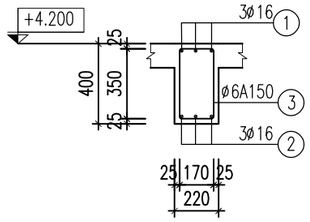


DM-4(22X40)

SL:1; L=8220MM

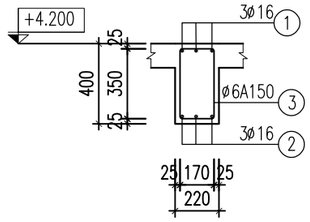


DM-5(22X40)

SL:3; L=4720MM

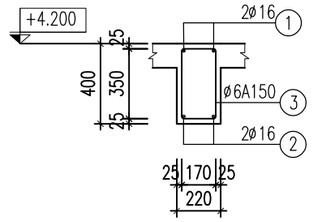


DM-6(22X40)

SL:3; L=3720MM

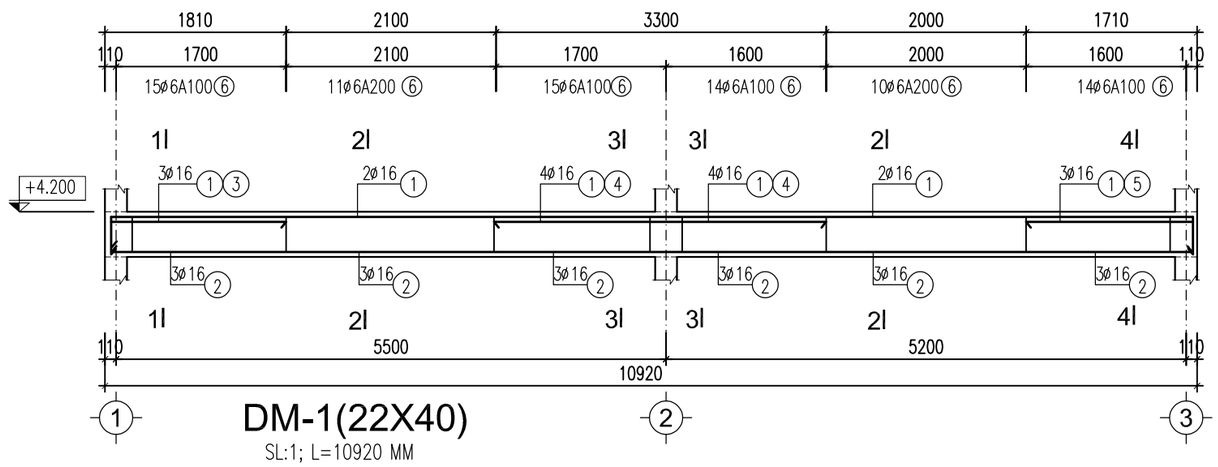


DM-1(22X40)


SL:1; L=10920 MM

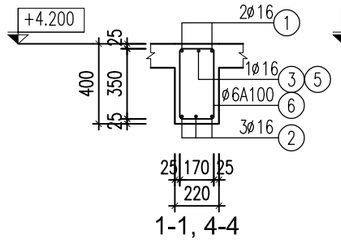

1-1, 4-4

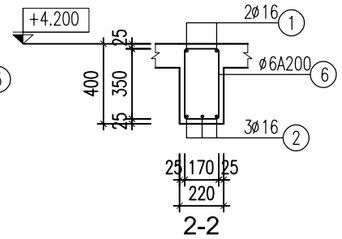

2-2

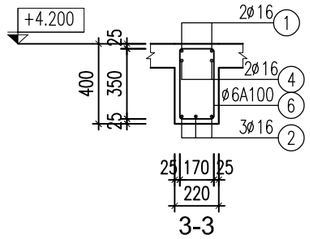

3-3

CHỦ ĐẦU TƯ CẦN YÊU CẦU KỸ SƯ HIỆN TRƯỜNG KIỂM TRA - RÀ SOÁT BẢN VẼ TRƯỚC KHI THI CÔNG
NẾU CÓ THẮC MẮC VUI LÒNG LIÊN HỆ KIẾN TRÚC SƯ - KỸ SƯ THIẾT KẾ ĐỂ CÓ TƯ VẤN KỊP THỜI TRƯỚC KHI KHỞI CÔNG

HỖ TRỢ TƯ VẤN KỸ THUẬT XÂY DỰNG : 0924099999
LIÊN HỆ MUA VẬT LIỆU MAXHOME : 0921845555 (MIỄN PHÍ VẬN CHUYỂN TOÀN QUỐC)

-BÊ TÔNG LÓT MÓNG ĐÁ 4X6, MÁC 100 -BÊ TÔNG MÓNG, MÁC 250	-BÊ TÔNG CỘT, DẦM, SÀN MÁC 250 -LỚP BÊ TÔNG BẢO VỆ SÀN: 15MM	-LỚP BÊ TÔNG BẢO VỆ CỐT THÉP DẦM: 25MM -LỚP BÊ TÔNG BẢO VỆ CỐT THÉP CỘT: 25MM	-THÉP CB240T (ø<10) KÝ HIỆU (ø) CÓ RA=2100KG/CM2 -THÉP CB300V (10=<ø<=20) KÝ HIỆU (ø) CÓ RA=2600KG/CM2	-THÉP CB300V (20<ø) KÝ HIỆU (ø) CÓ RA=2600KG/CM2 -CHIỀU DÀI THÉP NEO TẠI CÁC VỊ TRÍ LẤY BẰNG 30D	-CẮT NỐI UỐN CỐT THÉP THEO TCXDVN 5574-2018. -KHI THI CÔNG CẦN KẾT HỢP BẢN VẼ KIẾN TRÚC

CÔNG TY TNHH DESIGN AND CONSTRUCTION NEW MAXHOME
HÀ NỘI
ĐC : TẦNG 25, TÒA NHÀ VP TTTM CHỢ MƠ
SỐ 459C PHỐ BẠCH MAI, P. BẠCH MAI
THÀNH PHỐ HÀ NỘI
TEL: 0964458888 - 0828133333

Chủ đầu tư:

NGUYỄN THỊ ÁNH NGUYỆT

Địa điểm:

NAM HỒNG - HÀ TĨNH

Tên công trình:

NHÀ Ở GIA ĐÌNH

HỢP ĐỒNG SỐ /HĐ-TK/20.....

CHỦ NHIỆM THIẾT KẾ KTS: NGUYỄN VĂN CƯỜNG	
TRIỂN KHAI KS: HÀNG A LAO	
KIỂM DUYỆT KTS: NGUYỄN TẤT HỘI	

NỘI DUNG ĐIỀU CHỈNH

Lần	Ngày	Duyệt
1	.....	.....
2	.....	.....
3	.....	.....
4	.....	.....
5	.....	.....
6	.....	.....
7	.....	.....

Hạng mục:

KẾT CẤU

Tên bản vẽ:

CHI TIẾT DẦM

	Hà Nội, 12-2025
Phát hành lần 01	Thiết kế
.....	**KC-04-03**

BẢNG THỐNG KÊ CỐT THÉP

TÊN C.KIỆN	SỐ HIỆU	HÌNH DẠNG - KÍCH THƯỚC	ĐƯỜNG KÍNH (mm)	CHIỀU DÀI 1 THANH (mm)	SỐ LƯỢNG 1 C.KIỆN	SỐ LƯỢNG T.BỘ	TỔNG CHIỀU DÀI (m)	TỔNG T.LƯỢNG (Kg)
D1-1 Số lượng: 1	1	250 | 2800 | 250	16	3300	2	2	6.6	10.42
	2	2800	16	2800	3	3	8.4	13.26
	3	250 | 170 | 50	6	940	17	17	15.98	3.55
D1-2 Số lượng: 2	1	250 | 1100 | 250	16	1600	2	4	6.4	10.10
	2	1100	16	1100	2	4	4.4	6.94
	3	250 | 170 | 50	6	940	7	14	13.16	2.92
D1-3 Số lượng: 2	1	250 | 1650 | 250	16	2150	2	4	8.6	13.57
	2	1650	16	1650	2	4	6.6	10.42
	3	250 | 170 | 50	6	940	10	20	18.8	4.17
D1-4 Số lượng: 1	1	250 | 3850 | 250	16	4350	2	2	8.7	13.73
	2	3850	16	3850	3	3	11.55	18.23
	3	250 | 170 | 50	6	940	25	25	23.5	5.22
DM2 Số lượng: 1	1	350 | 11450 | 350	16	12630	3	3	37.89	59.80
	2	11450	16	11450	3	3	34.35	54.22
	3	350 | 170 | 50	6	1140	76	76	86.64	19.23
DM3 Số lượng: 1	1	350 | 11450 | 350	16	12630	2	2	25.26	39.87
	2	11450	16	11450	2	2	22.9	36.14
	3	350 | 170 | 50	6	1140	76	76	86.64	19.23

BẢNG THỐNG KÊ CỐT THÉP

TÊN C.KIỆN	SỐ HIỆU	HÌNH DẠNG - KÍCH THƯỚC	ĐƯỜNG KÍNH (mm)	CHIỀU DÀI 1 THANH (mm)	SỐ LƯỢNG 1 C.KIỆN	SỐ LƯỢNG T.BỘ	TỔNG CHIỀU DÀI (m)	TỔNG T.LƯỢNG (Kg)
DM4 Số lượng: 1	1	350 | 8150 | 350	16	8850	3	3	26.55	41.90
	2	8150	16	8150	3	3	24.45	38.59
	3	350 | 170 | 50	6	1140	54	54	61.56	13.66
DM5 Số lượng: 3	1	350 | 4650 | 350	16	5350	3	9	48.15	76.00
	2	4650	16	4650	3	9	41.85	66.05
	3	350 | 170 | 50	6	1140	30	90	102.6	22.77
DM6 Số lượng: 3	1	350 | 3650 | 350	16	4350	2	6	26.1	41.19
	2	3650	16	3650	2	6	21.9	34.57
	3	350 | 170 | 50	6	1140	24	72	82.08	18.22
DM1 Số lượng: 1	1	350 | 10850 | 350	16	11550	2	2	23.1	36.46
	2	10850	16	10850	3	3	32.55	51.37
	3	350 | 1800	16	2150	1	1	2.15	3.39
	4	3300	16	3300	2	2	6.6	10.42
	5	350 | 1700	16	2050	1	1	2.05	3.24
	6	350 | 170 | 50	6	1140	79	79	90.06	19.99

- Trọng lượng thép có đường kính Φ6 = 128.96 kg; Chiều dài = 581.02 mét
- Trọng lượng thép có đường kính Φ16 = 689.88 kg; Chiều dài = 437.1 mét

CHỦ ĐẦU TƯ CẦN YÊU CẦU KỸ SƯ HIỆN TRƯỜNG KIỂM TRA - RÀ SOÁT BẢN VẼ TRƯỚC KHI THI CÔNG
NẾU CÓ THẮC MẮC VUI LÒNG LIÊN HỆ KIẾN TRÚC SƯ - KỸ SƯ THIẾT KẾ ĐỂ CÓ TƯ VẤN KỊP THỜI TRƯỚC KHI KHỞI CÔNG

HỖ TRỢ TƯ VẤN KỸ THUẬT XÂY DỰNG : 0924099999
LIÊN HỆ MUA VẬT LIỆU MAXHOME : 0921845555 (MIỄN PHÍ VẬN CHUYỂN TOÀN QUỐC)

- BÊ TÔNG LÓT MÓNG ĐÁ 4X6, MÁC 100
- BÊ TÔNG MÓNG, MÁC 250
- BÊ TÔNG CỘT, DẦM, SÀN MÁC 250
- LỚP BÊ TÔNG BẢO VỆ SÀN: 15MM
- LỚP BÊ TÔNG BẢO VỆ CỐT THÉP DẦM: 25MM
- LỚP BÊ TÔNG BẢO VỆ CỐT THÉP CỘT: 25MM
- THÉP CB240T (ø<10) KÝ HIỆU (ø) CÓ RA=2100KG/CM2
- THÉP CB300V (10=<ø<=20) KÝ HIỆU (ø) CÓ RA=2600KG/CM2
- THÉP CB300V (20<ø) KÝ HIỆU (ø) CÓ RA=2600KG/CM2
- CHIỀU DÀI THÉP NEO TẠI CÁC VỊ TRÍ LẤY BẰNG 30D
- CẮT NỐI UỐN CỐT THÉP THEO TCXDVN 5574-2018.
- KHI THI CÔNG CẦN KẾT HỢP BẢN VẼ KIẾN TRÚC

CÔNG TY TNHH DESIGN AND CONSTRUCTION NEW MAXHOME
HÀ NỘI
ĐC : TẦNG 25, TÒA NHÀ VP TTTM CHỢ MƠ
SỐ 459C PHỐ BẠCH MAI, P. BẠCH MAI
THÀNH PHỐ HÀ NỘI
TEL: 0964458888 - 0828133333

MAXHOME

Chủ đầu tư:
NGUYỄN THỊ ÁNH NGUYỆT

Địa điểm:
NAM HỒNG - HÀ TĨNH

Tên công trình:
NHÀ Ở GIA ĐÌNH

HỢP ĐỒNG SỐ /HĐ-TK/20.....

CHỦ NHIỆM THIẾT KẾ	
KTS: NGUYỄN VĂN CƯỜNG	
TRIỂN KHAI	
KS: HÀNG A LAO	
KIỂM DUYỆT	
KTS: NGUYỄN TẤT HỘI	


NỘI DUNG ĐIỀU CHỈNH

Lần	Ngày	Duyệt
1	.....	.....
2	.....	.....
3	.....	.....
4	.....	.....
5	.....	.....
6	.....	.....
7	.....	.....

Hạng mục:
KẾT CẤU

Tên bản vẽ:
TK THÉP DẦM

	Hà Nội, 12-2025
Phát hành lần 01	Thiết kế
.....	**KC-04-04**

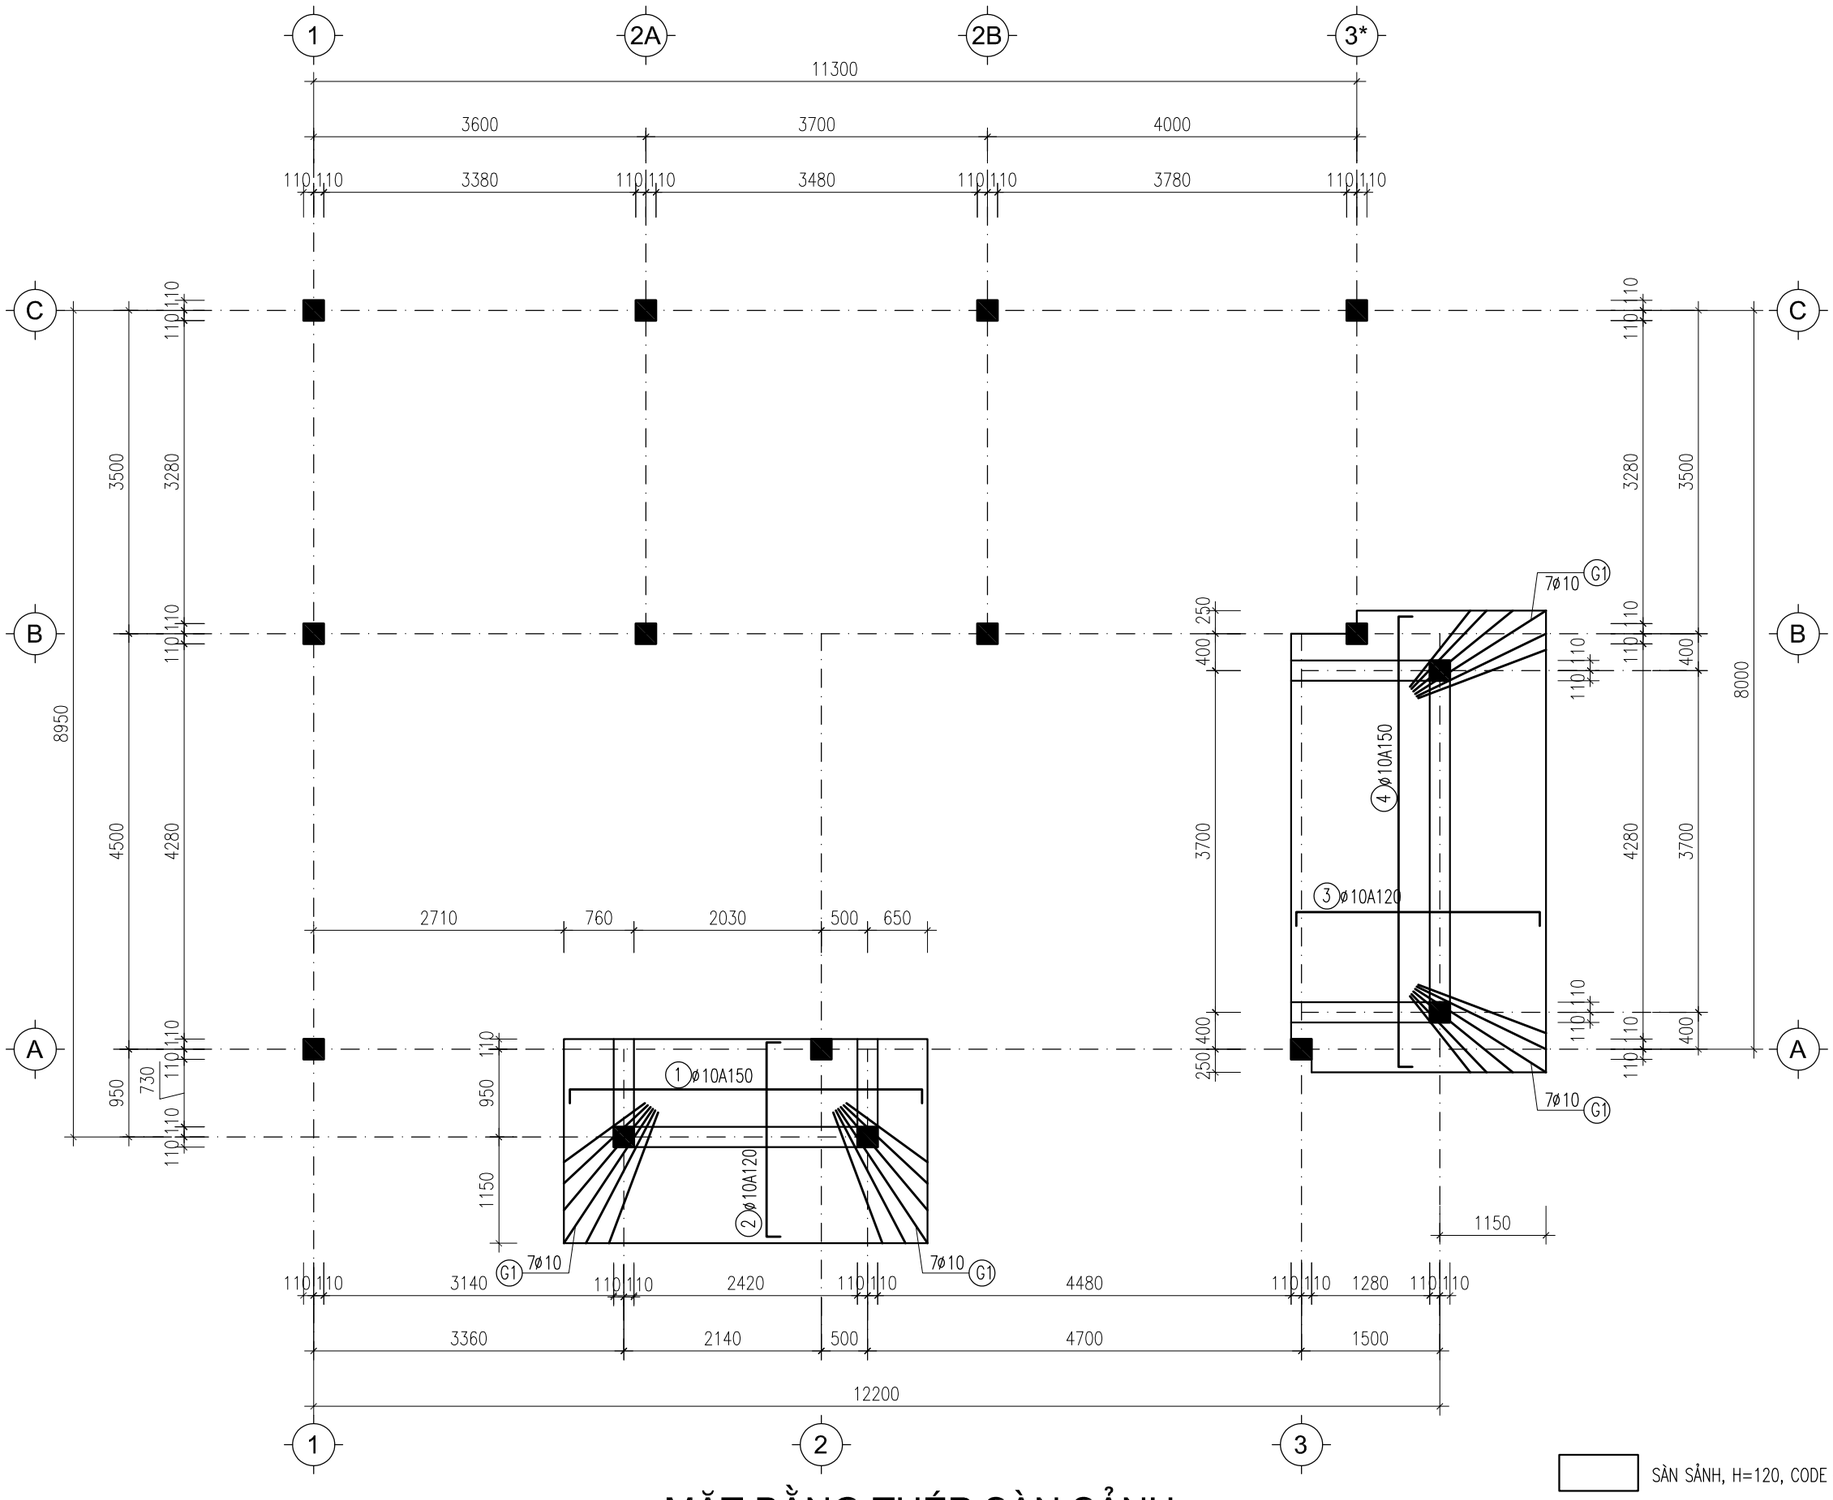

SÀN SẢNH, H=120, CODE +3.320

MẶT BẰNG THÉP SÀN SẢNH

CHỦ ĐẦU TƯ CẦN YÊU CẦU KỸ SƯ HIỆN TRƯỜNG KIỂM TRA - RÀ SOÁT BẢN VẼ TRƯỚC KHI THI CÔNG
NẾU CÓ THẮC MẮC VUI LÒNG LIÊN HỆ KIẾN TRÚC SƯ - KỸ SƯ THIẾT KẾ ĐỂ CÓ TƯ VẤN KỊP THỜI TRƯỚC KHI KHỞI CÔNG

HỖ TRỢ TƯ VẤN KỸ THUẬT XÂY DỰNG : 0924099999
LIÊN HỆ MUA VẬT LIỆU MAXHOME : 0921845555 (MIỄN PHÍ VẬN CHUYỂN TOÀN QUỐC)

-BÊ TÔNG LÓT MÓNG ĐÁ 4X6, MÁC 100 -BÊ TÔNG MÓNG, MÁC 250	-BÊ TÔNG CỘT, DẦM, SÀN MÁC 250 -LỚP BÊ TÔNG BẢO VỆ SÀN: 15MM	-LỚP BÊ TÔNG BẢO VỆ CỐT THÉP DẦM: 25MM -LỚP BÊ TÔNG BẢO VỆ CỐT THÉP CỘT: 25MM	-THÉP CB240T (ø<10) KÝ HIỆU (ø) CÓ RA=2100KG/CM2 -THÉP CB300V (10=<ø<=20) KÝ HIỆU (ø) CÓ RA=2600KG/CM2	-THÉP CB300V (20<ø) KÝ HIỆU (ø) CÓ RA=2600KG/CM2 -CHIỀU DÀI THÉP NEO TẠI CÁC VỊ TRÍ LẤY BẰNG 30D	-CẮT NỐI UỐN CỐT THÉP THEO TCXDVN 5574-2018. -KHI THI CÔNG CẦN KẾT HỢP BẢN VẼ KIẾN TRÚC

CÔNG TY TNHH DESIGN AND CONSTRUCTION NEW MAXHOME
HÀ NỘI
ĐC : TẦNG 25, TÒA NHÀ VP TTTM CHỢ MƠ
SỐ 459C PHỐ BẠCH MAI, P. BẠCH MAI
THÀNH PHỐ HÀ NỘI
TEL: 0964458888 - 0828133333

Chủ đầu tư:

NGUYỄN THỊ ÁNH NGUYỆT

Địa điểm:

NAM HỒNG - HÀ TĨNH

Tên công trình:

NHÀ Ở GIA ĐÌNH

HỢP ĐỒNG SỐ /HĐ-TK/20.....

CHỦ NHIỆM THIẾT KẾ KTS: NGUYỄN VĂN CƯỜNG	
TRIỂN KHAI KS: HÀNG A LAO	
KIỂM DUYỆT KTS: NGUYỄN TẤT HỘI	

NỘI DUNG ĐIỀU CHỈNH

Lần	Ngày	Duyệt
1	.....	.....
2	.....	.....
3	.....	.....
4	.....	.....
5	.....	.....
6	.....	.....
7	.....	.....


Hạng mục:

KẾT CẤU

Tên bản vẽ:

MB THÉP SÀN SẢNH

	Hà Nội, 12-2025
Phát hành lần 01	Thiết kế
.....	**KC-05-01**

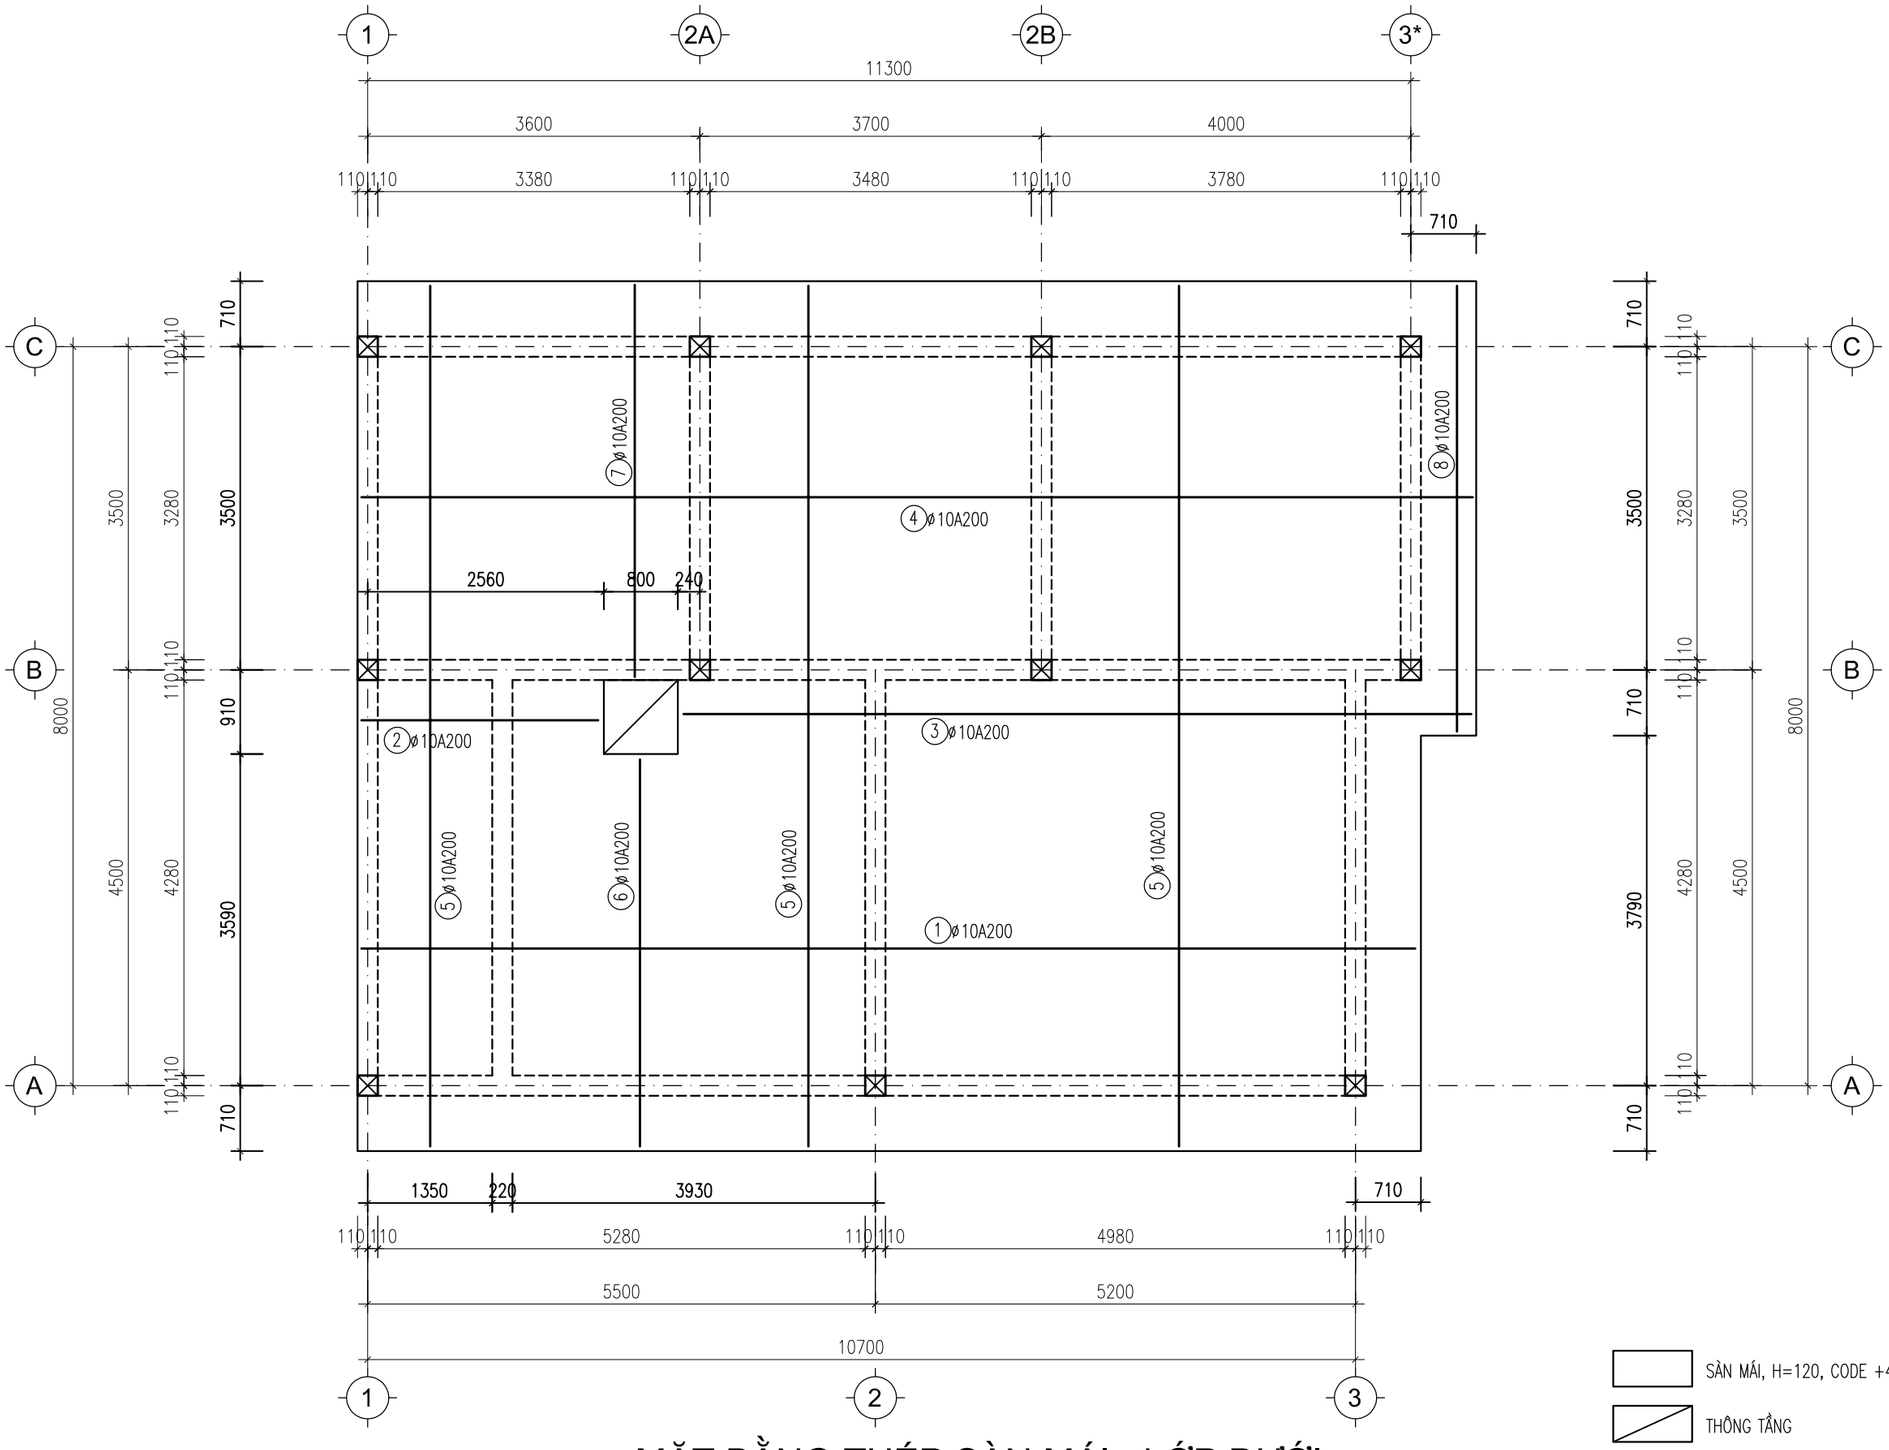

MẶT BẰNG THÉP SÀN MÁI - LỚP DƯỚI

CHỦ ĐẦU TƯ CẦN YÊU CẦU KỸ SƯ HIỆN TRƯỜNG KIỂM TRA - RÀ SOÁT BẢN VẼ TRƯỚC KHI THI CÔNG
NẾU CÓ THẮC MẮC VUI LÒNG LIÊN HỆ KIẾN TRÚC SƯ - KỸ SƯ THIẾT KẾ ĐỂ CÓ TƯ VẤN KỊP THỜI TRƯỚC KHI KHỞI CÔNG

HỖ TRỢ TƯ VẤN KỸ THUẬT XÂY DỰNG : 0924099999
LIÊN HỆ MUA VẬT LIỆU MAXHOME : 0921845555 (MIỄN PHÍ VẬN CHUYỂN TOÀN QUỐC)

-BÊ TÔNG LÓT MÓNG ĐÁ 4X6, MÁC 100 -BÊ TÔNG MÓNG, MÁC 250	-BÊ TÔNG CỘT, DẦM, SÀN MÁC 250 -LỚP BÊ TÔNG BẢO VỆ SÀN: 15MM	-LỚP BÊ TÔNG BẢO VỆ CỐT THÉP DẦM: 25MM -LỚP BÊ TÔNG BẢO VỆ CỐT THÉP CỘT: 25MM	-THÉP CB240T (ø<10) KÝ HIỆU (ø) CÓ RA=2100KG/CM2 -THÉP CB300V (10=<ø<=20) KÝ HIỆU (ø) CÓ RA=2600KG/CM2	-THÉP CB300V (20<ø) KÝ HIỆU (ø) CÓ RA=2600KG/CM2 -CHIỀU DÀI THÉP NEO TẠI CÁC VỊ TRÍ LẤY BẰNG 30D	-CẮT NỐI UỐN CỐT THÉP THEO TCXDVN 5574-2018. -KHI THI CÔNG CẦN KẾT HỢP BẢN VẼ KIẾN TRÚC

CÔNG TY TNHH DESIGN AND CONSTRUCTION NEW MAXHOME
HÀ NỘI
ĐC : TẦNG 25, TÒA NHÀ VP TTTM CHỢ MƠ
SỐ 459C PHỐ BẠCH MAI, P. BẠCH MAI
THÀNH PHỐ HÀ NỘI
TEL: 0964458888 - 0828133333

Chủ đầu tư:

NGUYỄN THỊ ÁNH NGUYỆT

Địa điểm:

NAM HỒNG - HÀ TĨNH

Tên công trình:

NHÀ Ở GIA ĐÌNH

HỢP ĐỒNG SỐ /HĐ-TK/20.....

CHỦ NHIỆM THIẾT KẾ KTS: NGUYỄN VĂN CƯỜNG	
TRIỂN KHAI KS: HÀNG A LAO	
KIỂM DUYỆT KTS: NGUYỄN TẤT HỘI	

NỘI DUNG ĐIỀU CHỈNH

Lần	Ngày	Duyệt
1	.....	.....
2	.....	.....
3	.....	.....
4	.....	.....
5	.....	.....
6	.....	.....
7	.....	.....


Hạng mục:

KẾT CẤU

Tên bản vẽ:

MB THÉP SÀN MÁI

	Hà Nội, 12-2025
Phát hành lần 01	Thiết kế
.....	**KC-05-02**

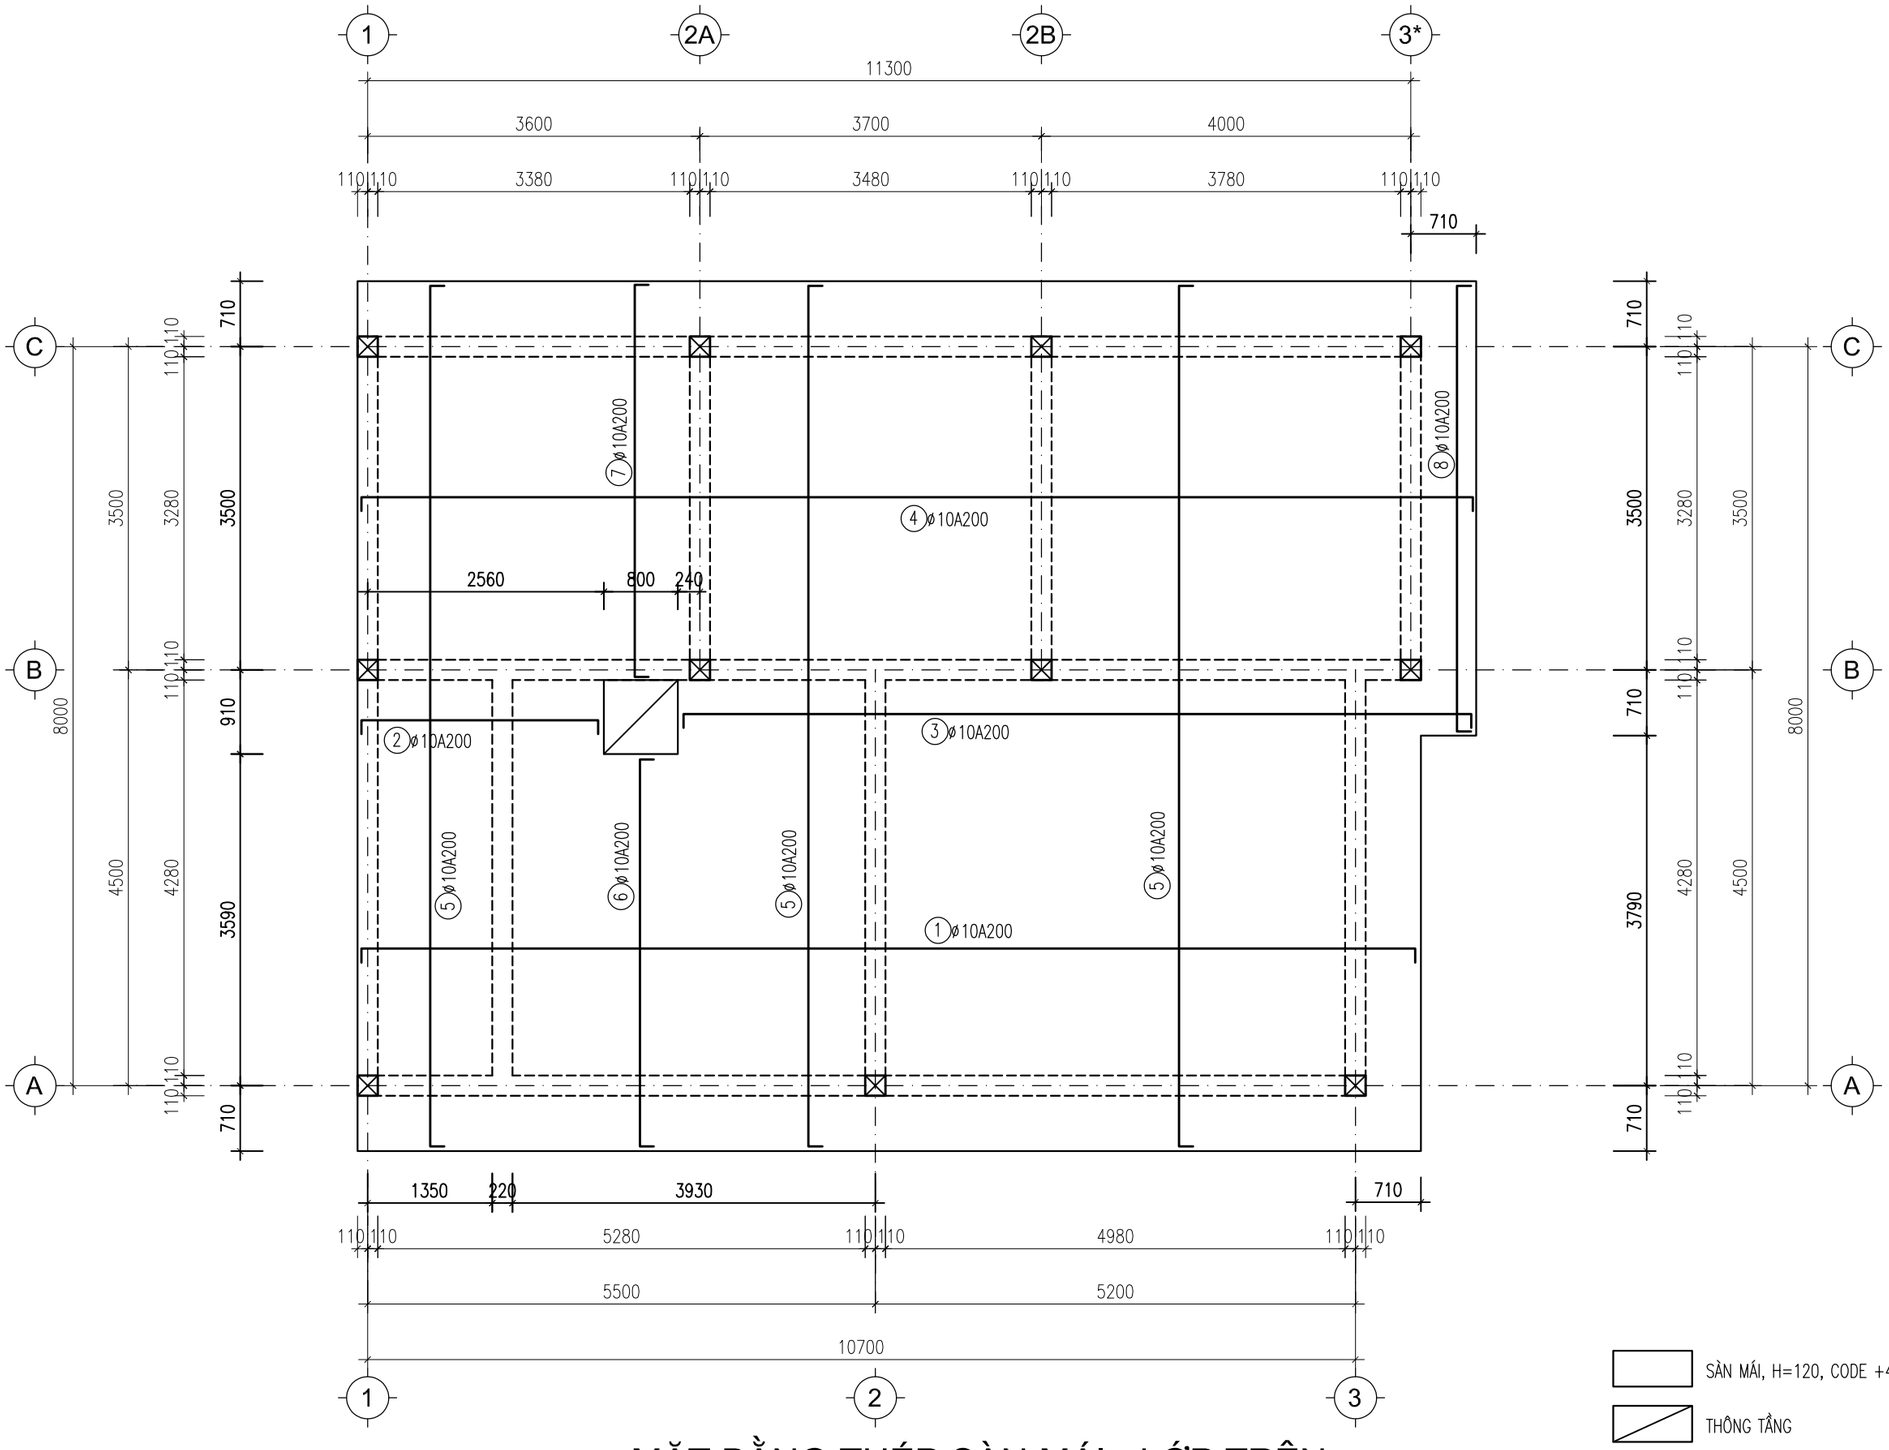

MẶT BẰNG THÉP SÀN MÁI - LỚP TRÊN

CHỦ ĐẦU TƯ CẦN YÊU CẦU KỸ SƯ HIỆN TRƯỜNG KIỂM TRA - RÀ SOÁT BẢN VẼ TRƯỚC KHI THI CÔNG
NẾU CÓ THẮC MẮC VUI LÒNG LIÊN HỆ KIẾN TRÚC SƯ - KỸ SƯ THIẾT KẾ ĐỂ CÓ TƯ VẤN KỊP THỜI TRƯỚC KHI KHỞI CÔNG

HỖ TRỢ TƯ VẤN KỸ THUẬT XÂY DỰNG : 0924099999
LIÊN HỆ MUA VẬT LIỆU MAXHOME : 0921845555 (MIỄN PHÍ VẬN CHUYỂN TOÀN QUỐC)

-BÊ TÔNG LÓT MÓNG ĐÁ 4X6, MÁC 100 -BÊ TÔNG MÓNG, MÁC 250	-BÊ TÔNG CỘT, DẦM, SÀN MÁC 250 -LỚP BÊ TÔNG BẢO VỆ SÀN: 15MM	-LỚP BÊ TÔNG BẢO VỆ CỐT THÉP DẦM: 25MM -LỚP BÊ TÔNG BẢO VỆ CỐT THÉP CỘT: 25MM	-THÉP CB240T (ø<10) KÝ HIỆU (ø) CÓ RA=2100KG/CM2 -THÉP CB300V (10=<ø<=20) KÝ HIỆU (ø) CÓ RA=2600KG/CM2	-THÉP CB300V (20<ø) KÝ HIỆU (ø) CÓ RA=2600KG/CM2 -CHIỀU DÀI THÉP NEO TẠI CÁC VỊ TRÍ LẤY BẰNG 30D	-CẮT NỐI UỐN CỐT THÉP THEO TCXDVN 5574-2018. -KHI THI CÔNG CẦN KẾT HỢP BẢN VẼ KIẾN TRÚC

CÔNG TY TNHH DESIGN AND CONSTRUCTION NEW MAXHOME
HÀ NỘI
ĐC : TẦNG 25, TÒA NHÀ VP TTTM CHỢ MƠ
SỐ 459C PHỐ BẠCH MAI, P. BẠCH MAI
THÀNH PHỐ HÀ NỘI
TEL: 0964458888 - 0828133333

Chủ đầu tư:

NGUYỄN THỊ ÁNH NGUYỆT

Địa điểm:

NAM HỒNG - HÀ TĨNH

Tên công trình:

NHÀ Ở GIA ĐÌNH

HỢP ĐỒNG SỐ /HĐ-TK/20.....

CHỦ NHIỆM THIẾT KẾ KTS: NGUYỄN VĂN CƯỜNG	
TRIỂN KHAI KS: HÀNG A LAO	
KIỂM DUYỆT KTS: NGUYỄN TẤT HỘI	

NỘI DUNG ĐIỀU CHỈNH

Lần	Ngày	Duyệt
1	.....	.....
2	.....	.....
3	.....	.....
4	.....	.....
5	.....	.....
6	.....	.....
7	.....	.....


Hạng mục:

KẾT CẤU

Tên bản vẽ:

MB THÉP SÀN MÁI

	Hà Nội, 12-2025
Phát hành lần 01	Thiết kế
.....	**KC-05-03**

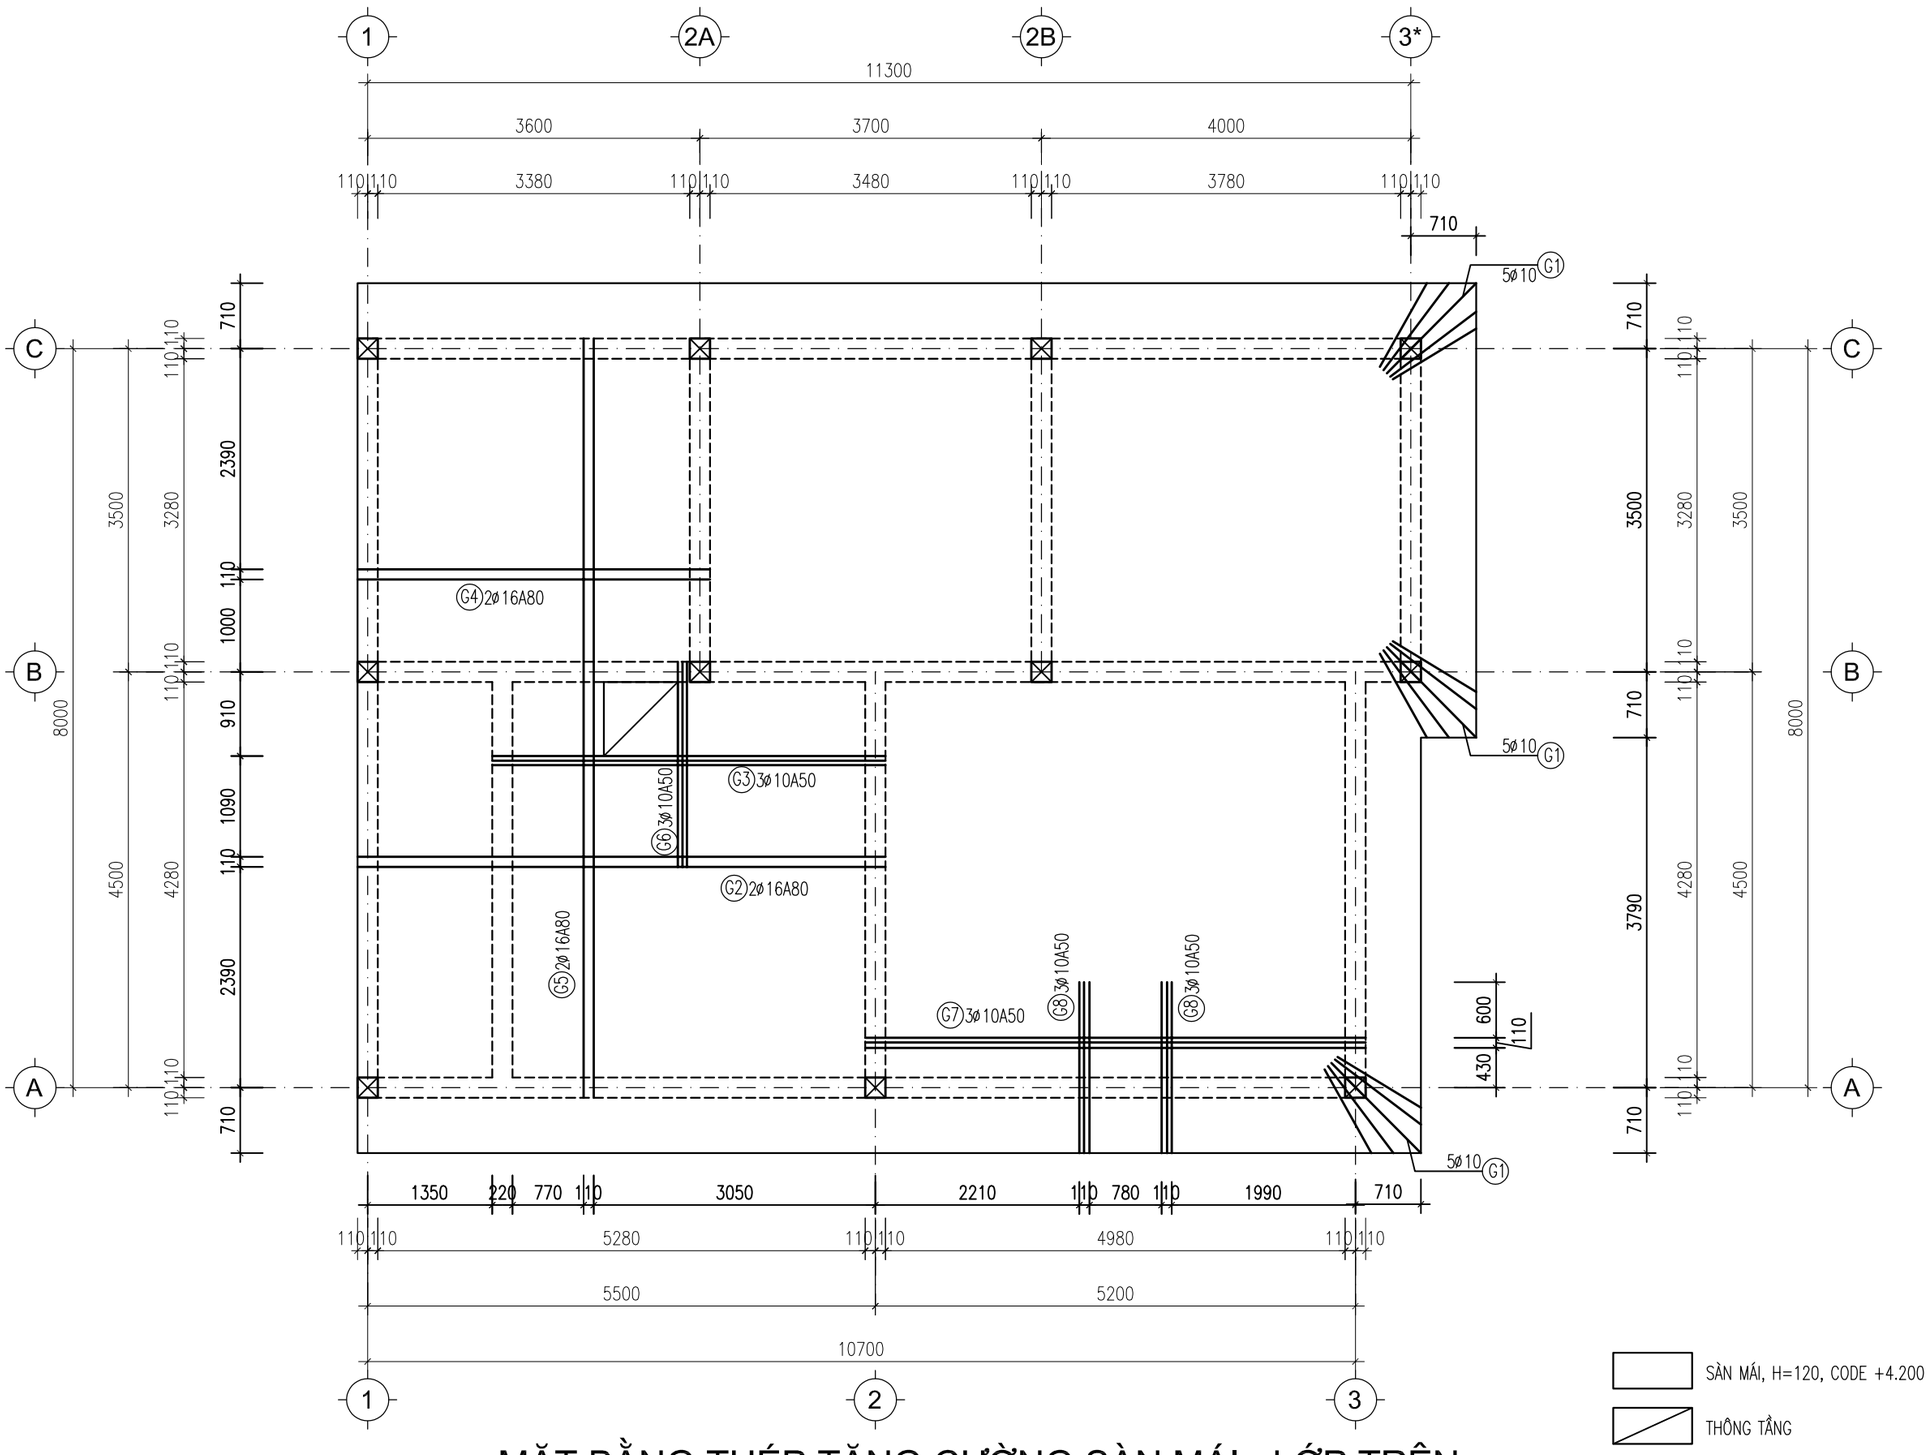

MẶT BẰNG THÉP TĂNG CƯỜNG SÀN MÁI - LỚP TRÊN

CHỦ ĐẦU TƯ CẦN YÊU CẦU KỸ SƯ HIỆN TRƯỜNG KIỂM TRA - RÀ SOÁT BẢN VẼ TRƯỚC KHI THI CÔNG
NẾU CÓ THẮC MẮC VUI LÒNG LIÊN HỆ KIẾN TRÚC SƯ - KỸ SƯ THIẾT KẾ ĐỂ CÓ TƯ VẤN KỊP THỜI TRƯỚC KHI KHỞI CÔNG

HỖ TRỢ TƯ VẤN KỸ THUẬT XÂY DỰNG : 0924099999
LIÊN HỆ MUA VẬT LIỆU MAXHOME : 0921845555 (MIỄN PHÍ VẬN CHUYỂN TOÀN QUỐC)

-BÊ TÔNG LÓT MÓNG ĐÁ 4X6, MÁC 100 -BÊ TÔNG MÓNG, MÁC 250	-BÊ TÔNG CỘT, DẦM, SÀN MÁC 250 -LỚP BÊ TÔNG BẢO VỆ SÀN: 15MM	-LỚP BÊ TÔNG BẢO VỆ CỐT THÉP DẦM: 25MM -LỚP BÊ TÔNG BẢO VỆ CỐT THÉP CỘT: 25MM	-THÉP CB240T (ø<10) KÝ HIỆU (ø) CÓ RA=2100KG/CM2 -THÉP CB300V (10=<ø<=20) KÝ HIỆU (ø) CÓ RA=2600KG/CM2	-THÉP CB300V (20<ø) KÝ HIỆU (ø) CÓ RA=2600KG/CM2 -CHIỀU DÀI THÉP NEO TẠI CÁC VỊ TRÍ LẤY BẰNG 30D	-CẮT NỐI UỐN CỐT THÉP THEO TCXDVN 5574-2018. -KHI THI CÔNG CẦN KẾT HỢP BẢN VẼ KIẾN TRÚC

CÔNG TY TNHH DESIGN AND CONSTRUCTION NEW MAXHOME
HÀ NỘI
ĐC : TẦNG 25, TÒA NHÀ VP TTTM CHỢ MƠ
SỐ 459C PHỐ BẠCH MAI, P. BẠCH MAI
THÀNH PHỐ HÀ NỘI
TEL: 0964458888 - 0828133333

Chủ đầu tư:

NGUYỄN THỊ ÁNH NGUYỆT

Địa điểm:

NAM HỒNG - HÀ TĨNH

Tên công trình:

NHÀ Ở GIA ĐÌNH

HỢP ĐỒNG SỐ /HĐ-TK/20.....

CHỦ NHIỆM THIẾT KẾ KTS: NGUYỄN VĂN CƯỜNG	
TRIỂN KHAI KS: HÀNG A LAO	
KIỂM DUYỆT KTS: NGUYỄN TẤT HỘI	

NỘI DUNG ĐIỀU CHỈNH

Lần	Ngày	Duyệt
1	.....	.....
2	.....	.....
3	.....	.....
4	.....	.....
5	.....	.....
6	.....	.....
7	.....	.....

Hạng mục:

KẾT CẤU

Tên bản vẽ:

MB THÉP SÀN MÁI

	Hà Nội, 12-2025
Phát hành lần 01	Thiết kế
.....	**KC-05-04**

BẢNG THỐNG KÊ CỐT THÉP

TÊN C.KIỆN	SỐ HIỆU	HÌNH DẠNG - KÍCH THƯỚC	ĐƯỜNG KÍNH (mm)	CHIỀU DÀI 1 THANH (mm)	SỐ LƯỢNG		TỔNG CHIỀU DÀI (m)	TỔNG T.LƯỢNG (Kg)
					1 C.KIỆN	T.BỘ		
SÀN SẢNH / Số lượng: 1	1	100 | 3900 | 100	10	4100	14	14	57.4	35.39
	2	100 | 2150 | 100	10	2350	32	32	75.2	46.36
	3	100 | 2700 | 100	10	2900	41	41	118.9	73.31
	4	100 | 4950 | 100	10	5150	18	18	92.7	57.15
	G	100 | 1650 | 100	10	1850	28	28	51.8	31.94
SÀN MÁI-LT / Số lượng: 1	1	100 | 11450 | 100	10	11650	20	20	233	143.65
	2	100 | 2600 | 100	10	2800	4	4	11.2	6.91
	3	100 | 8000 | 100	10	8200	4	4	32.8	20.22
	4	100 | 12050 | 100	10	12550	19	19	238.45	147.01
	5	100 | 9350 | 100	10	9550	50	50	477.5	294.40
	6	100 | 4250 | 100	10	4450	4	4	17.8	10.97
	7	100 | 4250 | 100	10	4450	4	4	17.8	10.97
	8	100 | 4850 | 100	10	5050	3	3	15.15	9.34
	G1	100 | 1350 | 100	10	1550	15	15	23.25	14.33
	G2	100 | 5650 | 100	16	5850	2	2	11.7	18.47
	G3	100 | 4200 | 100	10	4400	3	3	13.2	8.14
	G4	100 | 3750 | 100	16	3950	2	2	7.9	12.47
	G5	100 | 8150 | 100	16	8350	2	2	16.7	26.36
	G6	100 | 2150 | 100	10	2350	3	3	7.05	4.35
	G7	100 | 5350 | 100	10	5550	3	3	16.65	10.27
	G8	100 | 1800 | 100	10	2000	6	6	12	7.40
SÀN MÁI-LD / Số lượng: 1	1	11450	10	11450	20	20	229	141.19
	2	2600	10	2600	4	4	10.4	6.41
	3	8000	10	8000	4	4	32	19.73
	4	12050	10	12350	19	19	234.65	144.67
	5	9350	10	9350	50	50	467.5	288.23
	6	4250	10	4250	4	4	17	10.48
	7	4250	10	4250	4	4	17	10.48
	8	4850	10	4850	3	3	14.55	8.97

- Trọng lượng thép có đường kính Φ10 = 1562.27 kg; Chiều dài = 2533.95 mét
- Trọng lượng thép có đường kính Φ16 = 57.3 kg; Chiều dài = 36.3 mét

CHỦ ĐẦU TƯ CẦN YÊU CẦU KỸ SƯ HIỆN TRƯỜNG KIỂM TRA - RÀ SOÁT BẢN VẼ TRƯỚC KHI THI CÔNG
NẾU CÓ THẮC MẮC VUI LÒNG LIÊN HỆ KIẾN TRÚC SƯ - KỸ SƯ THIẾT KẾ ĐỂ CÓ TƯ VẤN KỊP THỜI TRƯỚC KHI KHỞI CÔNG

HỖ TRỢ TƯ VẤN KỸ THUẬT XÂY DỰNG : 0924099999
LIÊN HỆ MUA VẬT LIỆU MAXHOME : 0921845555 (MIỄN PHÍ VẬN CHUYỂN TOÀN QUỐC)

-BÊ TÔNG LÓT MÓNG ĐÁ 4X6, MÁC 100
-BÊ TÔNG MÓNG, MÁC 250
-BÊ TÔNG CỘT, DẦM, SÀN MÁC 250
-LỚP BÊ TÔNG BẢO VỆ SÀN: 15MM
-LỚP BÊ TÔNG BẢO VỆ CỐT THÉP DẦM: 25MM
-LỚP BÊ TÔNG BẢO VỆ CỐT THÉP CỘT: 25MM
-THÉP CB240T (Φ<10) KÝ HIỆU (Φ) CÓ RA=2100KG/CM2
-THÉP CB300V (10=<Φ<=20) KÝ HIỆU (Φ) CÓ RA=2600KG/CM2
-THÉP CB300V (20<Φ) KÝ HIỆU (Φ) CÓ RA=2600KG/CM2
-CHIỀU DÀI THÉP NEO TẠI CÁC VỊ TRÍ LẤY BẰNG 30D
-CẮT NỐI UỐN CỐT THÉP THEO TCXDVN 5574-2018.
-KHI THI CÔNG CẦN KẾT HỢP BẢN VẼ KIẾN TRÚC

CÔNG TY TNHH DESIGN AND CONSTRUCTION NEW MAXHOME
HÀ NỘI
ĐC : TẦNG 25, TÒA NHÀ VP TTTM CHỢ MƠ
SỐ 459C PHỐ BẠCH MAI, P. BẠCH MAI
THÀNH PHỐ HÀ NỘI
TEL: 0964458888 - 0828133333

Chủ đầu tư:
NGUYỄN THỊ ÁNH NGUYỆT
Địa điểm:
NAM HỒNG - HÀ TĨNH

Tên công trình:
NHÀ Ở GIA ĐÌNH

HỢP ĐỒNG SỐ /HĐ-TK/20.....

CHỦ NHIỆM THIẾT KẾ	
KTS: NGUYỄN VĂN CƯỜNG	
TRIỂN KHAI	
KS: HÀNG A LÁO	
KIỂM DUYỆT	
KTS: NGUYỄN TÁ HỘI	

NỘI DUNG ĐIỀU CHỈNH

Lần	Ngày	Duyệt
1	.....	.....
2	.....	.....
3	.....	.....
4	.....	.....
5	.....	.....
6	.....	.....
7	.....	.....

Hạng mục:
KẾT CẤU

Tên bản vẽ:
TK THÉP SÀN

Phát hành lần 01	Hà Nội, 12-2025
	Thiết kế
.....	**KC-05-05**

A. TẢI TRỌNG THIẾT KẾ

1. Tĩnh tải mái: 50kg/m2
2. Hoạt tải mái: 30kg/m2
3. Áp lực gió tiêu chuẩn: 55 kg/m2 ,địa hình I-A
4. Phụ tải theo trần: 10kg/m2

B.TIÊU CHUẨN THIẾT KẾ

Các tiêu chuẩn thiết kế áp dụng cho hệ kèo thép EURO-TRUSS như sau:

1.Tiêu chuẩn tải trọng áp dụng: TCVN- 2737/1995;
2.Tiêu chuẩn Việt Nam TCVN 5575:2012,Thiết kế kết cấu thép

C. PHẠM VI CUNG CẤP

1. Hệ giàn thép trọng lượng nhẹ mạ nhôm kẽm
   - Thanh cánh trên C75.75
   - Thanh cánh dưới C75.75
   - Thanh chống đứng, chống xiên C75.75
2. Vít tự khoan xi 7 màu 12-14*20
3. Bulong neo M10*100
4. Phụ kiện L
5. Phụ kiện hip
6. Bát đỉnh kèo

D. PHẠM VI KHÔNG CUNG CẤP

- Các phần việc xây tô dầm bê tông mái và các hạng mục khác không được ghi trong thiết kế này.

NHỮNG QUI ĐỊNH CHUNG

A. KIỂM TRA

1. Phải kiểm tra kích thước trước khi gia công lắp dựng kèo đảm bảo điều chỉnh yêu cầu kết cấu và kiến trúc.
2. Tất cả các chi tiết của giàn vì kèo phải đảm bảo được đặt đúng theo qui cách bản vẽ chi tiết.

B. LẮP DỰNG


1. Tất cả các kèo phải được lắp ráp đúng theo bản vẽ thiết kế.
2. Việc tiến hành lắp dựng phải thực hiện đúng theo qui trình lắp dựng của nhà sản xuất.

C. GIẰNG MÁI


Tất cả các kèo phải được giằng tạm thời trong quá trình lắp dựng và giằng cố định hoàn chỉnh theo bản vẽ thiết kế

D. LỢP MÁI


1. Khi chất ngói lên mái mỗi chồng không được đặt quá 6 viên nếu đặt trên giàn chính (tại vị trí kèo),không được đặt quá 4 viên nếu đặt ngói nằm ở khoảng giữa 2 kèo (đặt ngói nằm trên mè)
2.Các chồng ngói phải được đặt so le và rải điều trên toàn bộ diện tích mái.
3.Chồng ngói không được để qua đêm trên mái.

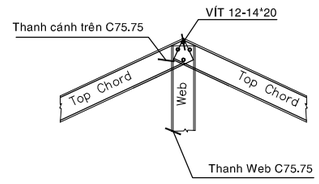


CHI TIẾT LIÊN KẾT ĐỈNH KÈO

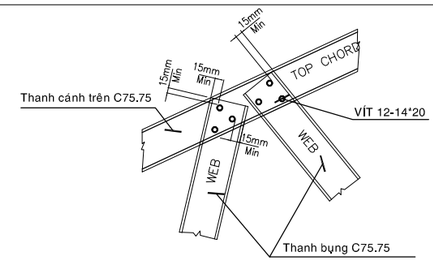


CHI TIẾT LIÊN KẾT CÁNH KÈO

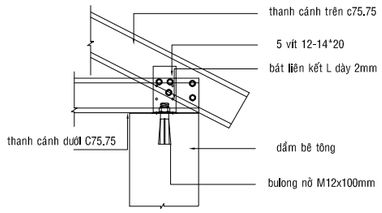



CHI TIẾT LIÊN KẾT CHÂN KÈO

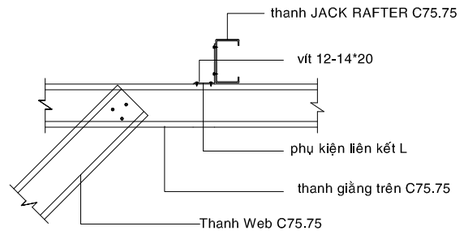


CHI TIẾT LIÊN KẾT HIP

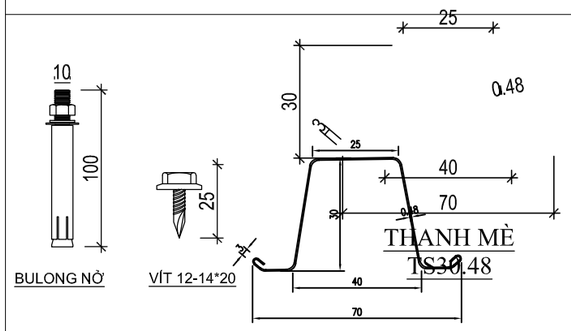

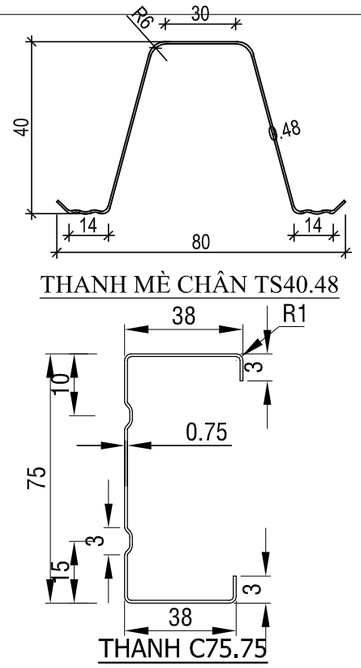


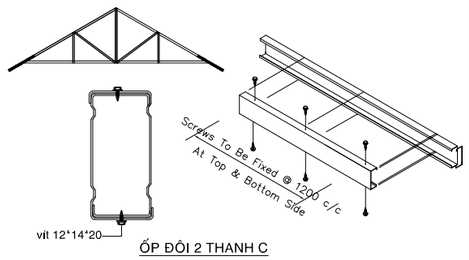


ỐP ĐÔI 2 THANH C

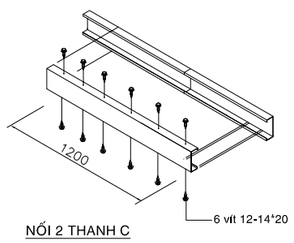

NỐI 2 THANH C

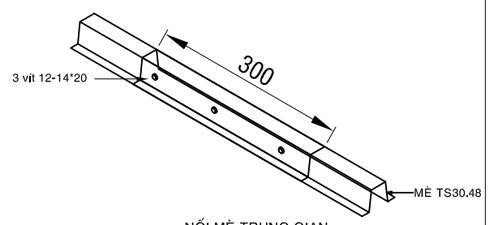

NỐI MÈ TRUNG GIAN

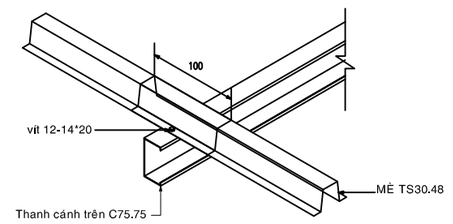

NỐI MÈ TRÊN ĐẦU C

CHI TIẾT VẬT TƯ & LIÊN KẾT

CHỦ ĐẦU TƯ CẦN YÊU CẦU KỸ SƯ HIỆN TRƯỜNG KIỂM TRA - RÀ SOÁT BẢN VẼ TRƯỚC KHI THI CÔNG
NẾU CÓ THẮC MẮC VUI LÒNG LIÊN HỆ KIẾN TRÚC SƯ - KỸ SƯ THIẾT KẾ ĐỂ CÓ TƯ VẤN KỊP THỜI TRƯỚC KHI KHỞI CÔNG

HỖ TRỢ TƯ VẤN KỸ THUẬT XÂY DỰNG : 0924099999
LIÊN HỆ MUA VẬT LIỆU MAXHOME : 0921845555 (MIỄN PHÍ VẬN CHUYỂN TOÀN QUỐC)

-BÊ TÔNG LÓT MÓNG ĐÁ 4X6, MÁC 100 -BÊ TÔNG MÓNG, MÁC 250	-BÊ TÔNG CỘT, DẦM, SÀN MÁC 250 -LỚP BÊ TÔNG BẢO VỆ SÀN: 15MM	-LỚP BÊ TÔNG BẢO VỆ CỐT THÉP DẦM: 25MM -LỚP BÊ TÔNG BẢO VỆ CỐT THÉP CỘT: 25MM	-THÉP CB240T (ø<10) KÝ HIỆU (ø) CÓ RA=2100KG/CM2 -THÉP CB300V (10=<ø<=20) KÝ HIỆU (ø) CÓ RA=2600KG/CM2	-THÉP CB300V (20<ø) KÝ HIỆU (ø) CÓ RA=2600KG/CM2 -CHIỀU DÀI THÉP NEO TẠI CÁC VỊ TRÍ LẤY BẰNG 30D	-CẮT NỐI UỐN CỐT THÉP THEO TCXDVN 5574-2018. -KHI THI CÔNG CẦN KẾT HỢP BẢN VẼ KIẾN TRÚC

CÔNG TY TNHH DESIGN AND CONSTRUCTION NEW MAXHOME
HÀ NỘI
ĐC : TẦNG 25, TÒA NHÀ VP TTTM CHỢ MƠ
SỐ 459C PHỐ BẠCH MAI, P. BẠCH MAI
THÀNH PHỐ HÀ NỘI
TEL: 0964458888 - 0828133333

Chủ đầu tư:

NGUYỄN THỊ ÁNH NGUYỆT

Địa điểm:

NAM HỒNG - HÀ TĨNH

Tên công trình:

NHÀ Ở GIA ĐÌNH

HỢP ĐỒNG SỐ /HĐ-TK/20.....

CHỦ NHIỆM THIẾT KẾ KTS: NGUYỄN VĂN CƯỜNG	
TRIỂN KHAI KS: HÀNG A LAO	
KIỂM DUYỆT KTS: NGUYỄN TẤT HỘI	

NỘI DUNG ĐIỀU CHỈNH

Lần	Ngày	Duyệt
1	.....	.....
2	.....	.....
3	.....	.....
4	.....	.....
5	.....	.....
6	.....	.....
7	.....	.....


Hạng mục:

KẾT CẤU


Tên bản vẽ:

T.SỐ CHI TIẾT HỆ VÌ KÈO


	Hà Nội, 12-2025
Phát hành lần 01	Thiết kế
.....	**KC-06-01**

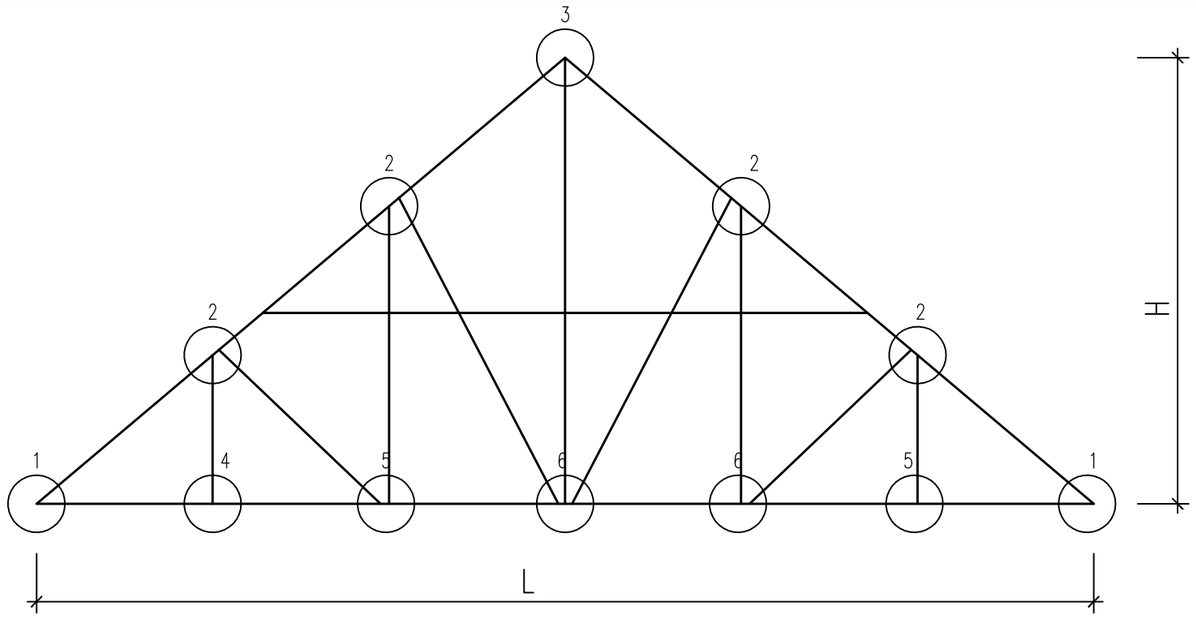


SƠ ĐỒ KÈO ĐIỂN HÌNH

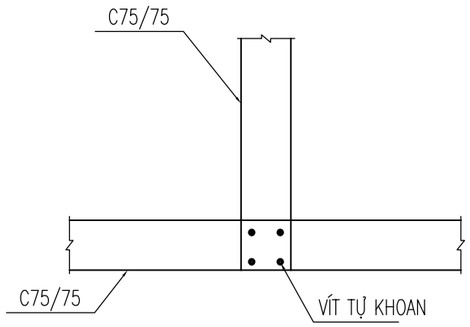


NÚT 04

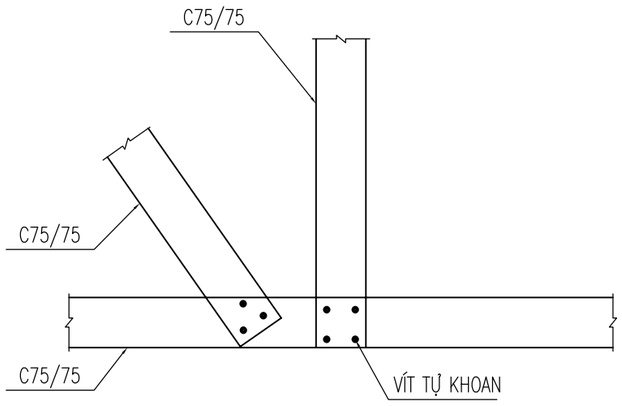


NÚT 05

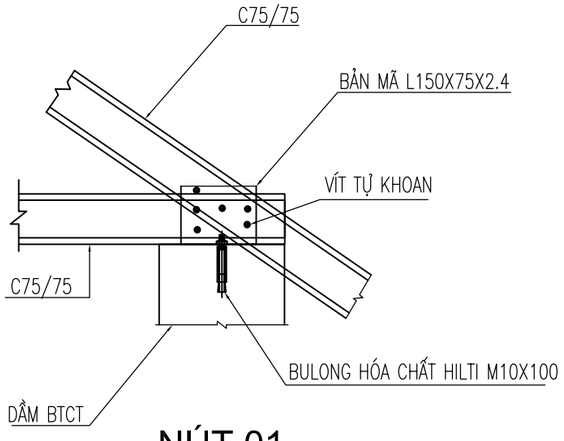


NÚT 01

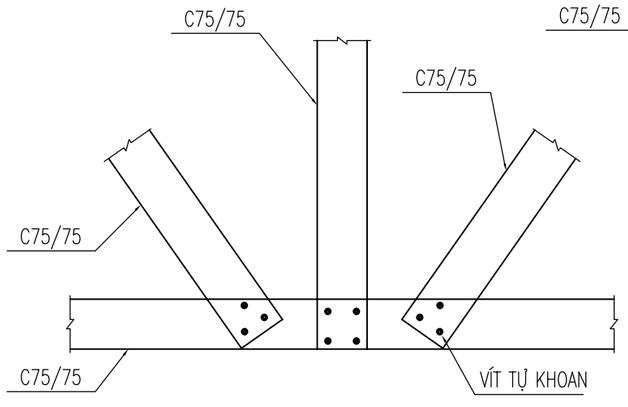

NÚT 06

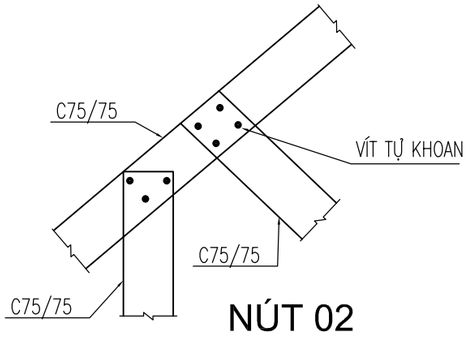

NÚT 02

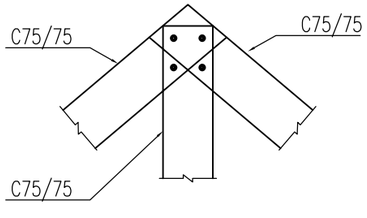

NÚT 03

CHỦ ĐẦU TƯ CẦN YÊU CẦU KỸ SƯ HIỆN TRƯỜNG KIỂM TRA - RÀ SOÁT BẢN VẼ TRƯỚC KHI THI CÔNG
NẾU CÓ THẮC MẮC VUI LÒNG LIÊN HỆ KIẾN TRÚC SƯ - KỸ SƯ THIẾT KẾ ĐỂ CÓ TƯ VẤN KỊP THỜI TRƯỚC KHI KHỞI CÔNG

HỖ TRỢ TƯ VẤN KỸ THUẬT XÂY DỰNG : 0924099999
LIÊN HỆ MUA VẬT LIỆU MAXHOME : 0921845555 (MIỄN PHÍ VẬN CHUYỂN TOÀN QUỐC)

-BÊ TÔNG LÓT MÓNG ĐÁ 4X6, MÁC 100 -BÊ TÔNG MÓNG, MÁC 250	-BÊ TÔNG CỘT, DẦM, SÀN MÁC 250 -LỚP BÊ TÔNG BẢO VỆ SÀN: 15MM	-LỚP BÊ TÔNG BẢO VỆ CỐT THÉP DẦM: 25MM -LỚP BÊ TÔNG BẢO VỆ CỐT THÉP CỘT: 25MM	-THÉP CB240T (ø<10) KÝ HIỆU (ø) CÓ RA=2100KG/CM2 -THÉP CB300V (10=<ø<=20) KÝ HIỆU (ø) CÓ RA=2600KG/CM2	-THÉP CB300V (20<ø) KÝ HIỆU (ø) CÓ RA=2600KG/CM2 -CHIỀU DÀI THÉP NEO TẠI CÁC VỊ TRÍ LẤY BẰNG 30D	-CẮT NỐI UỐN CỐT THÉP THEO TCXDVN 5574-2018. -KHI THI CÔNG CẦN KẾT HỢP BẢN VẼ KIẾN TRÚC

CÔNG TY TNHH DESIGN AND CONSTRUCTION NEW MAXHOME
HÀ NỘI
ĐC : TẦNG 25, TÒA NHÀ VP TTTM CHỢ MƠ
SỐ 459C PHỐ BẠCH MAI, P. BẠCH MAI
THÀNH PHỐ HÀ NỘI
TEL: 0964458888 - 0828133333

Chủ đầu tư:
NGUYỄN THỊ ÁNH NGUYỆT

Địa điểm:
NAM HỒNG - HÀ TĨNH

Tên công trình:
NHÀ Ở GIA ĐÌNH

HỢP ĐỒNG SỐ /HĐ-TK/20.....

CHỦ NHIỆM THIẾT KẾ KTS: NGUYỄN VĂN CƯỜNG	
TRIỂN KHAI KS: HÀNG A LAO	
KIỂM DUYỆT KTS: NGUYỄN TẤT HỘI	

NỘI DUNG ĐIỀU CHỈNH


Lần	Ngày	Duyệt
1	.....	.....
2	.....	.....
3	.....	.....
4	.....	.....
5	.....	.....
6	.....	.....
7	.....	.....


Hạng mục:
KẾT CẤU


Tên bản vẽ:
CHI TIẾT HỆ VÌ KÈO


	Hà Nội, 12-2025
Phát hành lần 01	Thiết kế
.....	**KC-06-02**

GHI CHÚ:
TOÀN BỘ KHUNG KÈO TỔ HỢP BẰNG THANH TC75.75,
LITO (MÈ MÓC NGÓI) SỬ DỤNG THANH TS35.48 ĐƯỢC CHIA ĐỀU TRÊN MÁI TỪ 330mm ĐẾN 360mm VÀ THEO QUY CÁCH CỦA NHÀ SẢN XUẤT

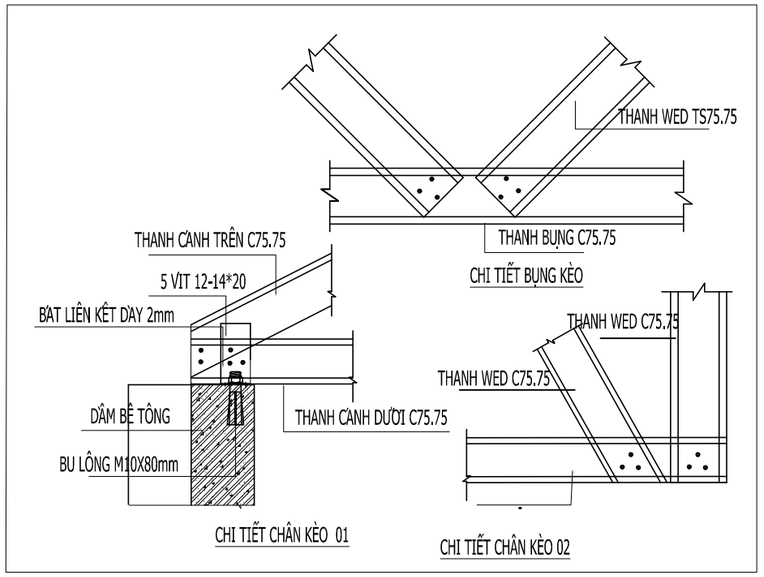

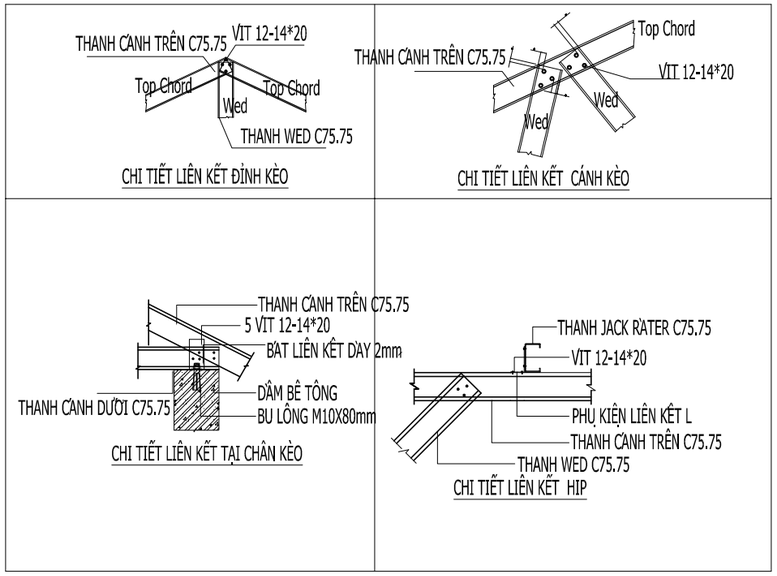

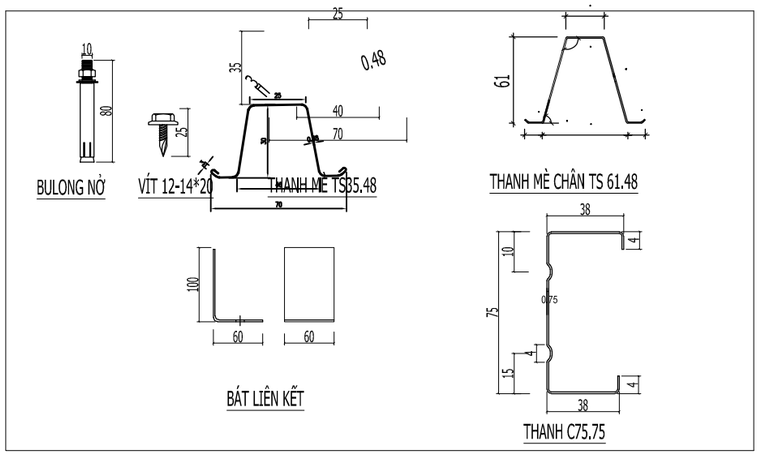

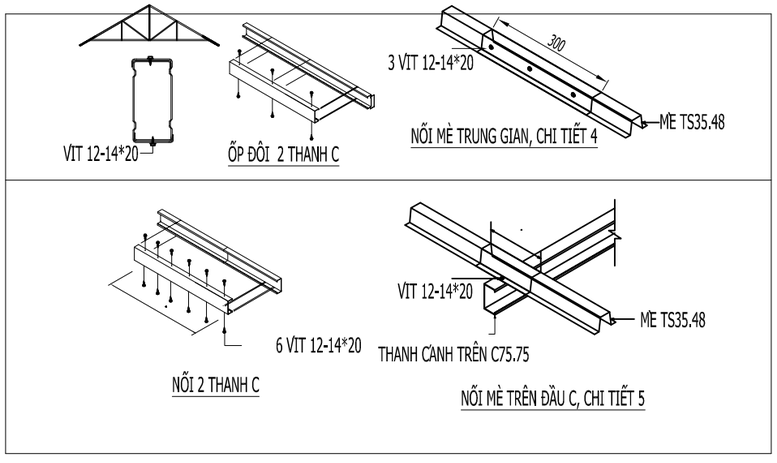

CHI TIẾT VẬT TƯ VÀ LIÊN KẾT

CHỦ ĐẦU TƯ CẦN YÊU CẦU KỸ SƯ HIỆN TRƯỜNG KIỂM TRA - RÀ SOÁT BẢN VẼ TRƯỚC KHI THI CÔNG
NẾU CÓ THẮC MẮC VUI LÒNG LIÊN HỆ KIẾN TRÚC SƯ - KỸ SƯ THIẾT KẾ ĐỂ CÓ TƯ VẤN KỊP THỜI TRƯỚC KHI KHỞI CÔNG

HỖ TRỢ TƯ VẤN KỸ THUẬT XÂY DỰNG : 0924099999
LIÊN HỆ MUA VẬT LIỆU MAXHOME : 0921845555 (MIỄN PHÍ VẬN CHUYỂN TOÀN QUỐC)

-BÊ TÔNG LÓT MÓNG ĐÁ 4X6, MÁC 100 -BÊ TÔNG MÓNG, MÁC 250	-BÊ TÔNG CỘT, DẦM, SÀN MÁC 250 -LỚP BÊ TÔNG BẢO VỆ SÀN: 15MM	-LỚP BÊ TÔNG BẢO VỆ CỐT THÉP DẦM: 25MM -LỚP BÊ TÔNG BẢO VỆ CỐT THÉP CỘT: 25MM	-THÉP CB240T (ø<10) KÝ HIỆU (ø) CÓ RA=2100KG/CM2 -THÉP CB300V (10=<ø<=20) KÝ HIỆU (ø) CÓ RA=2600KG/CM2	-THÉP CB300V (20<ø) KÝ HIỆU (ø) CÓ RA=2600KG/CM2 -CHIỀU DÀI THÉP NEO TẠI CÁC VỊ TRÍ LẤY BẰNG 30D	-CẮT NỐI UỐN CỐT THÉP THEO TCXDVN 5574-2018. -KHI THI CÔNG CẦN KẾT HỢP BẢN VẼ KIẾN TRÚC

CÔNG TY TNHH DESIGN AND CONSTRUCTION NEW MAXHOME
HÀ NỘI
ĐC : TẦNG 25, TÒA NHÀ VP TTTM CHỢ MƠ
SỐ 459C PHỐ BẠCH MAI, P. BẠCH MAI
THÀNH PHỐ HÀ NỘI
TEL: 0964458888 - 0828133333

Chủ đầu tư:
NGUYỄN THỊ ÁNH NGUYỆT

Địa điểm:
NAM HỒNG - HÀ TĨNH

Tên công trình:
NHÀ Ở GIA ĐÌNH

HỢP ĐỒNG SỐ /HĐ-TK/20.....

CHỦ NHIỆM THIẾT KẾ	
KTS: NGUYỄN VĂN CƯỜNG	
TRIỂN KHAI	
KS: HÀNG A LAO	
KIỂM DUYỆT	
KTS: NGUYỄN TẤT HỘI	

NỘI DUNG ĐIỀU CHỈNH


Lần	Ngày	Duyệt
1	.....	.....
2	.....	.....
3	.....	.....
4	.....	.....
5	.....	.....
6	.....	.....
7	.....	.....


Hạng mục:
KẾT CẤU

Tên bản vẽ:
T.SỐ CHI TIẾT HỆ VÌ KÈO


	Hà Nội, 12-2025
Phát hành lần 01	Thiết kế
.....	**KC-06-03**

GHI CHÚ:
TOÀN BỘ KHUNG KÈO TỔ HỢP BẰNG THANH TC75.75,
LITO (MÈ MÓC NGÓI) SỬ DỤNG THANH TS35.48 ĐƯỢC CHIA ĐỀU TRÊN MÁI TỪ 330mm ĐẾN 360mm VÀ THEO QUY CÁCH CỦA NHÀ SẢN XUẤT

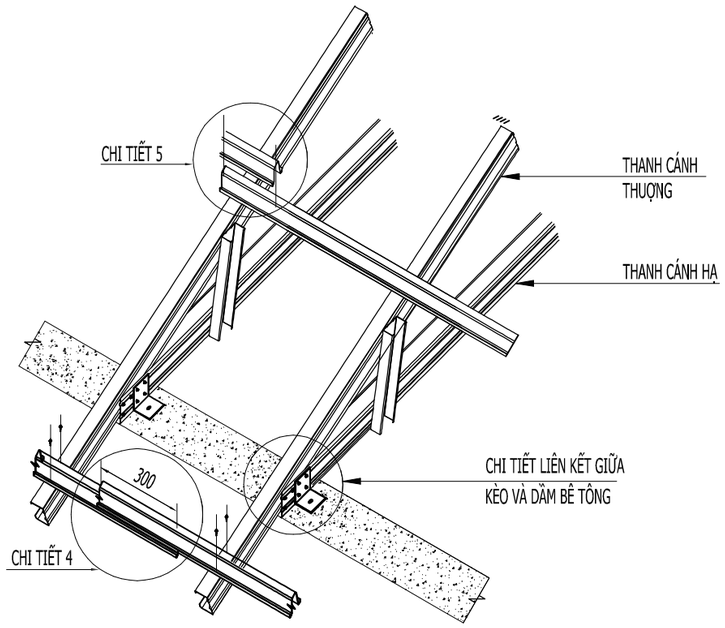


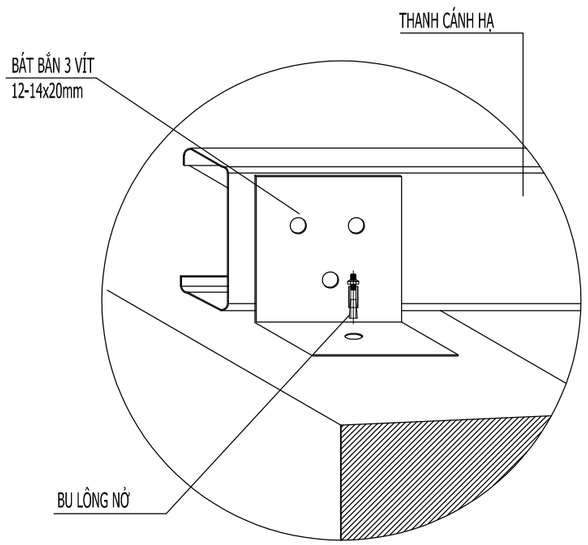


CHI TIẾT LIÊN KẾT KÈO VÀO DẦM

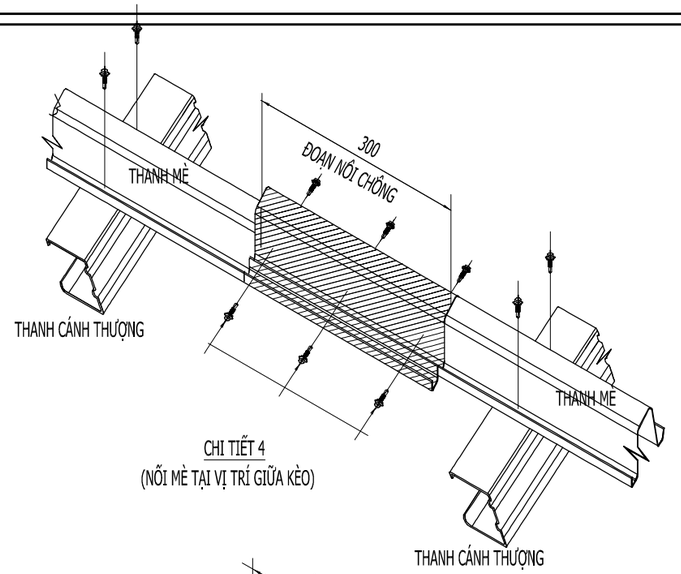



CHI TIẾT 4
(NỐI MÈ TẠI VỊ TRÍ GIỮA KÈO)

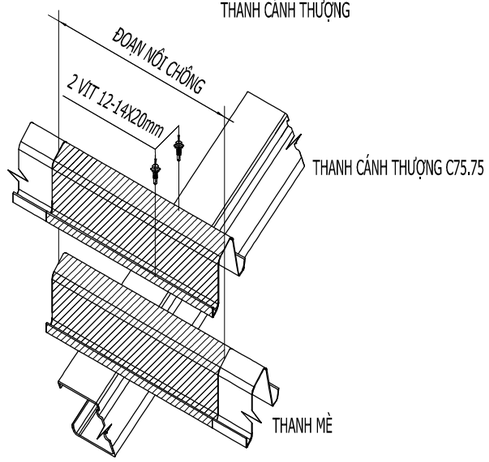

CHI TIẾT 5
(NỐI MÈ TẠI VỊ TRÍ KÈO)

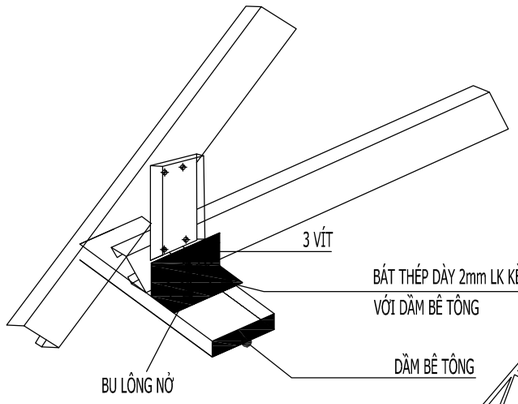

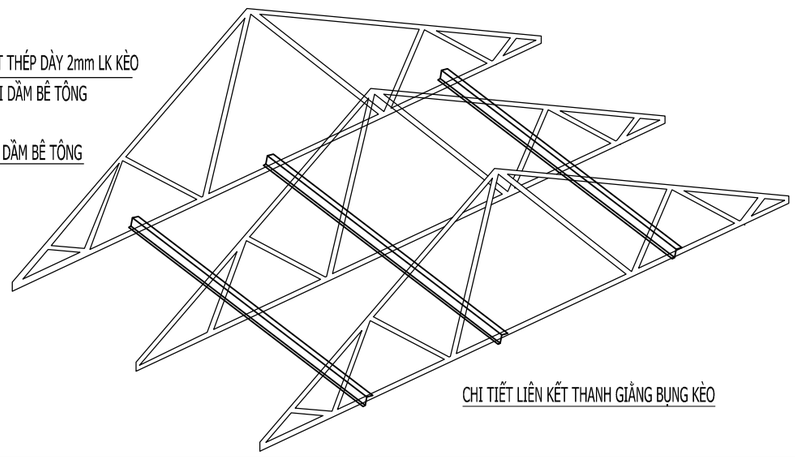
CHI TIẾT LIÊN KẾT THANH GIẰNG BỤNG KÈO

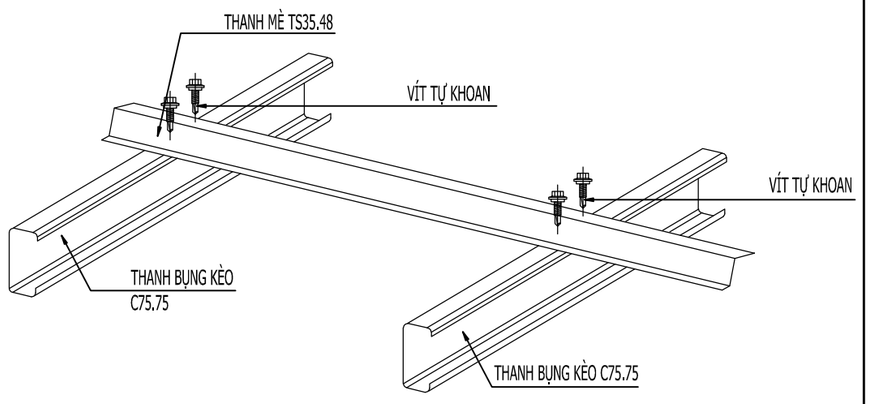

CHI TIẾT LIÊN KẾT

CHỦ ĐẦU TƯ CẦN YÊU CẦU KỸ SƯ HIỆN TRƯỜNG KIỂM TRA - RÀ SOÁT BẢN VẼ TRƯỚC KHI THI CÔNG
NẾU CÓ THẮC MẮC VUI LÒNG LIÊN HỆ KIẾN TRÚC SƯ - KỸ SƯ THIẾT KẾ ĐỂ CÓ TƯ VẤN KỊP THỜI TRƯỚC KHI KHỞI CÔNG

HỖ TRỢ TƯ VẤN KỸ THUẬT XÂY DỰNG : 0924099999
LIÊN HỆ MUA VẬT LIỆU MAXHOME : 0921845555 (MIỄN PHÍ VẬN CHUYỂN TOÀN QUỐC)

-BÊ TÔNG LÓT MÓNG ĐÁ 4X6, MÁC 100 -BÊ TÔNG MÓNG, MÁC 250	-BÊ TÔNG CỘT, DẦM, SÀN MÁC 250 -LỚP BÊ TÔNG BẢO VỆ SÀN: 15MM	-LỚP BÊ TÔNG BẢO VỆ CỐT THÉP DẦM: 25MM -LỚP BÊ TÔNG BẢO VỆ CỐT THÉP CỘT: 25MM	-THÉP CB240T (ø<10) KÝ HIỆU (ø) CÓ RA=2100KG/CM2 -THÉP CB300V (10=<ø<=20) KÝ HIỆU (ø) CÓ RA=2600KG/CM2	-THÉP CB300V (20<ø) KÝ HIỆU (ø) CÓ RA=2600KG/CM2 -CHIỀU DÀI THÉP NEO TẠI CÁC VỊ TRÍ LẤY BẰNG 30D	-CẮT NỐI UỐN CỐT THÉP THEO TCXDVN 5574-2018. -KHI THI CÔNG CẦN KẾT HỢP BẢN VẼ KIẾN TRÚC

CÔNG TY TNHH DESIGN AND CONSTRUCTION NEW MAXHOME
HÀ NỘI
ĐC : TẦNG 25, TÒA NHÀ VP TTTM CHỢ MƠ
SỐ 459C PHỐ BẠCH MAI, P. BẠCH MAI
THÀNH PHỐ HÀ NỘI
TEL: 0964458888 - 0828133333

Chủ đầu tư:
NGUYỄN THỊ ÁNH NGUYỆT

Địa điểm:
NAM HỒNG - HÀ TĨNH

Tên công trình:
NHÀ Ở GIA ĐÌNH

HỢP ĐỒNG SỐ /HĐ-TK/20.....

CHỦ NHIỆM THIẾT KẾ KTS: NGUYỄN VĂN CƯỜNG	
TRIỂN KHAI KS: HÀNG A LAO	
KIỂM DUYỆT KTS: NGUYỄN TẤT HỘI	

NỘI DUNG ĐIỀU CHỈNH

Lần	Ngày	Duyệt
1	.....	.....
2	.....	.....
3	.....	.....
4	.....	.....
5	.....	.....
6	.....	.....
7	.....	.....

Hạng mục:
KẾT CẤU

Tên bản vẽ:
T.SỐ CHI TIẾT HỆ VÌ KÈO

	Hà Nội, 12-2025
Phát hành lần 01	Thiết kế
.....	**KC-06-04**